



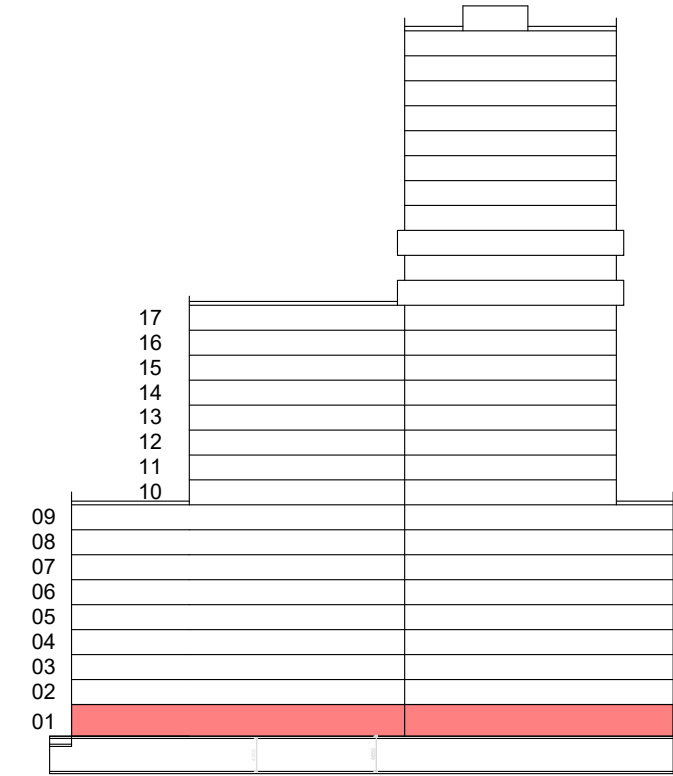


Инд. № подл.	Подп. и дата	Взам. инд. №

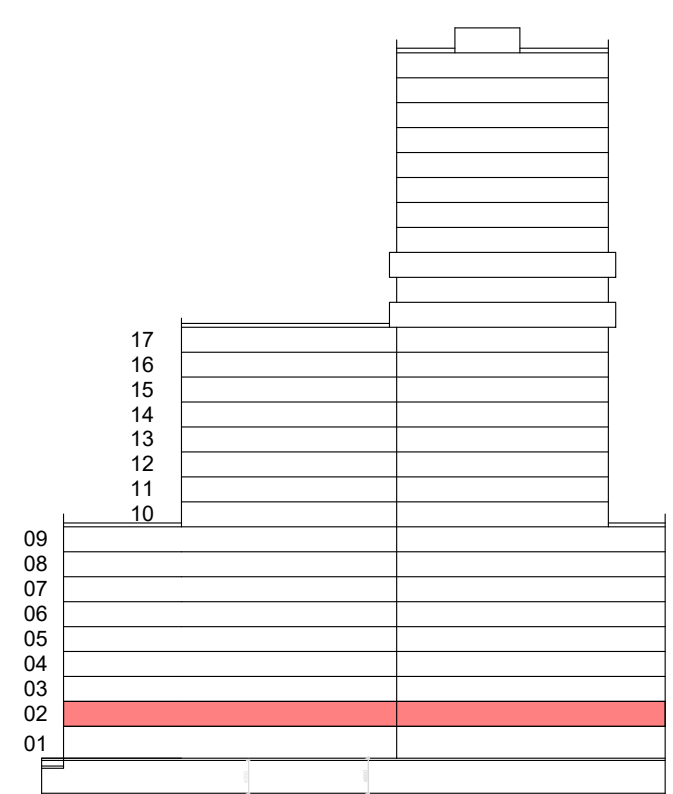


29
28
27
26
25
24
23
22
21
20
19
18
17
16
15
14
13
12
11
10
09
08
07
06
05
04
03
02
01
-1


						АР. К-1					
Иж.	Коллж.	Лист	Ф. док.	Подп.	Дата	Архитектурные решения Корпуса К-1			Страниц ЭП	Лист З	Листов
						План 2 этажа			Проектное бюро R1		

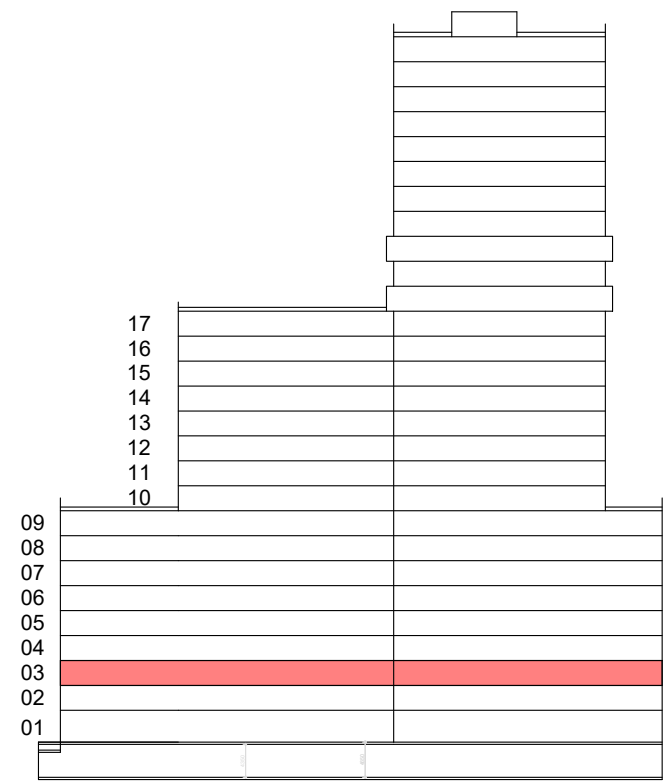


						АР. К-1					
Иж.	Коллж.	Лист	Ф. док.	Подп.	Дата	Архитектурные решения Корпуса К-1			Страниц ЭП	Лист 4	Листов
						План 3 этажа			Проектное бюро R1		

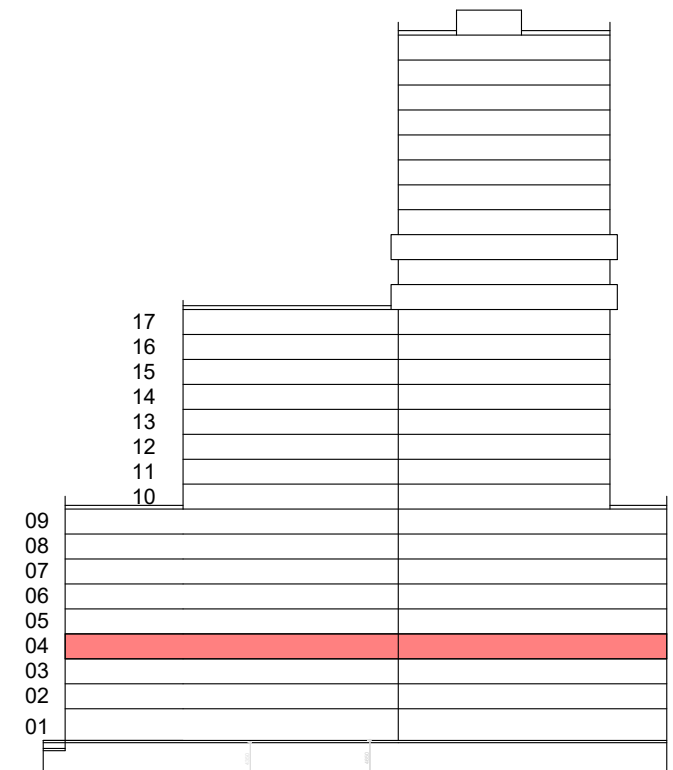


И-ф. № подл.	Подп. и дата	Взам. инв. №

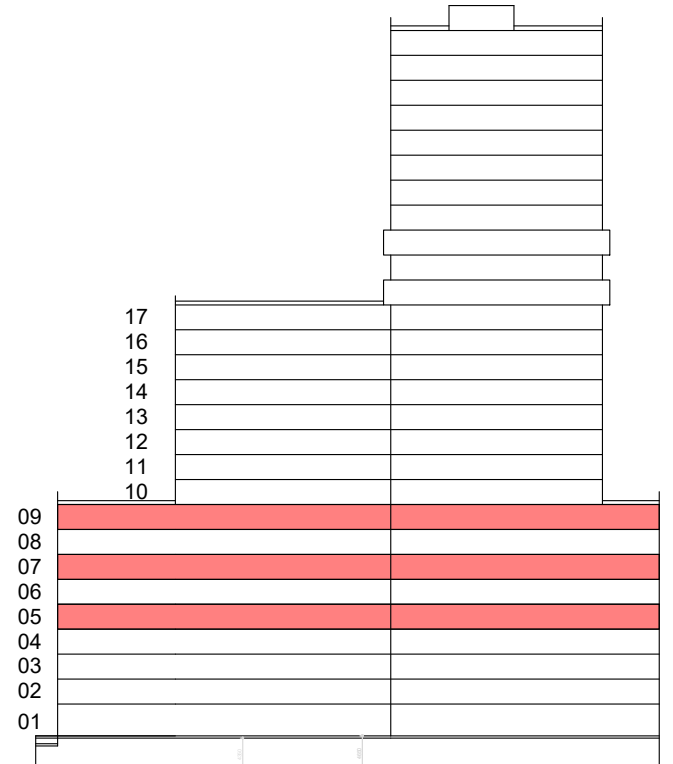


						АР. К-1		
Иж	Калж	Лист	Ф.Вж	Подп.	Дого			
Архитектурные решения. Глава 2. Планировочные решения						Стандарт ЭП	Лист 6	Листов
						Плани 5, 7, 9 этажа		

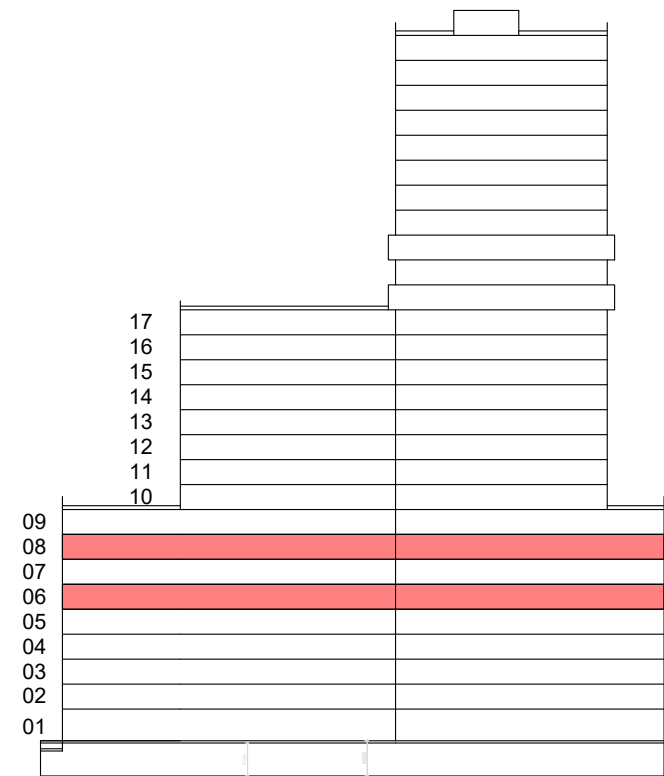


Инд. № подл.	Подп. и дата	Взам. инд. №

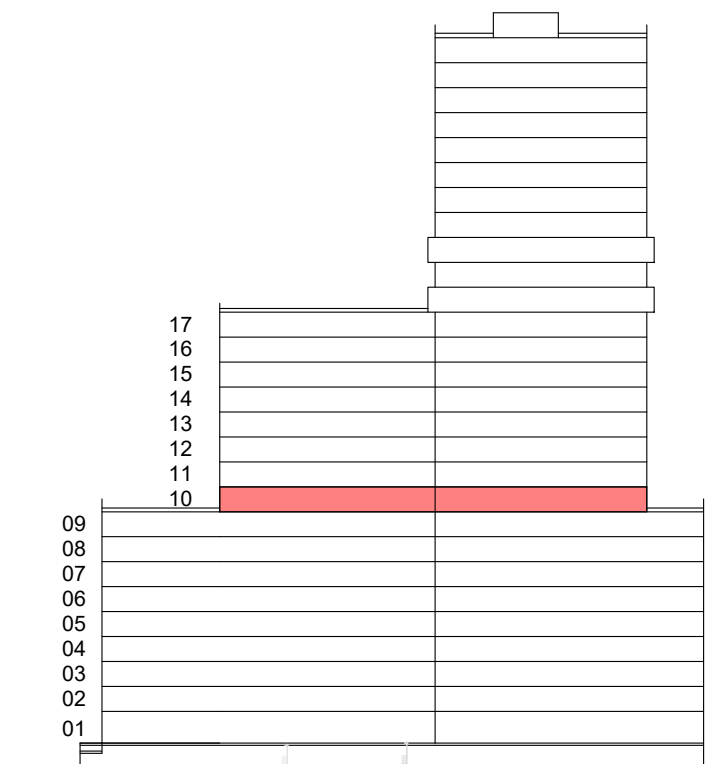


						АР. К-1		
Изм.	Кол-во	Лист	В док.	Подп.	Дата			
						Архитектурные решения. Глава 2. Планировочные решения		
						Страница ЭП	Лист 8	Листов
						План 10 этажа		Проектное бюро R1

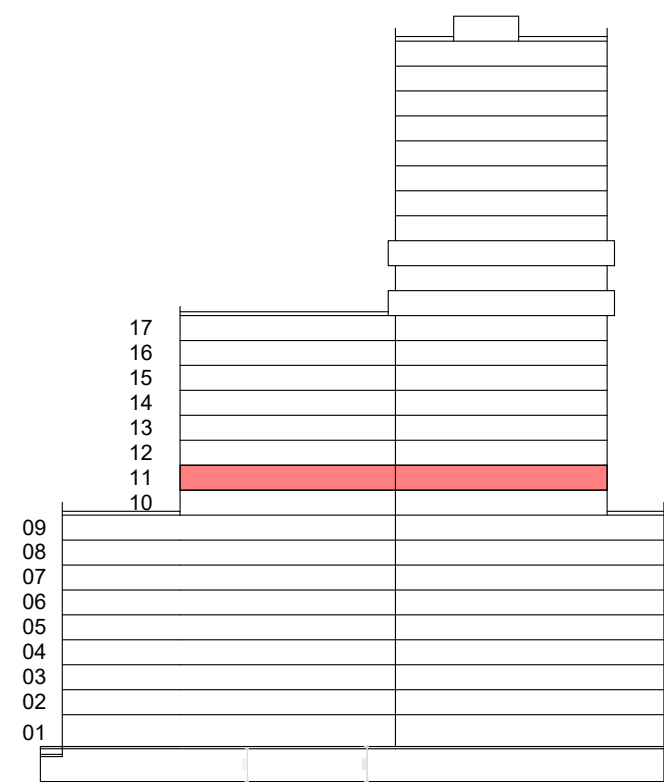


Инд. № подл.	Подп. и дата	Взам. инд. №


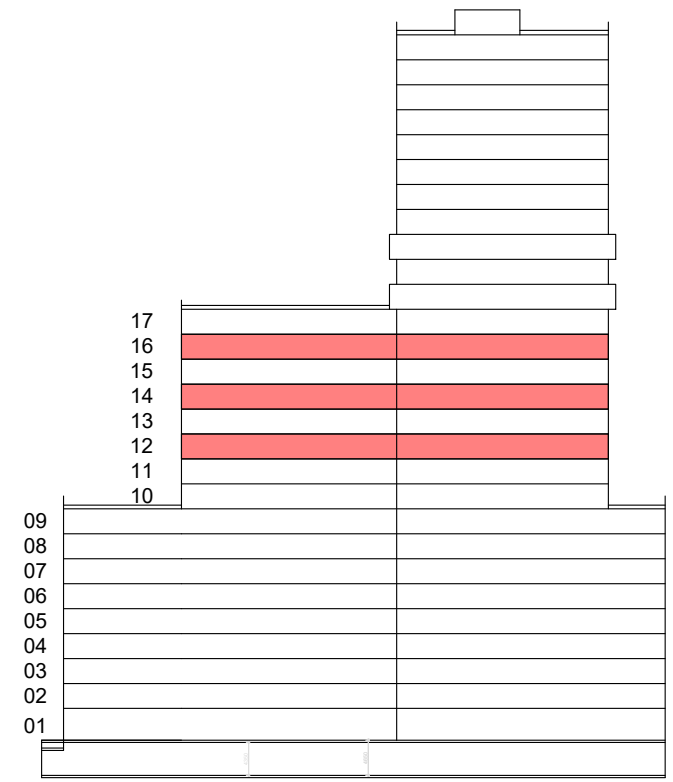


Формат: А4

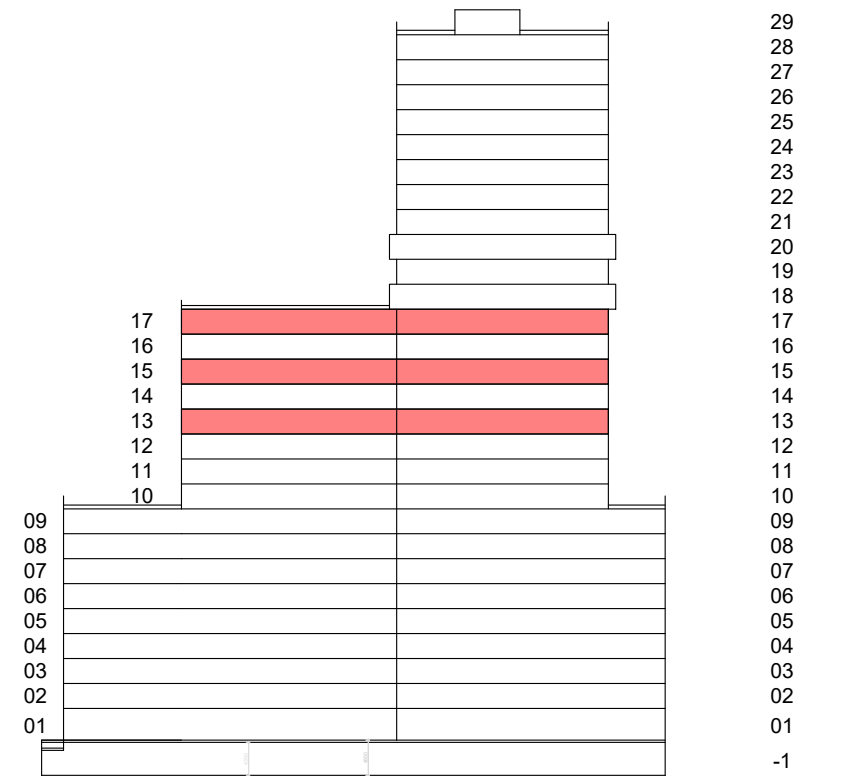

Инд. № подл.	Подп. и дата	Взам. инд. №

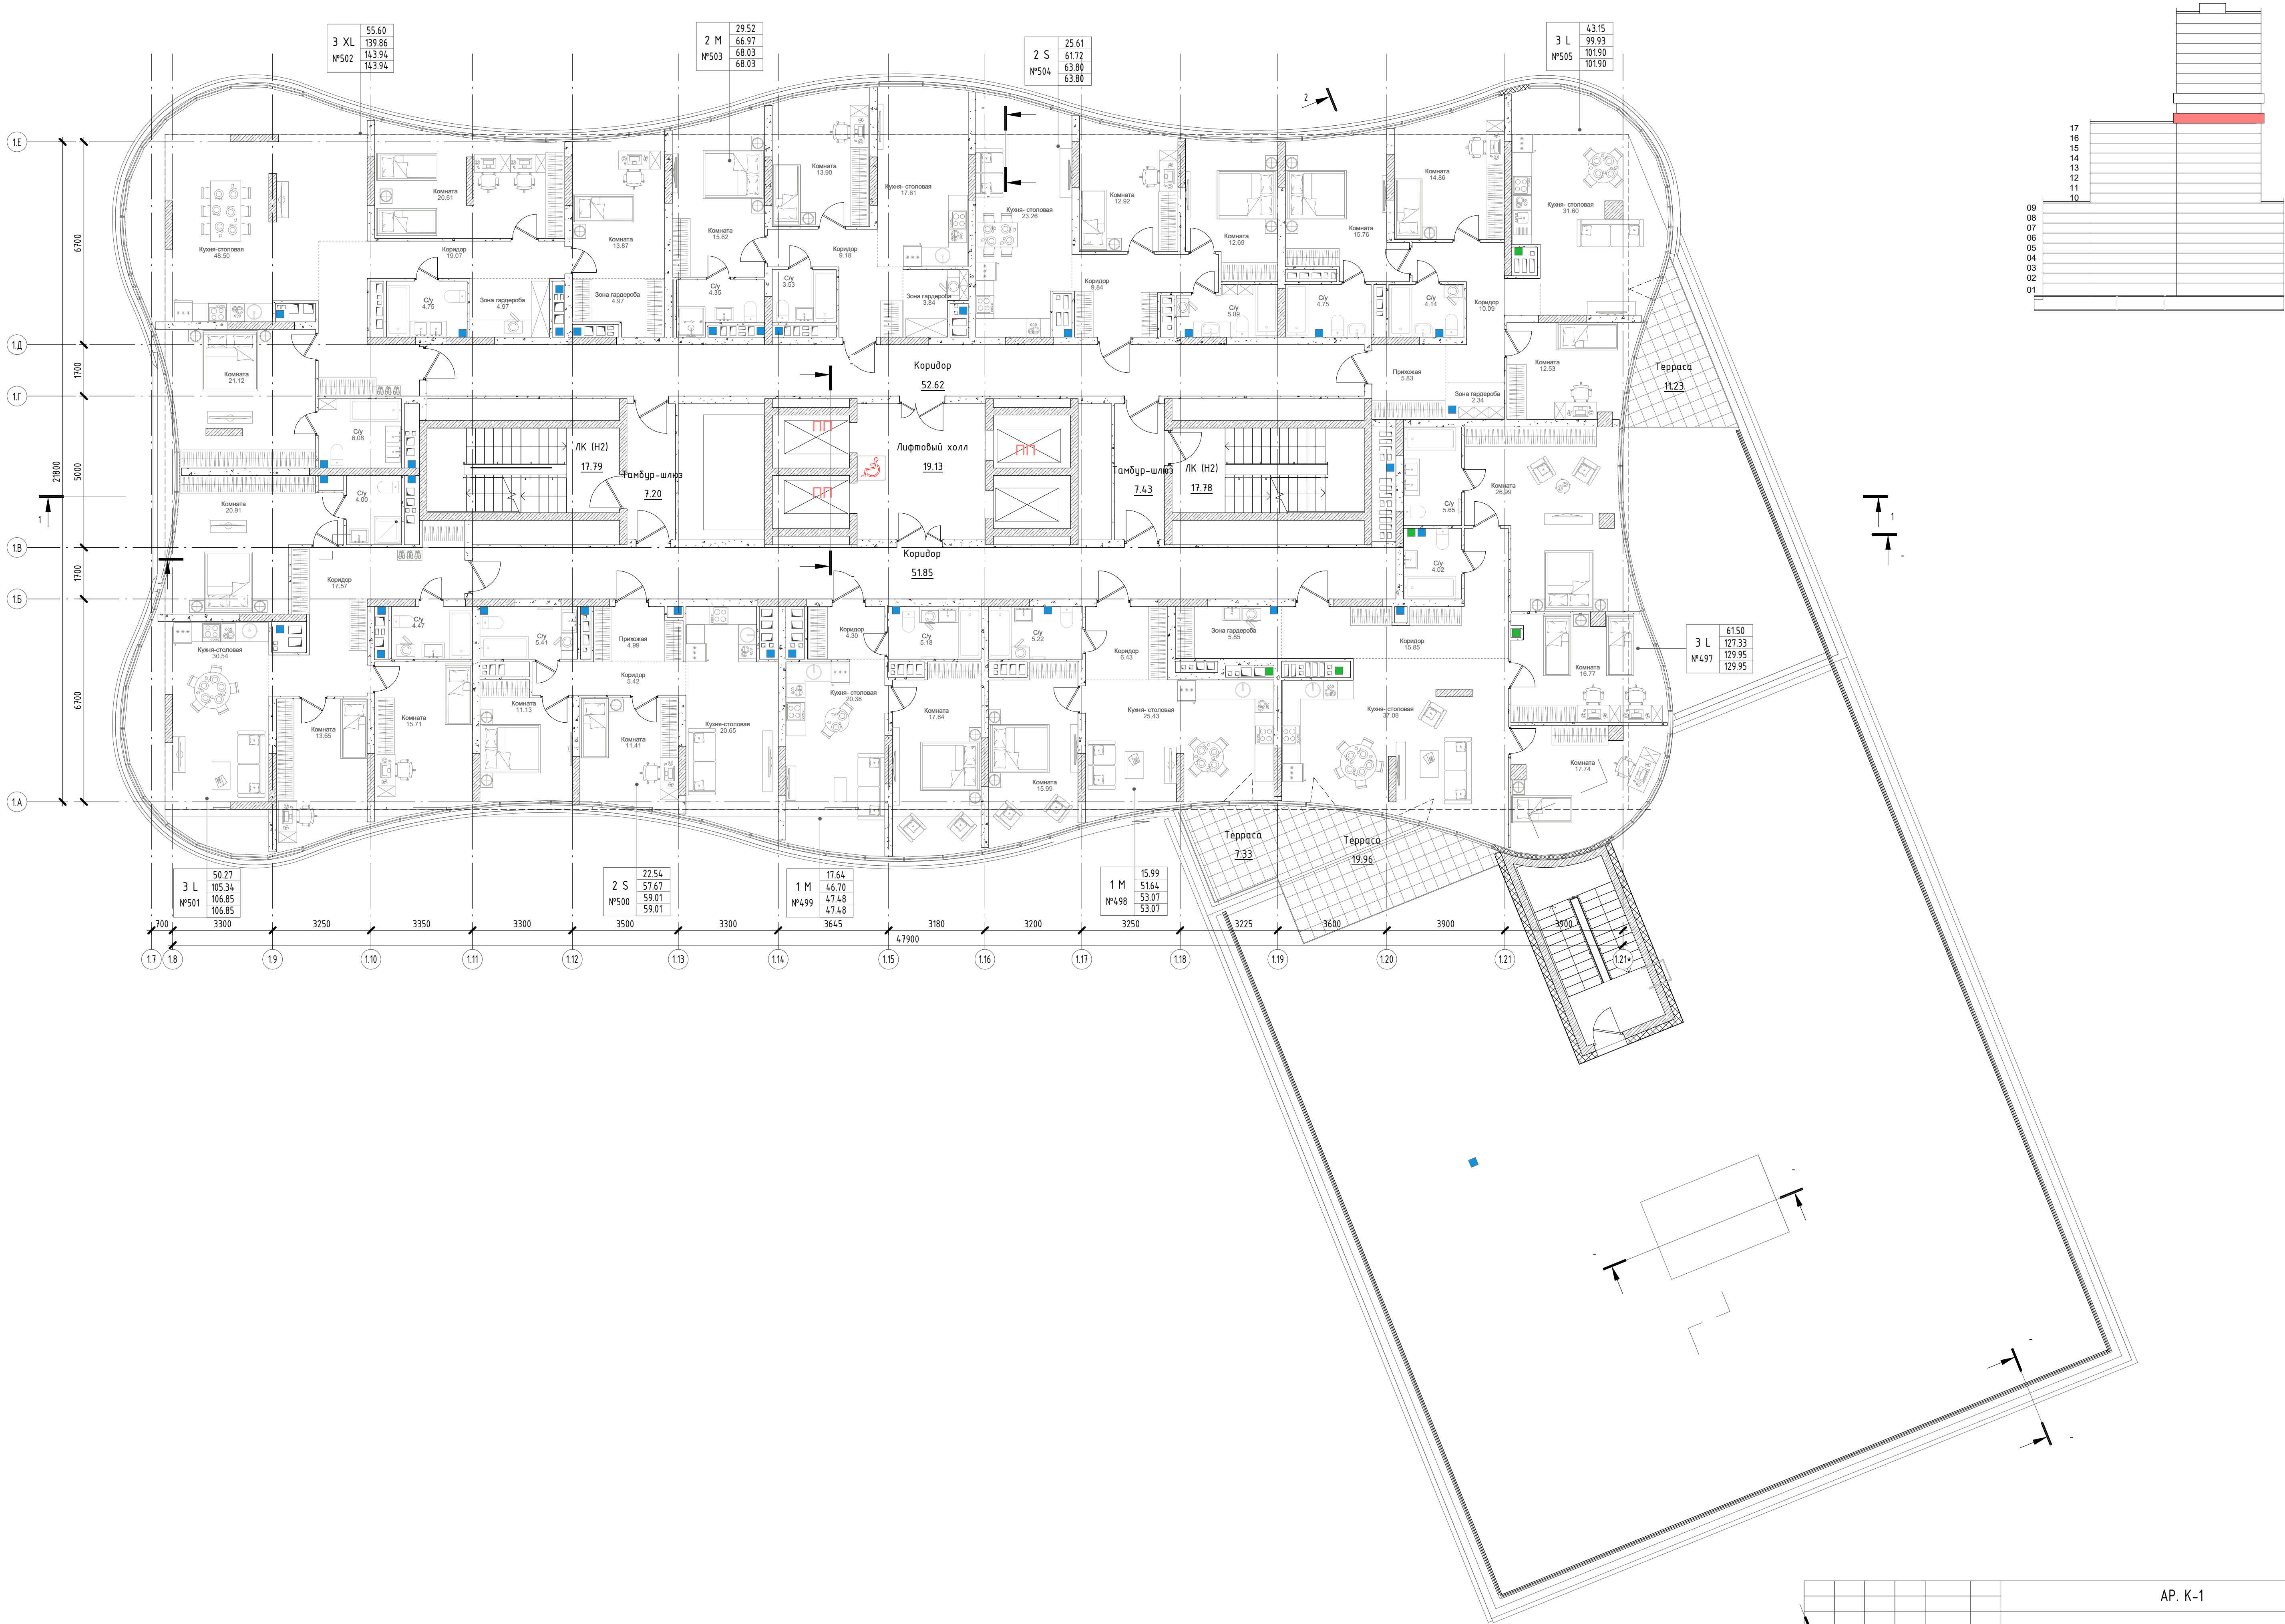

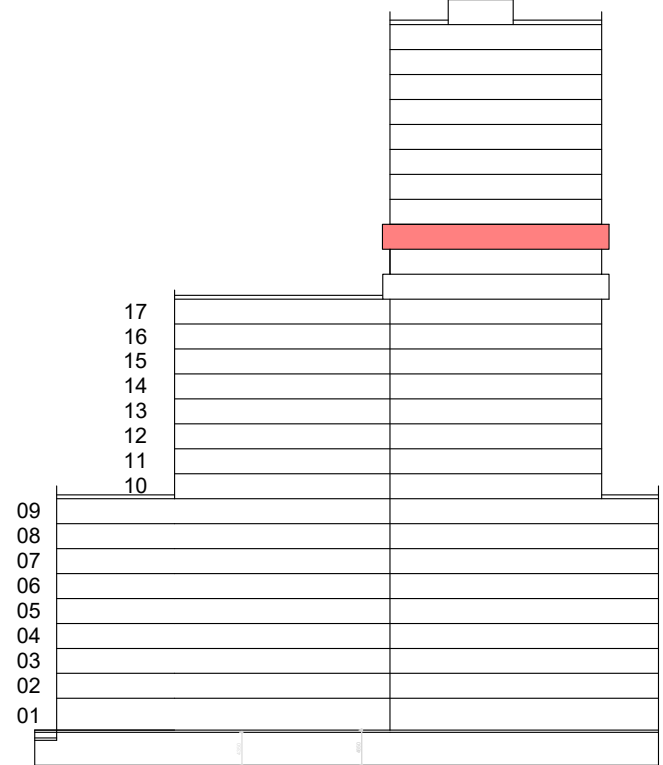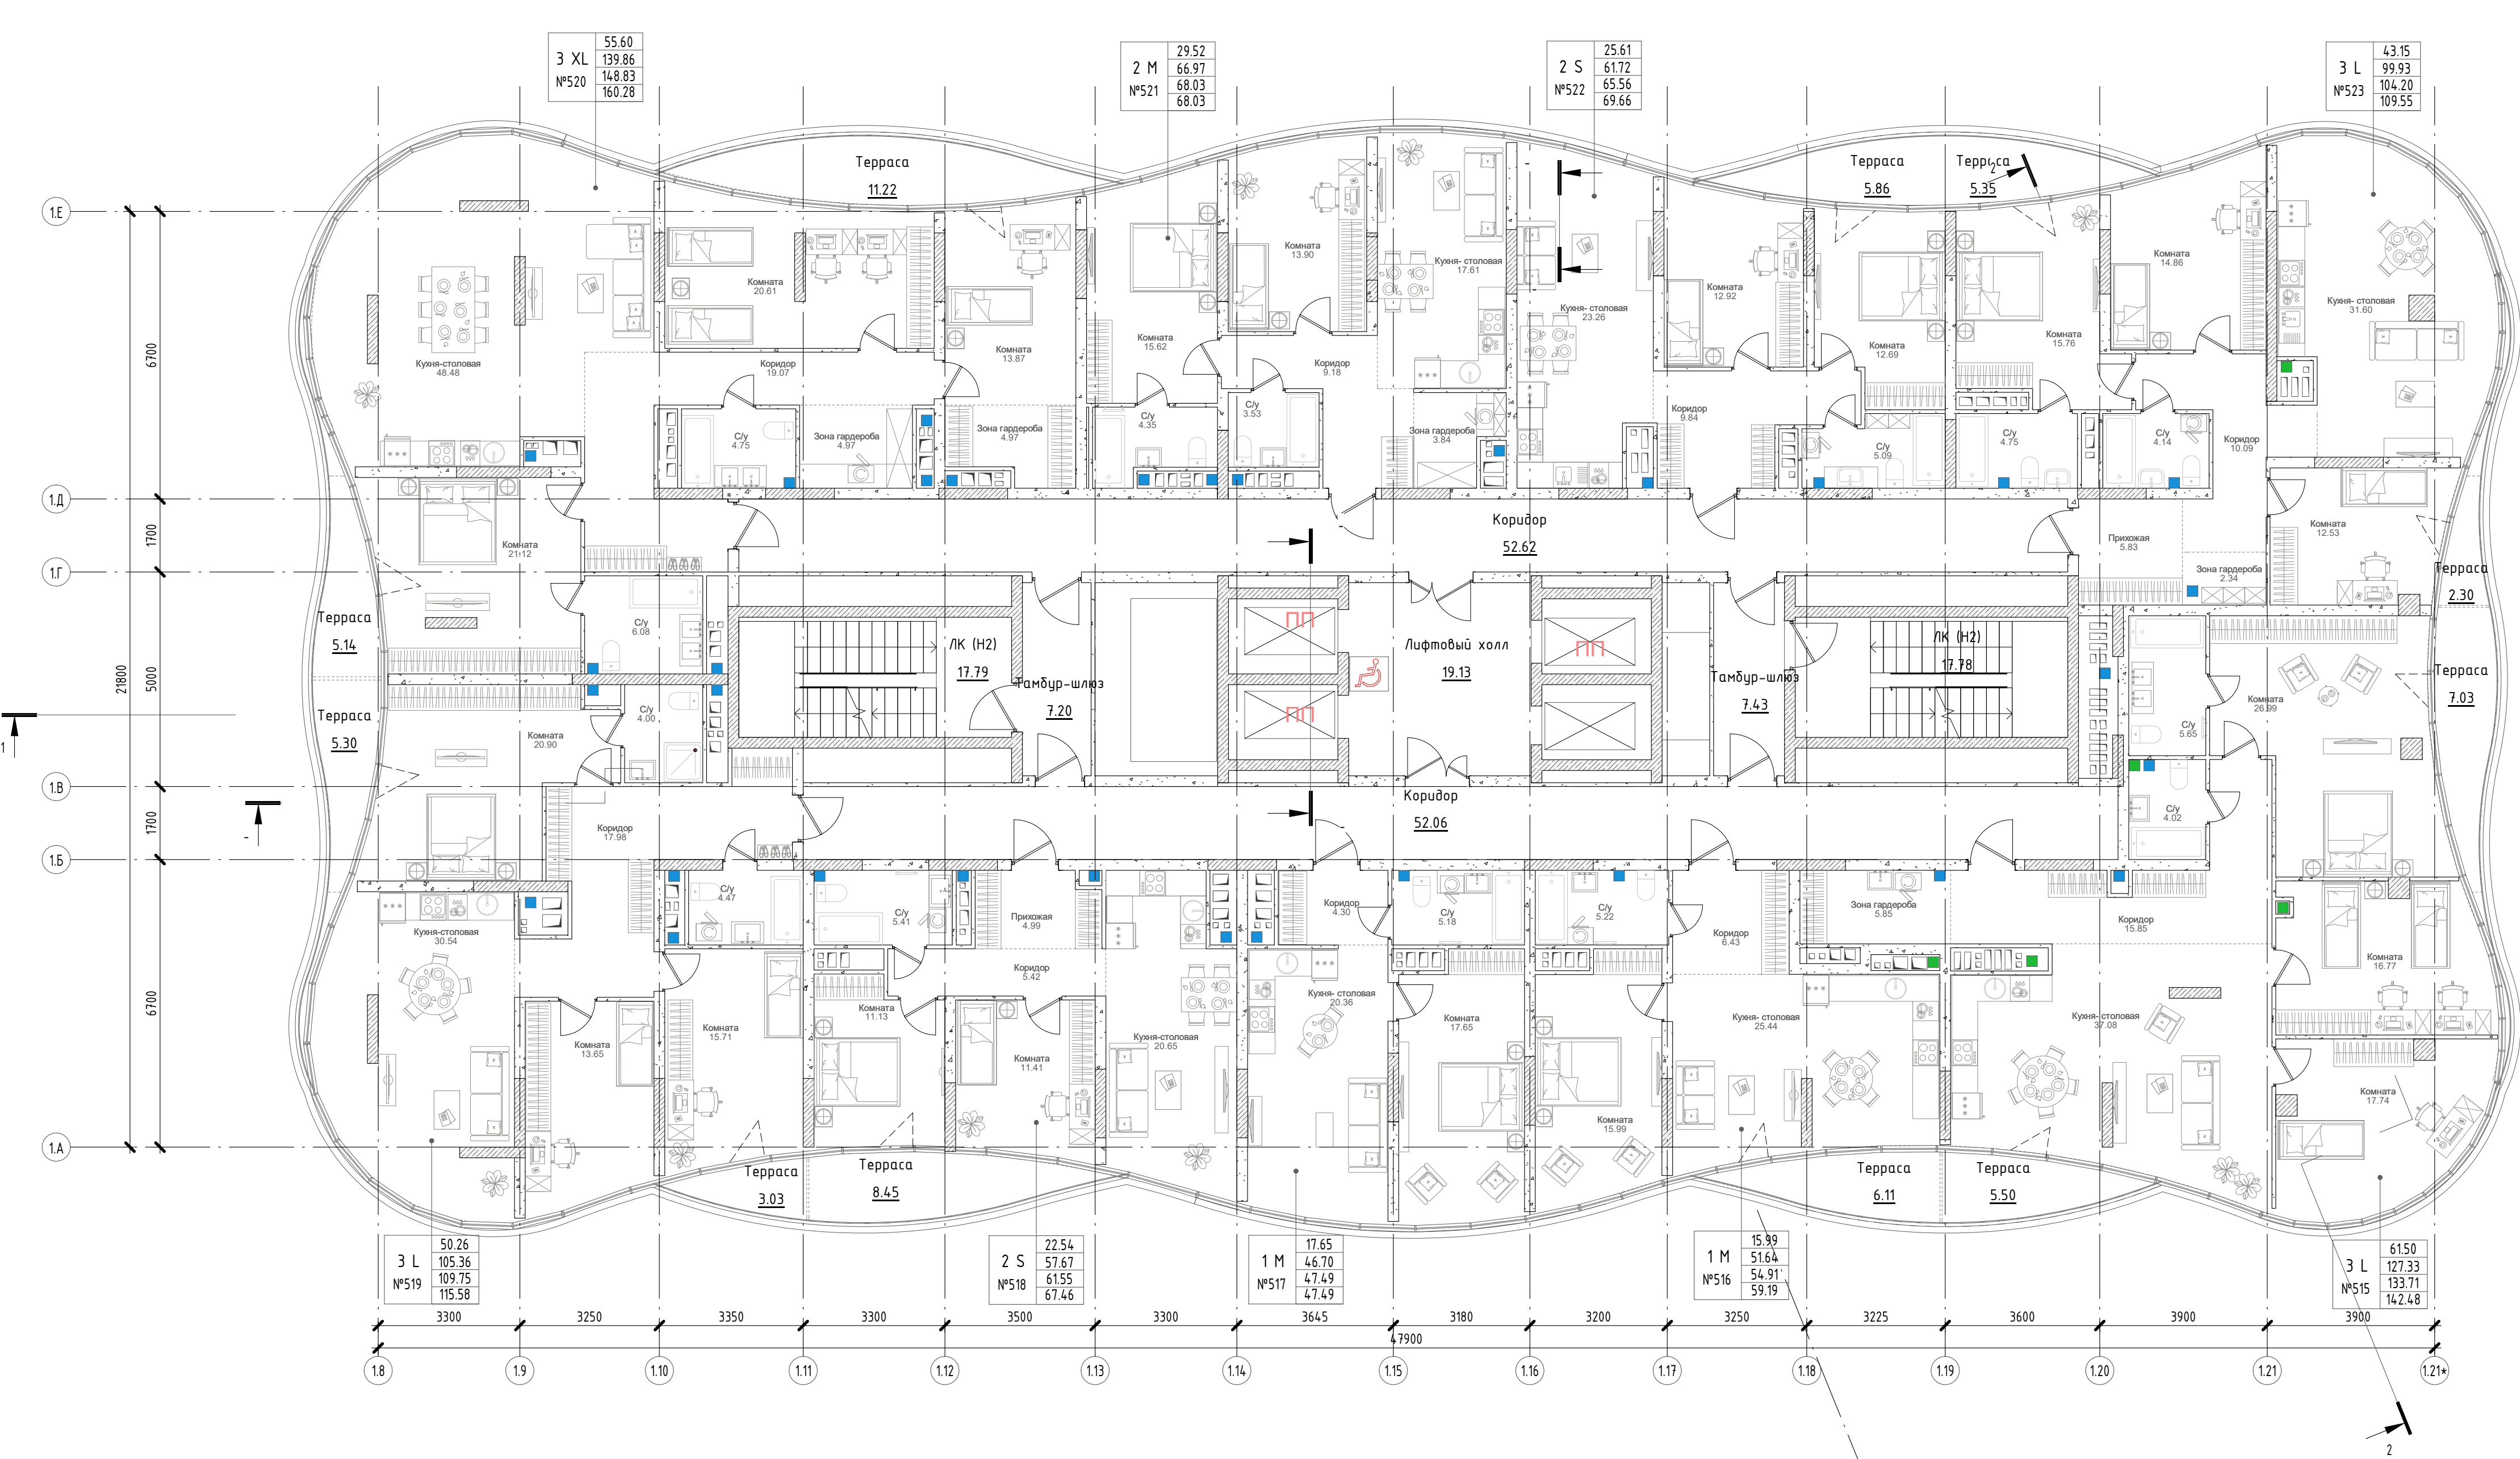

АР. К-1					
Архитектурные решения. Глава 2. Планировочные решения					
План 20 этажа					
Стадия			Лист		
ЭП			14		
Проектное бюро R1			Формат: А1		

