




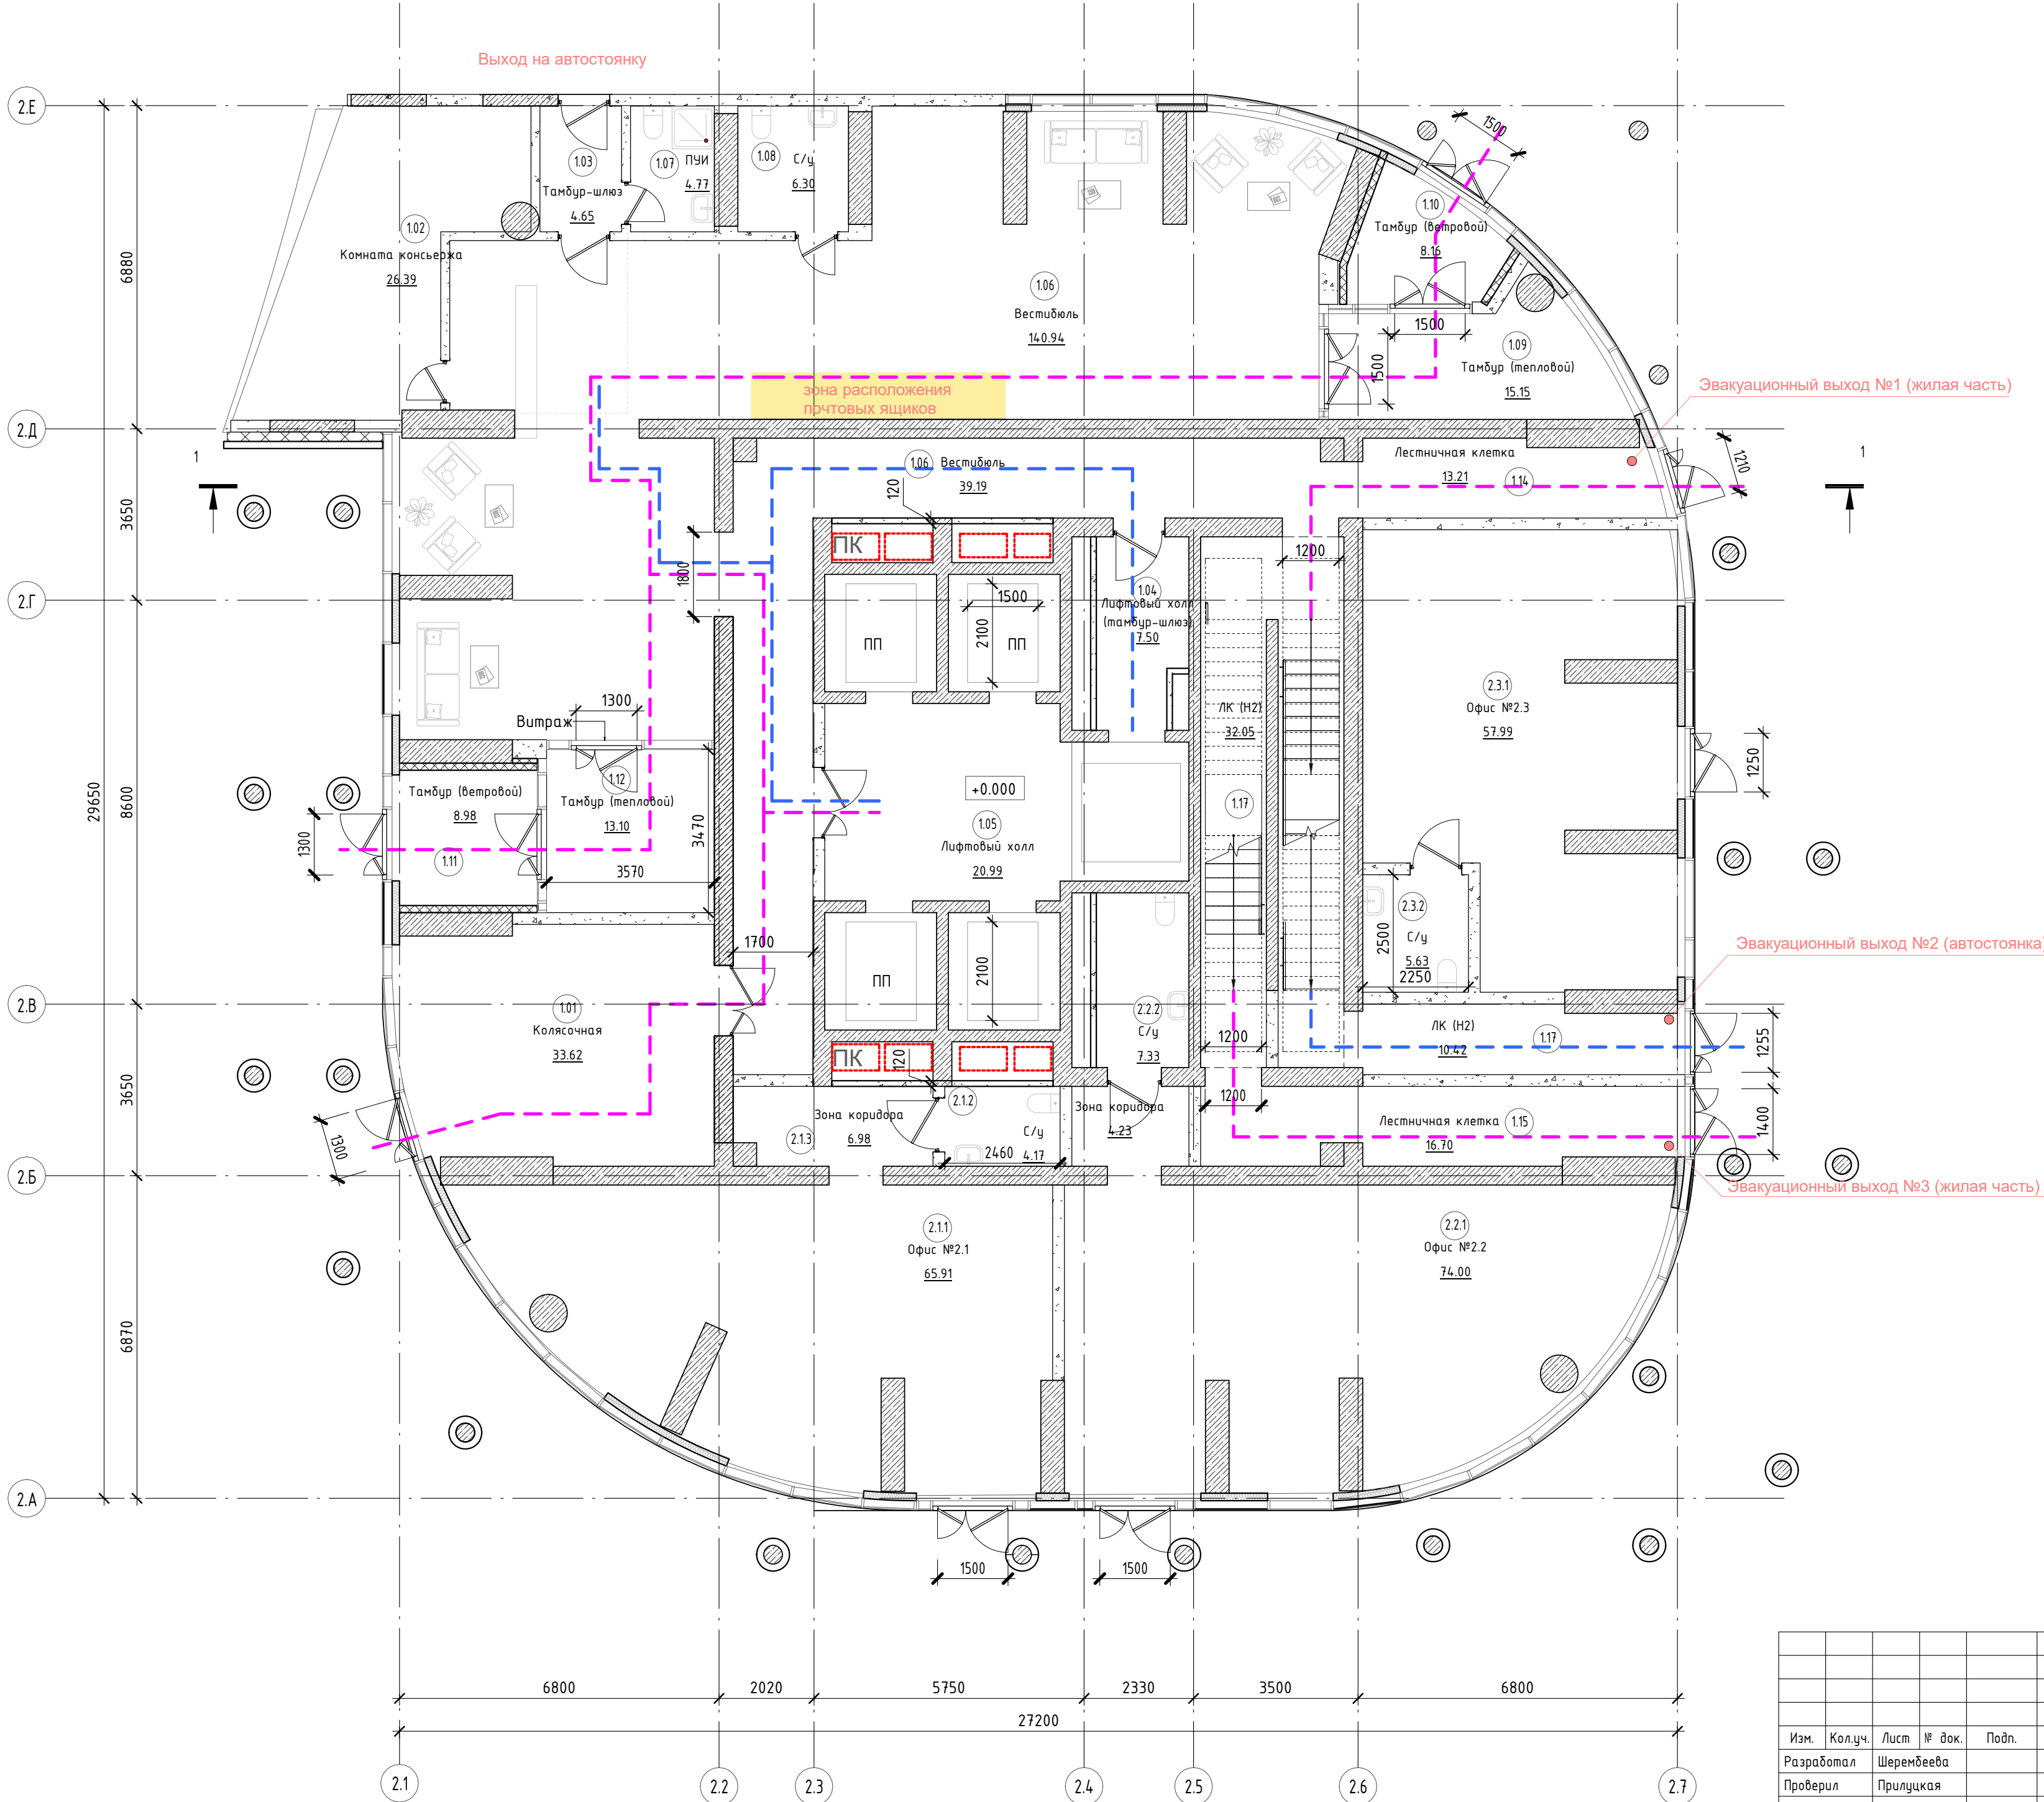

К-2. Экспликация помещений 1 этажа МОП			
№ пом.	Наименование	Площадь, м2	Кат. пом.
Коммерческое помещение 1			
2.3.1	Офис №2.3	57.99	
2.3.2	С/у	5.63	
		63.61	
Коммерческое помещение 2			
2.2.1	Офис №2.2	74.00	
2.2.2	С/у	7.33	
2.2.3	Зона коридора	4.23	
		85.56	
Коммерческое помещение 3			
2.1.1	Офис №2.1	65.91	
2.1.2	С/у	4.17	
2.1.3	Зона коридора	6.98	
		77.06	
МОП			
1.01	Колясочная	33.62	
1.02	Комната консьержа	26.39	
1.03	Тамбур-шлюз	4.65	
1.04	Лифтовый холл (тамбур-шлюз)	7.50	
1.05	Лифтовый холл	20.99	
1.06	Вестибюль	140.94	
1.07	ПУИ	4.77	
1.08	С/у	6.30	
1.09	Тамбур (тепловой)	15.15	
1.10	Тамбур (ветровой)	8.16	
1.11	Тамбур (ветровой)	8.98	
1.12	Тамбур (тепловой)	13.10	
1.14	Лестничная клетка	13.21	
1.15	Лестничная клетка	16.70	
1.17	ЛК (Н2)	42.47	
		402.12	

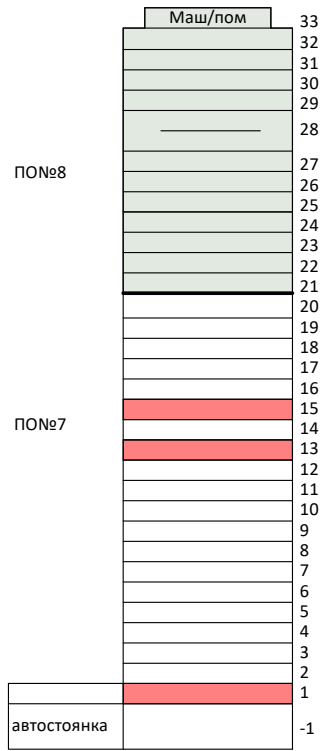


1506-2026-AP			
Корпус К-2			
Архитектурные решения	Стадия	Лист	Листов
	ПД	6	
План 1 этажа		ООО "ПБ Р1"	
ГИП	Кочнева	08.26	
Н.Контроль	Ситчихина	08.26	

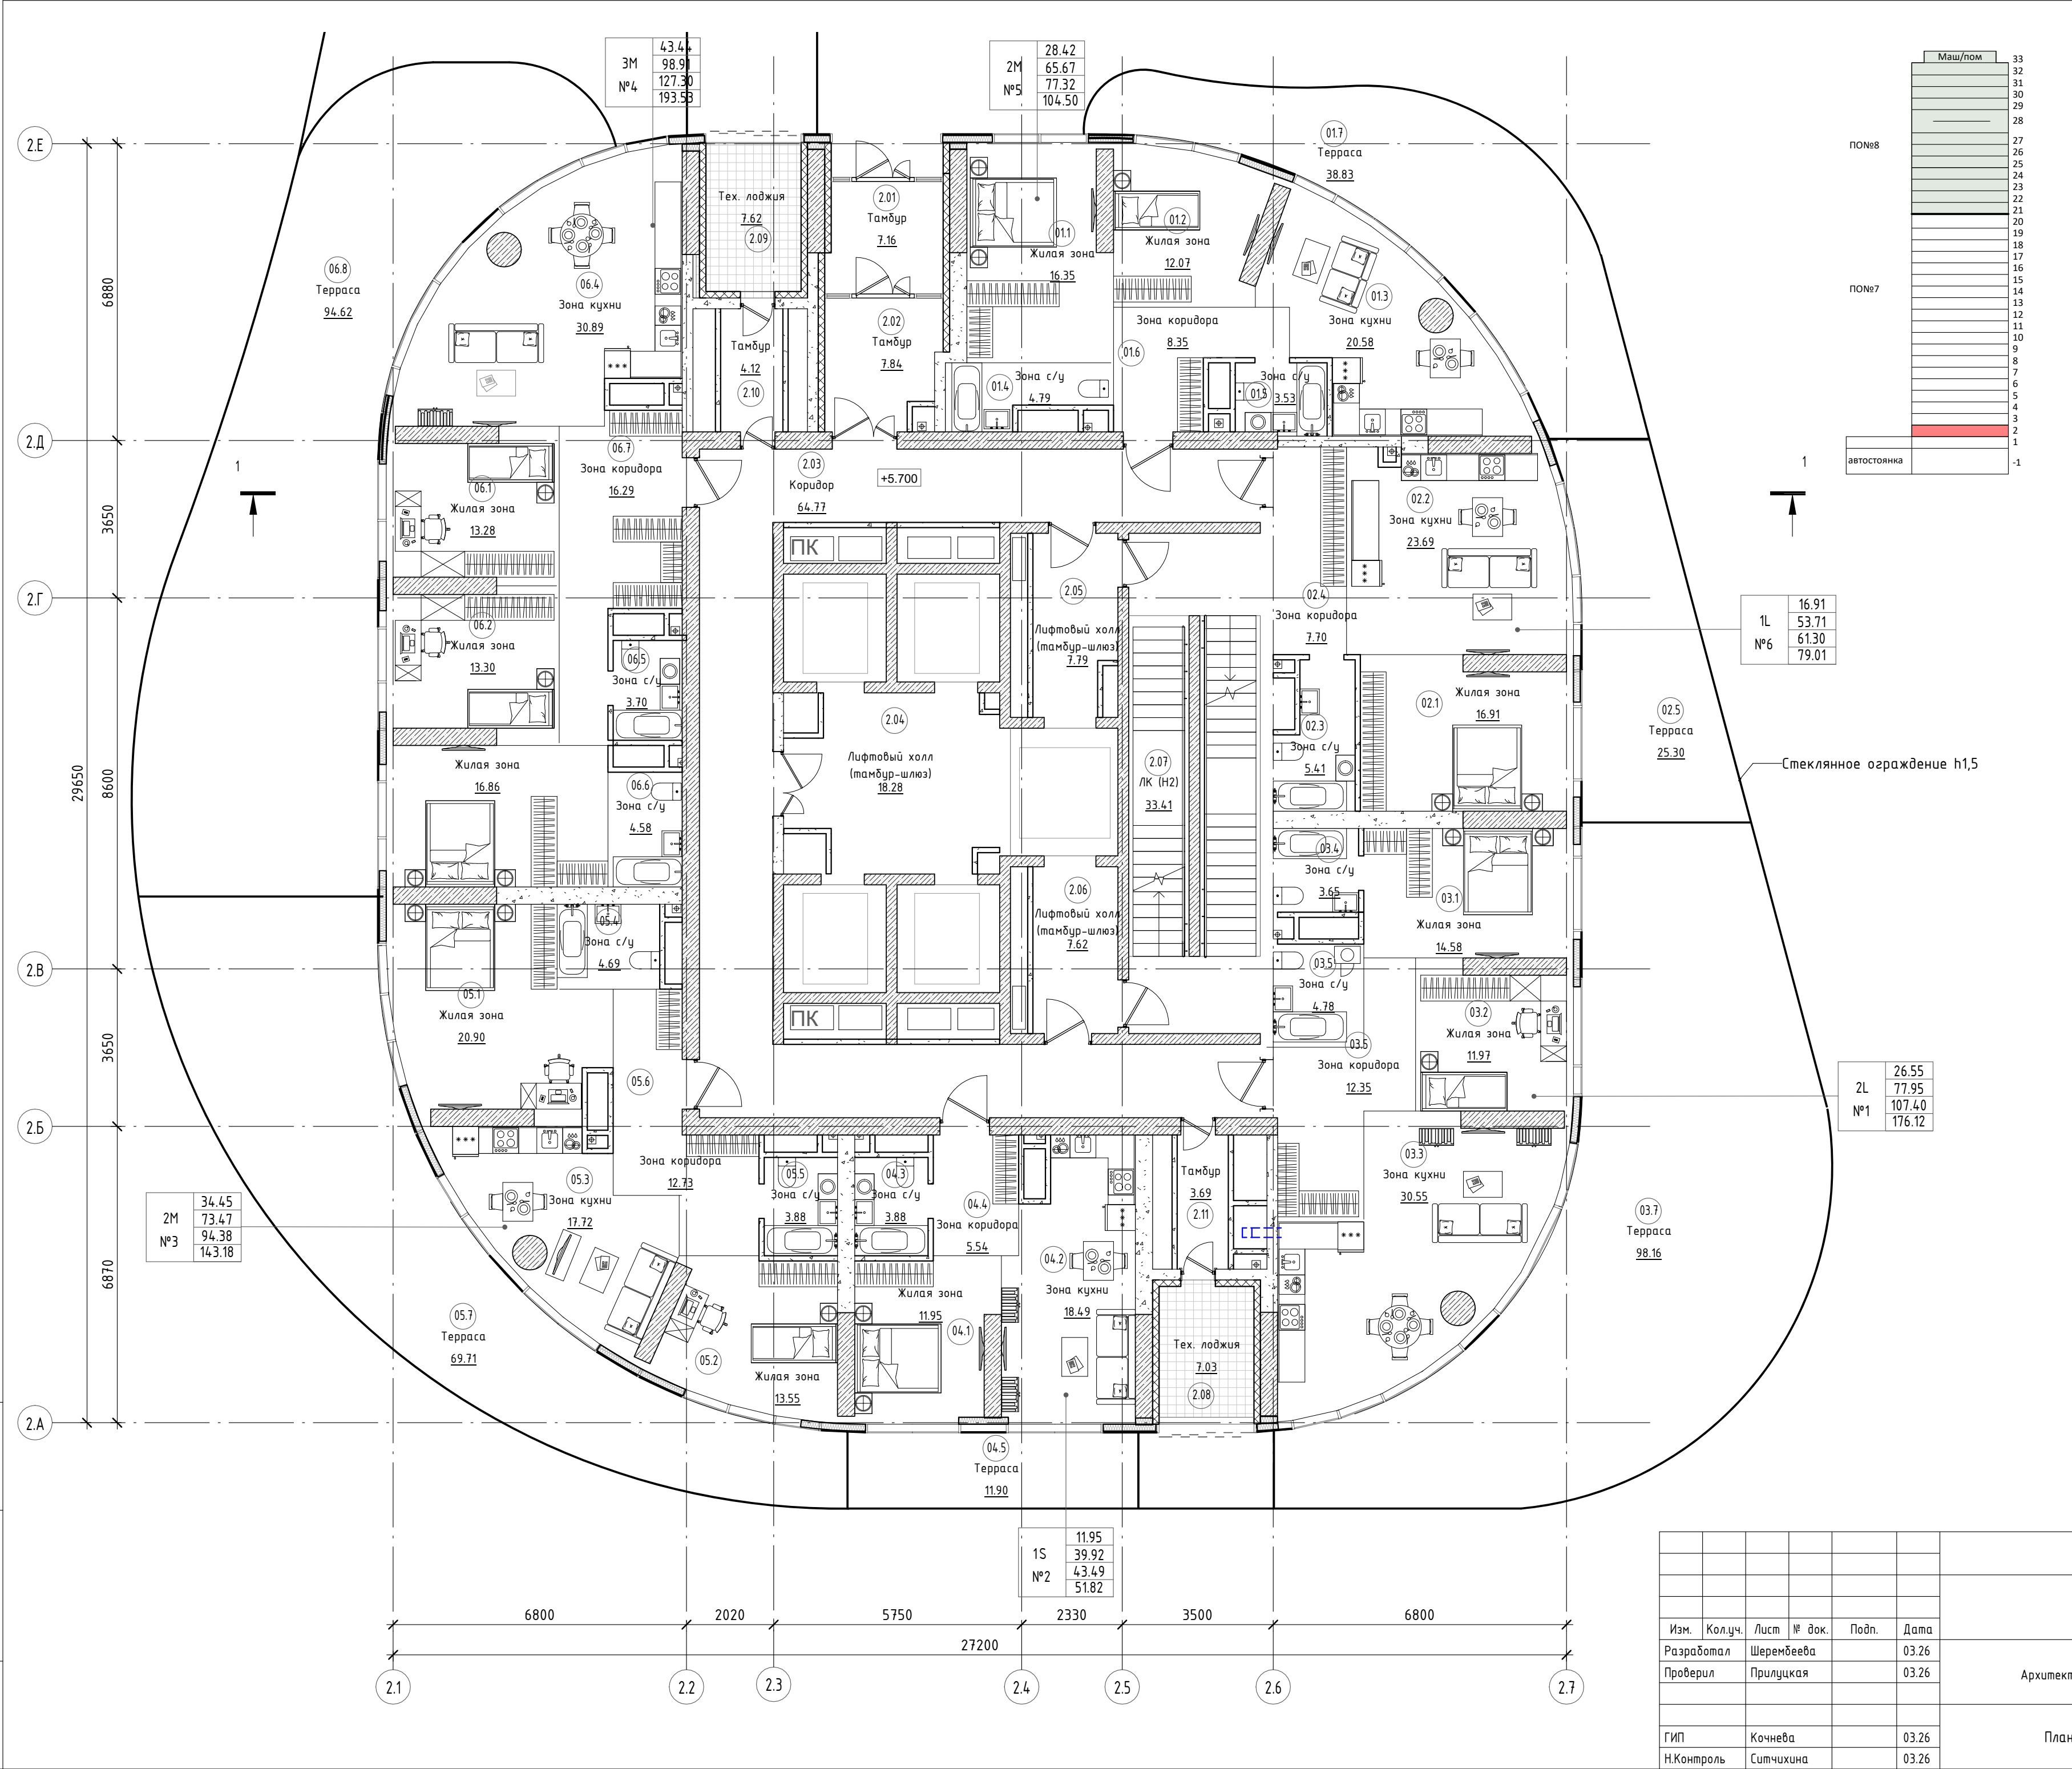


К-2. Экспликация помещений квартир 2 этажа				
№ пом.	Наименование	Площадь, м2	Кат. пом.	
1				
03.1	Жилая зона	14.58		
03.2	Жилая зона	11.97		
03.3	Зона кухни	30.55		
03.4	Зона с/у	3.65		
03.5	Зона с/у	4.78		
03.6	Зона коридора	12.35		
03.7	Терраса	98.16		
		176.04		
2				
04.1	Жилая зона	11.95		
04.2	Зона кухни	18.49		
04.3	Зона с/у	3.88		
04.4	Зона коридора	5.54		
04.5	Терраса	11.90		
		51.76		
3				
05.1	Жилая зона	20.90		
05.2	Жилая зона	13.55		
05.3	Зона кухни	17.72		
05.4	Зона с/у	4.69		
05.5	Зона с/у	3.88		
05.6	Зона коридора	12.73		
05.7	Терраса	69.71		
		143.17		
4				
06.1	Жилая зона	13.28		
06.2	Жилая зона	13.30		
06.3	Жилая зона	16.86		
06.4	Зона кухни	30.89		
06.5	Зона с/у	3.70		
06.6	Зона с/у	4.58		
06.7	Зона коридора	16.29		
06.8	Терраса	94.62		
		193.52		
5				
01.1	Жилая зона	16.35		
01.2	Жилая зона	12.07		
01.3	Зона кухни	20.58		
01.4	Зона с/у	4.79		
01.5	Зона с/у	3.53		
01.6	Зона коридора	8.35		
01.7	Терраса	38.83		
		104.51		
6				
02.1	Жилая зона	16.91		
02.2	Зона кухни	23.69		
02.3	Зона с/у	5.41		
02.4	Зона коридора	7.70		
02.5	Терраса	25.30		
		79.02		
МОП				
2.01	Тамбур	7.16		
2.02	Тамбур	7.84		
2.03	Коридор	64.77		
2.04	Лифтовый холл (тамбур-шлюз)	18.28		
2.05	Лифтовый холл (тамбур-шлюз)	7.79		
2.06	Лифтовый холл (тамбур-шлюз)	7.62		
2.07	ЛК (H2)	33.41		
2.08	Тех. лоджия	7.03		
		153.89		
1506-2026-AP				
Корпус К-2				
Архитектурные решения		Стадия	Лист	Листов
		ПД	7	
2 этажа		ООО "ПБ Р1"		


Изм.	Кол.уч.	Лист	№ док.	Подп.	Дата
Разработал	Шерембеева				03.26
Проверил	Прилуцкая				03.26
ГИП	Кочнева				03.26
Н.Контроль	Ситчихина				03.26

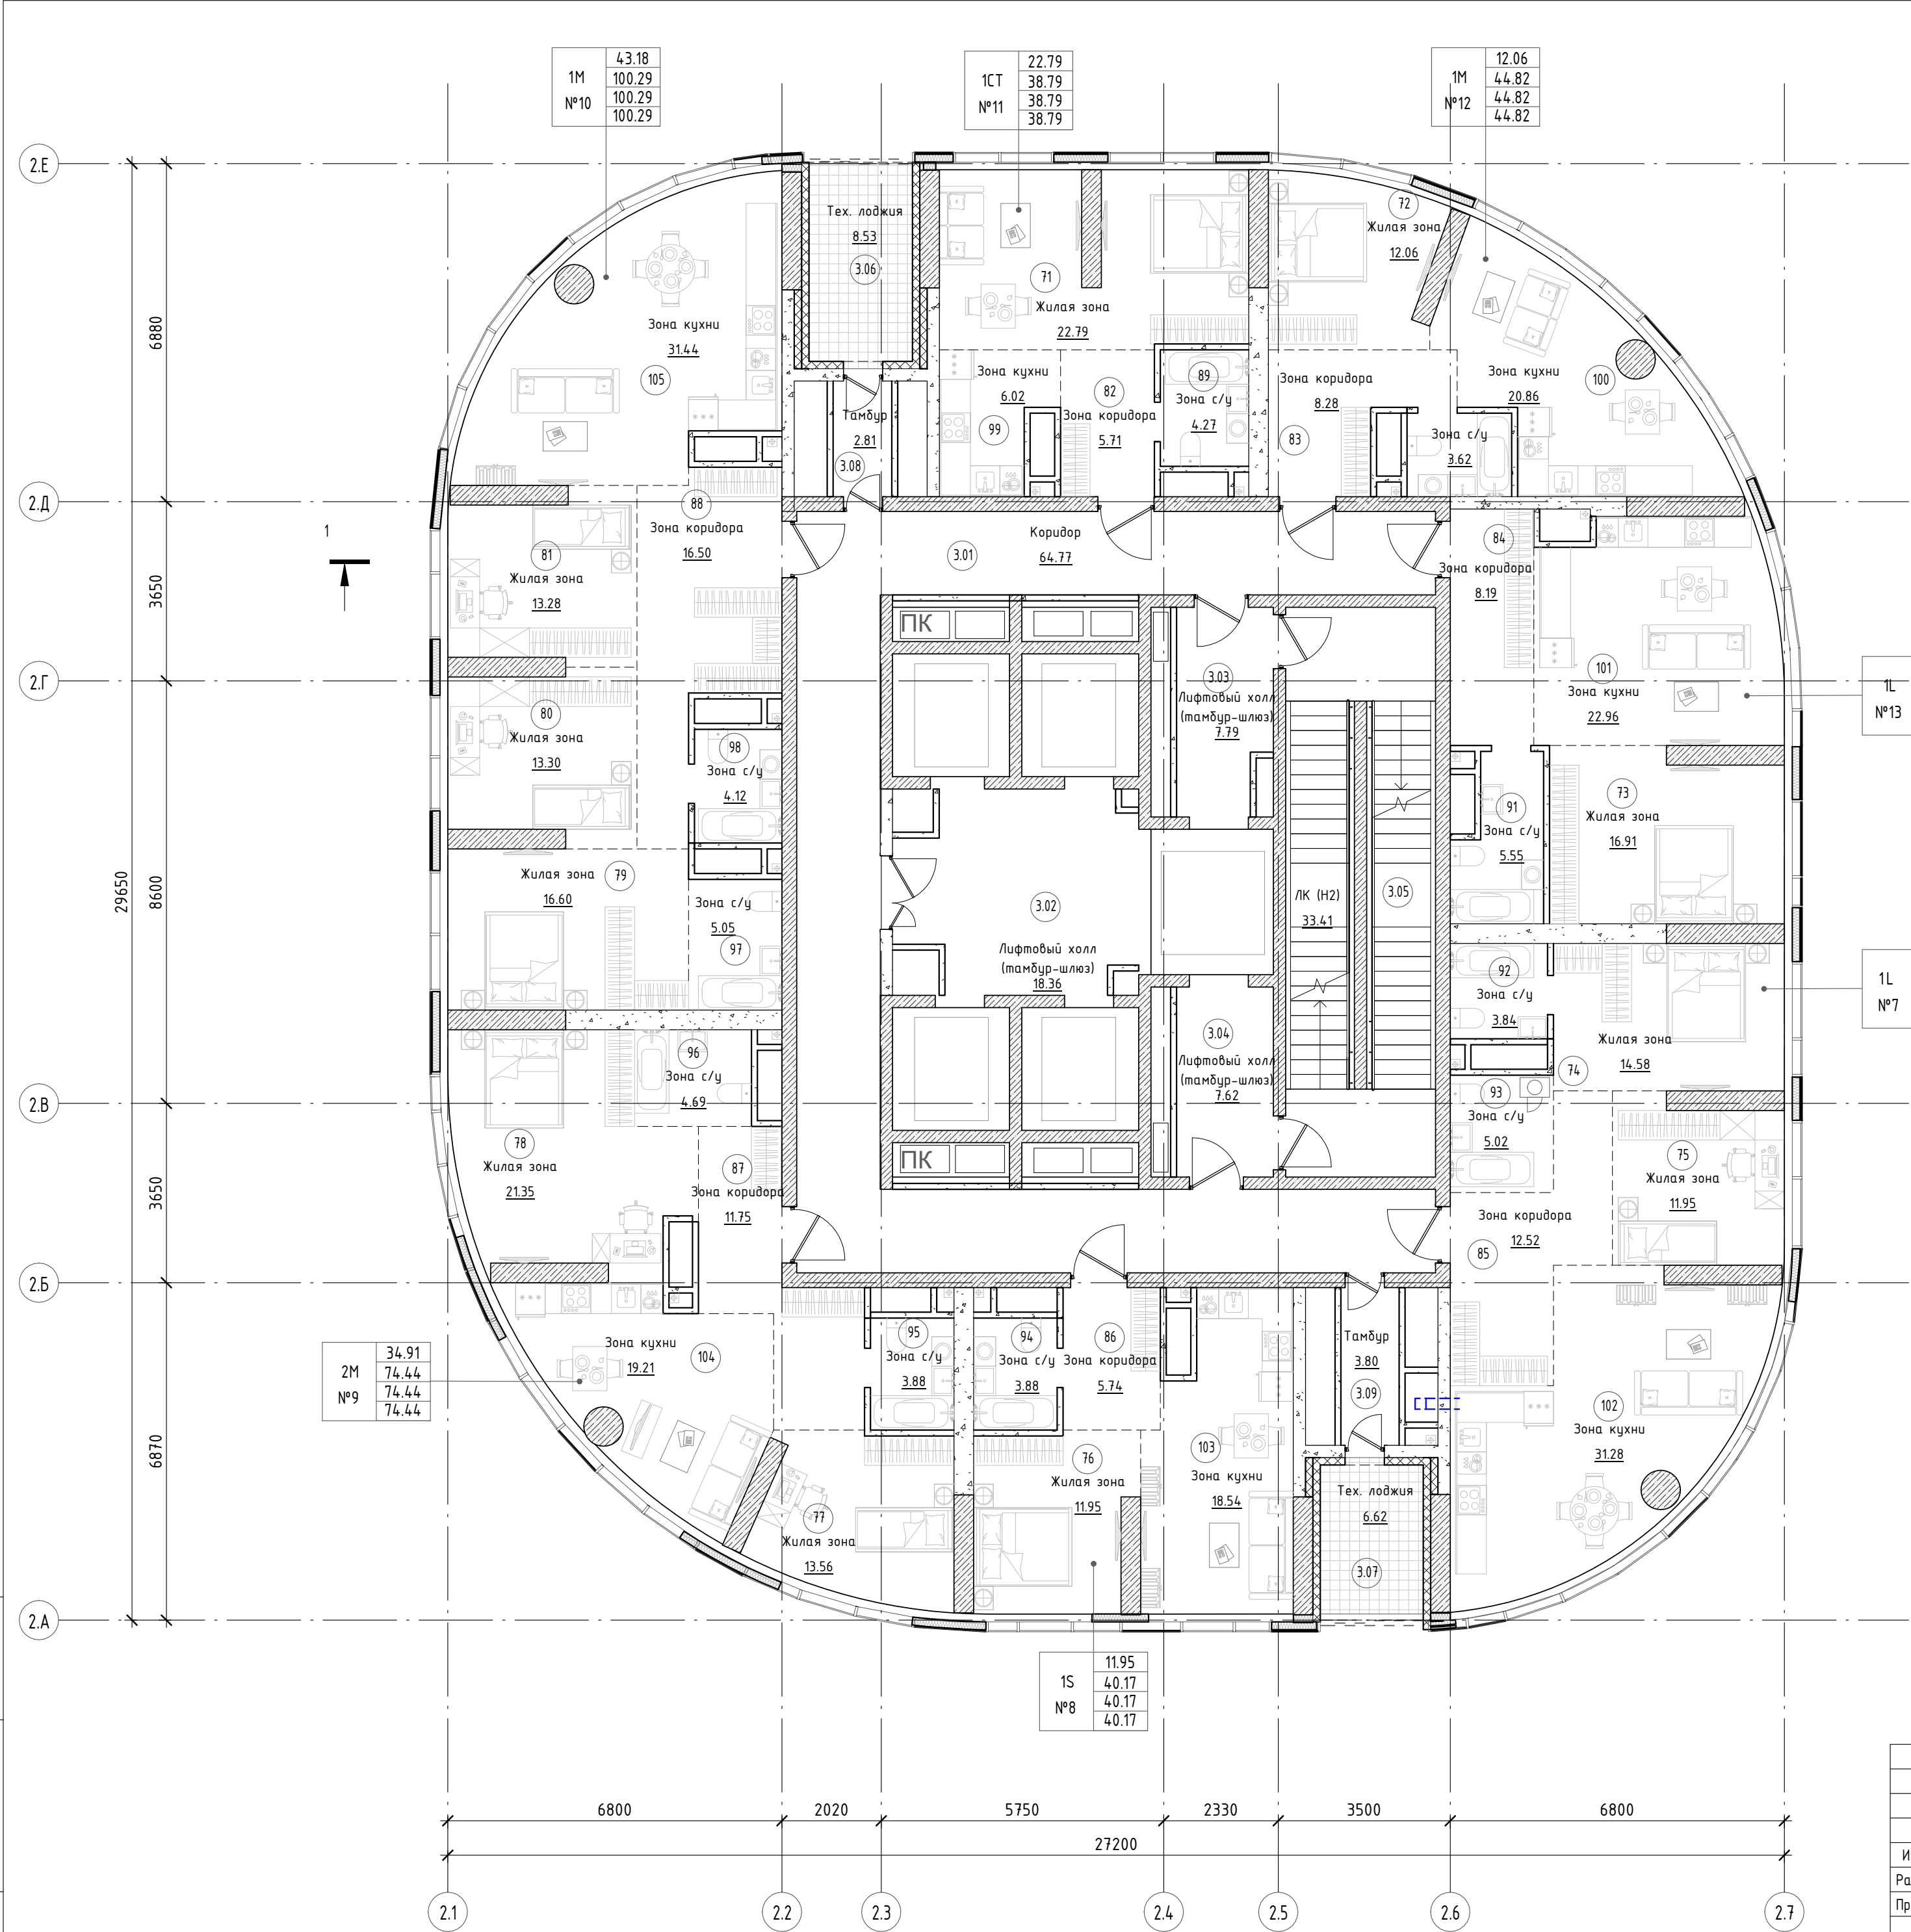


МОП			
3.01	Коридор	64.77	
3.02	Лифтовый холл (тамбур-шлюз)	18.36	
3.03	Лифтовый холл (тамбур-шлюз)	7.79	
3.04	Лифтовый холл (тамбур-шлюз)	7.62	
3.05	ЛК (H2)	33.41	
3.06	Тех. лоджия	8.53	
3.07	Тех. лоджия	6.62	
3.08	Тамбур	2.81	
3.09	Тамбур	3.80	
		153.72	

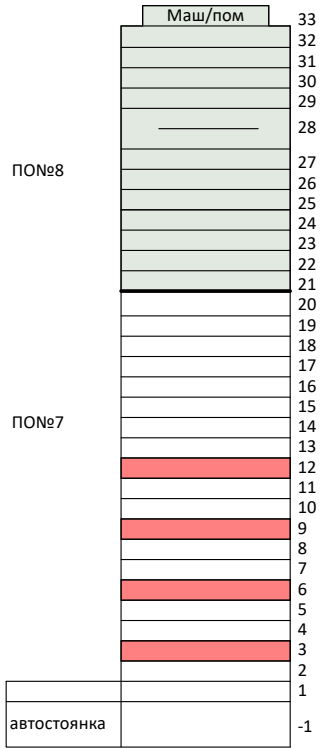


						1506-2026-AP			
						Корпус К-2			
Изм.	Кол.уч.	Лист	№ док.	Подп.	Дата	Архитектурные решения	Стадия	Лист	Листов
Разработал	Шерембеева				03.26		ПД	8	
Проверил	Прилуцкая				03.26				
						План этажей 3, 6, 9, 12	000 "ПБ Р1"		
ГИП	Кочнева				03.26				
Н.Контроль	Ситчихина				03.26				

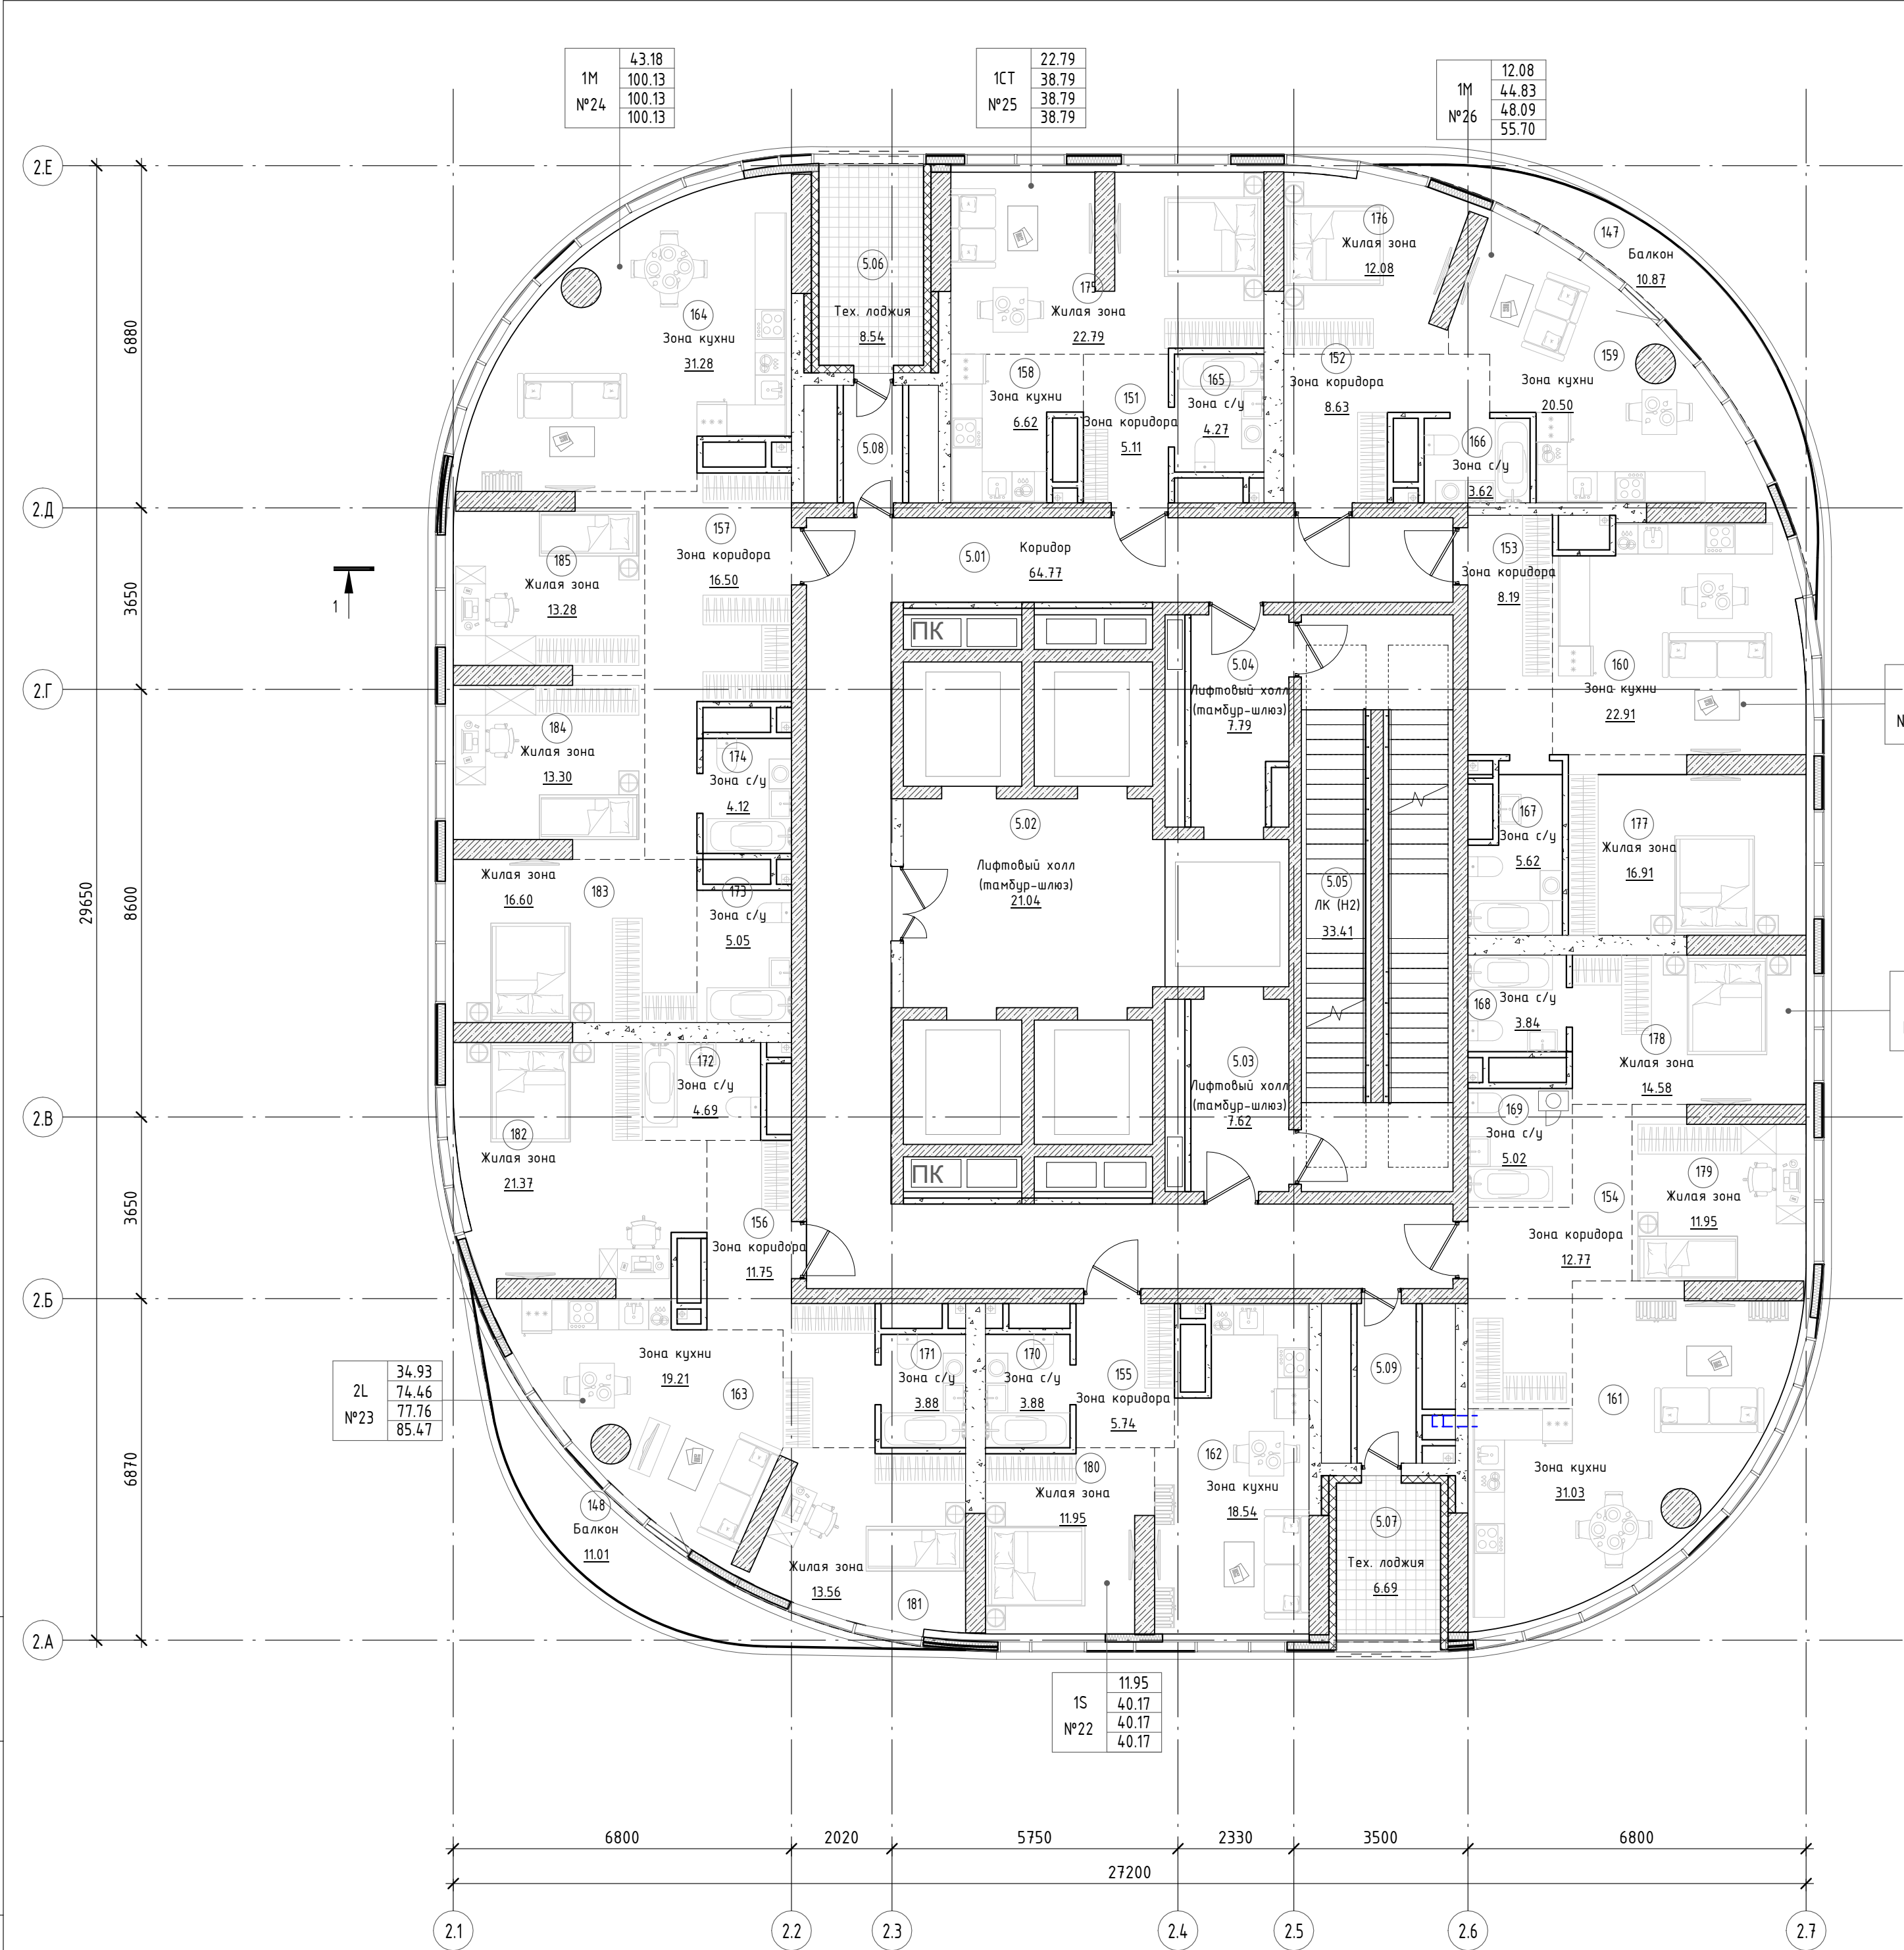


МОП			
5.01	Коридор	64.77	
5.02	Лифтовый холл (тамбур-шлюз)	21.04	
5.03	Лифтовый холл (тамбур-шлюз)	7.62	
5.04	Лифтовый холл (тамбур-шлюз)	7.79	
5.05	ЛК (H2)	33.41	
5.06	Тех. лоджия	8.54	
5.07	Тех. лоджия	6.69	
5.08	Тамбур	2.83	
5.09	Тамбур	3.82	
		156.52	

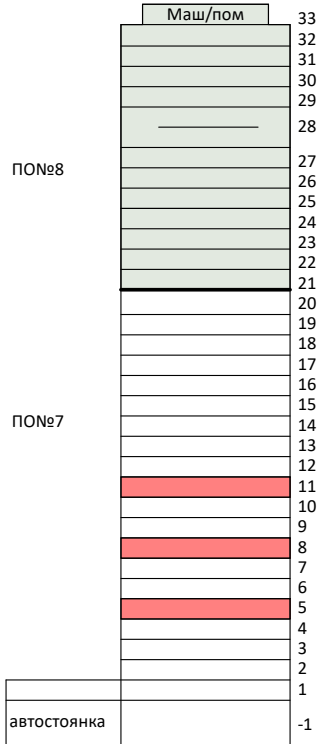


1506-2026-AP					
Корпус К-2					
Изм.	Кол.уч.	Лист	№ док.	Подп.	Дата
Архитектурные решения				Стадия	Лист
				ПД	10
План этажей 5, 8, 11				ООО "ПБ Р1"	
Кочнева Ситчихина				Формат: А2	

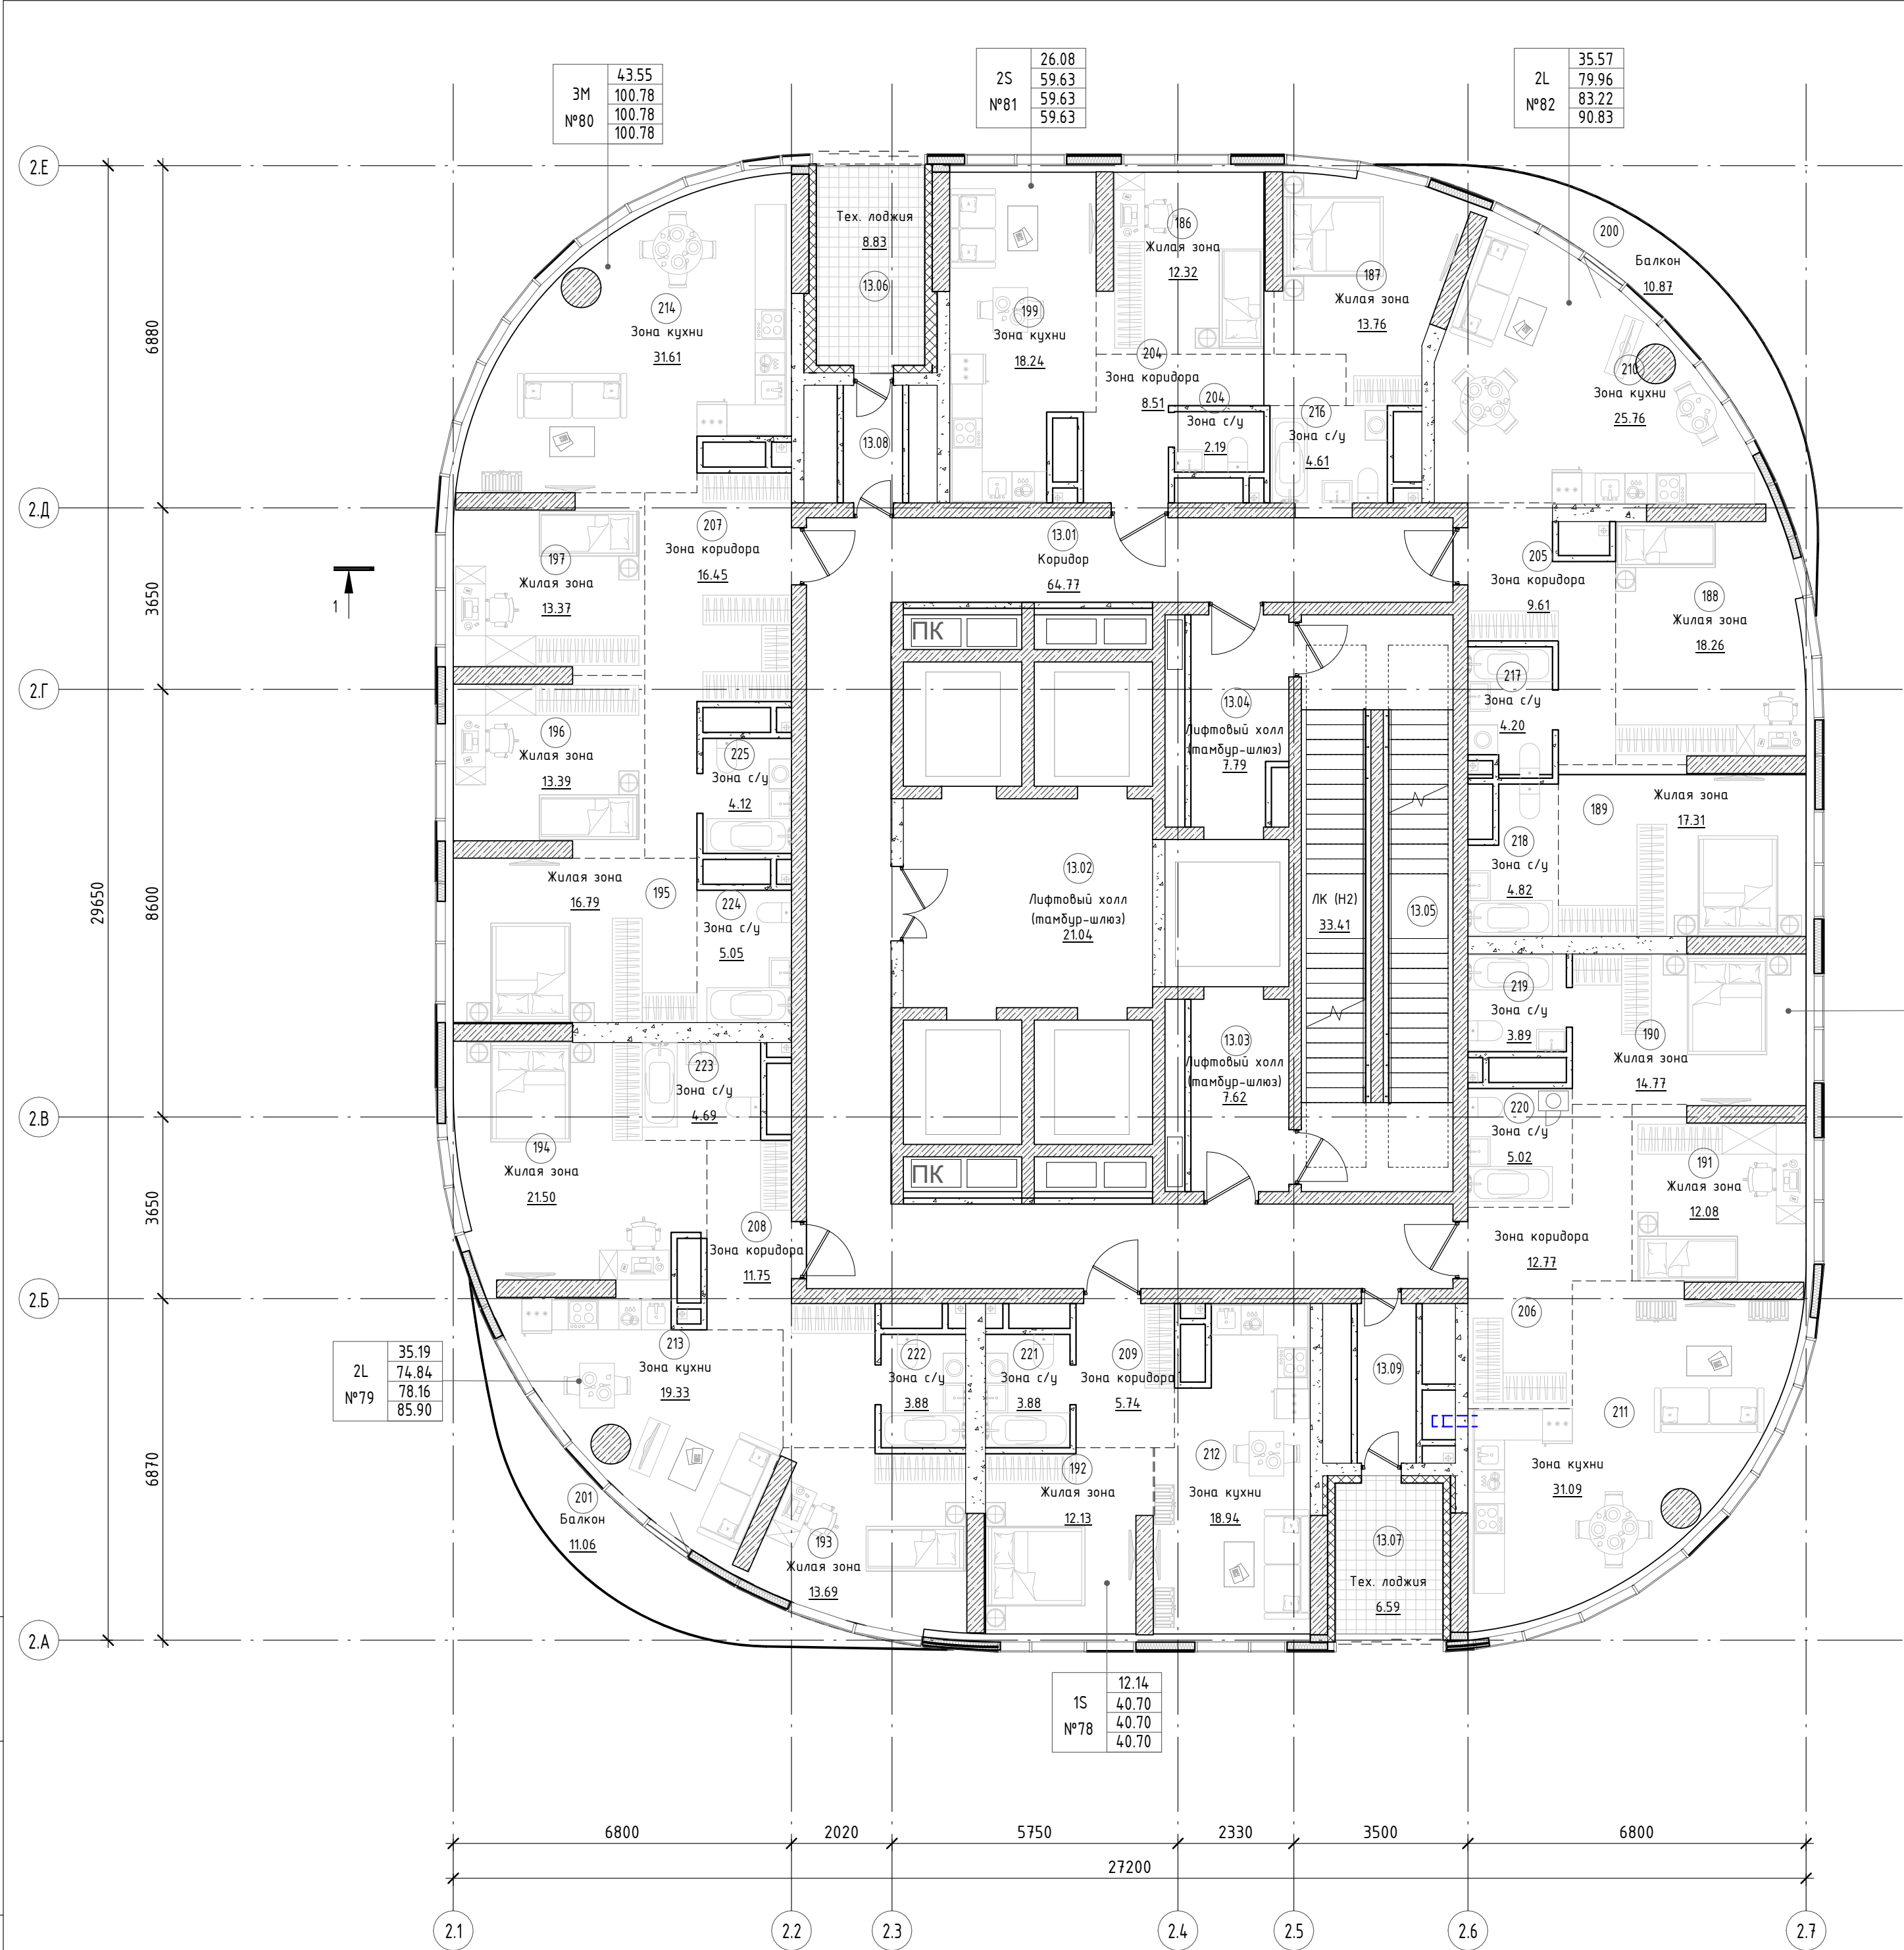


МОП			
13.01	Коридор	64.77	
13.02	Лифтовый холл (тамбур-шлюз)	21.04	
13.03	Лифтовый холл (тамбур-шлюз)	7.62	
13.04	Лифтовый холл (тамбур-шлюз)	7.79	
13.05	ЛК (H2)	33.41	
13.06	Тех. лоджия	8.83	
13.07	Тех. лоджия	6.59	
13.08	Тамбур	2.83	
13.09	Тамбур	3.80	
		156.67	

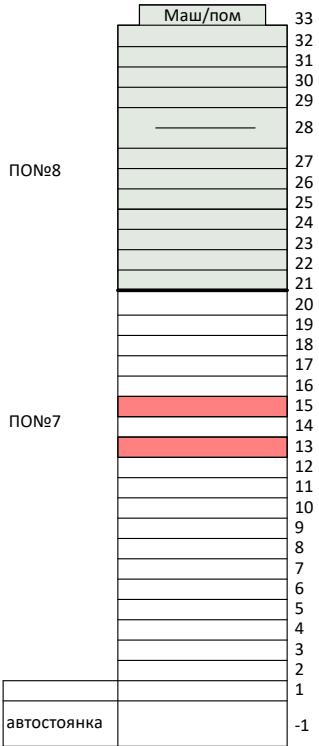


						1506-2026-AP				
						Корпус К-2				
Изм.	Кол.уч.	Лист	№ док.	Подп.	Дата	Архитектурные решения	Стадия	Лист	Листов	
							ПД	11		
							План этажей 13, 15	000 "ПБ Р1"		

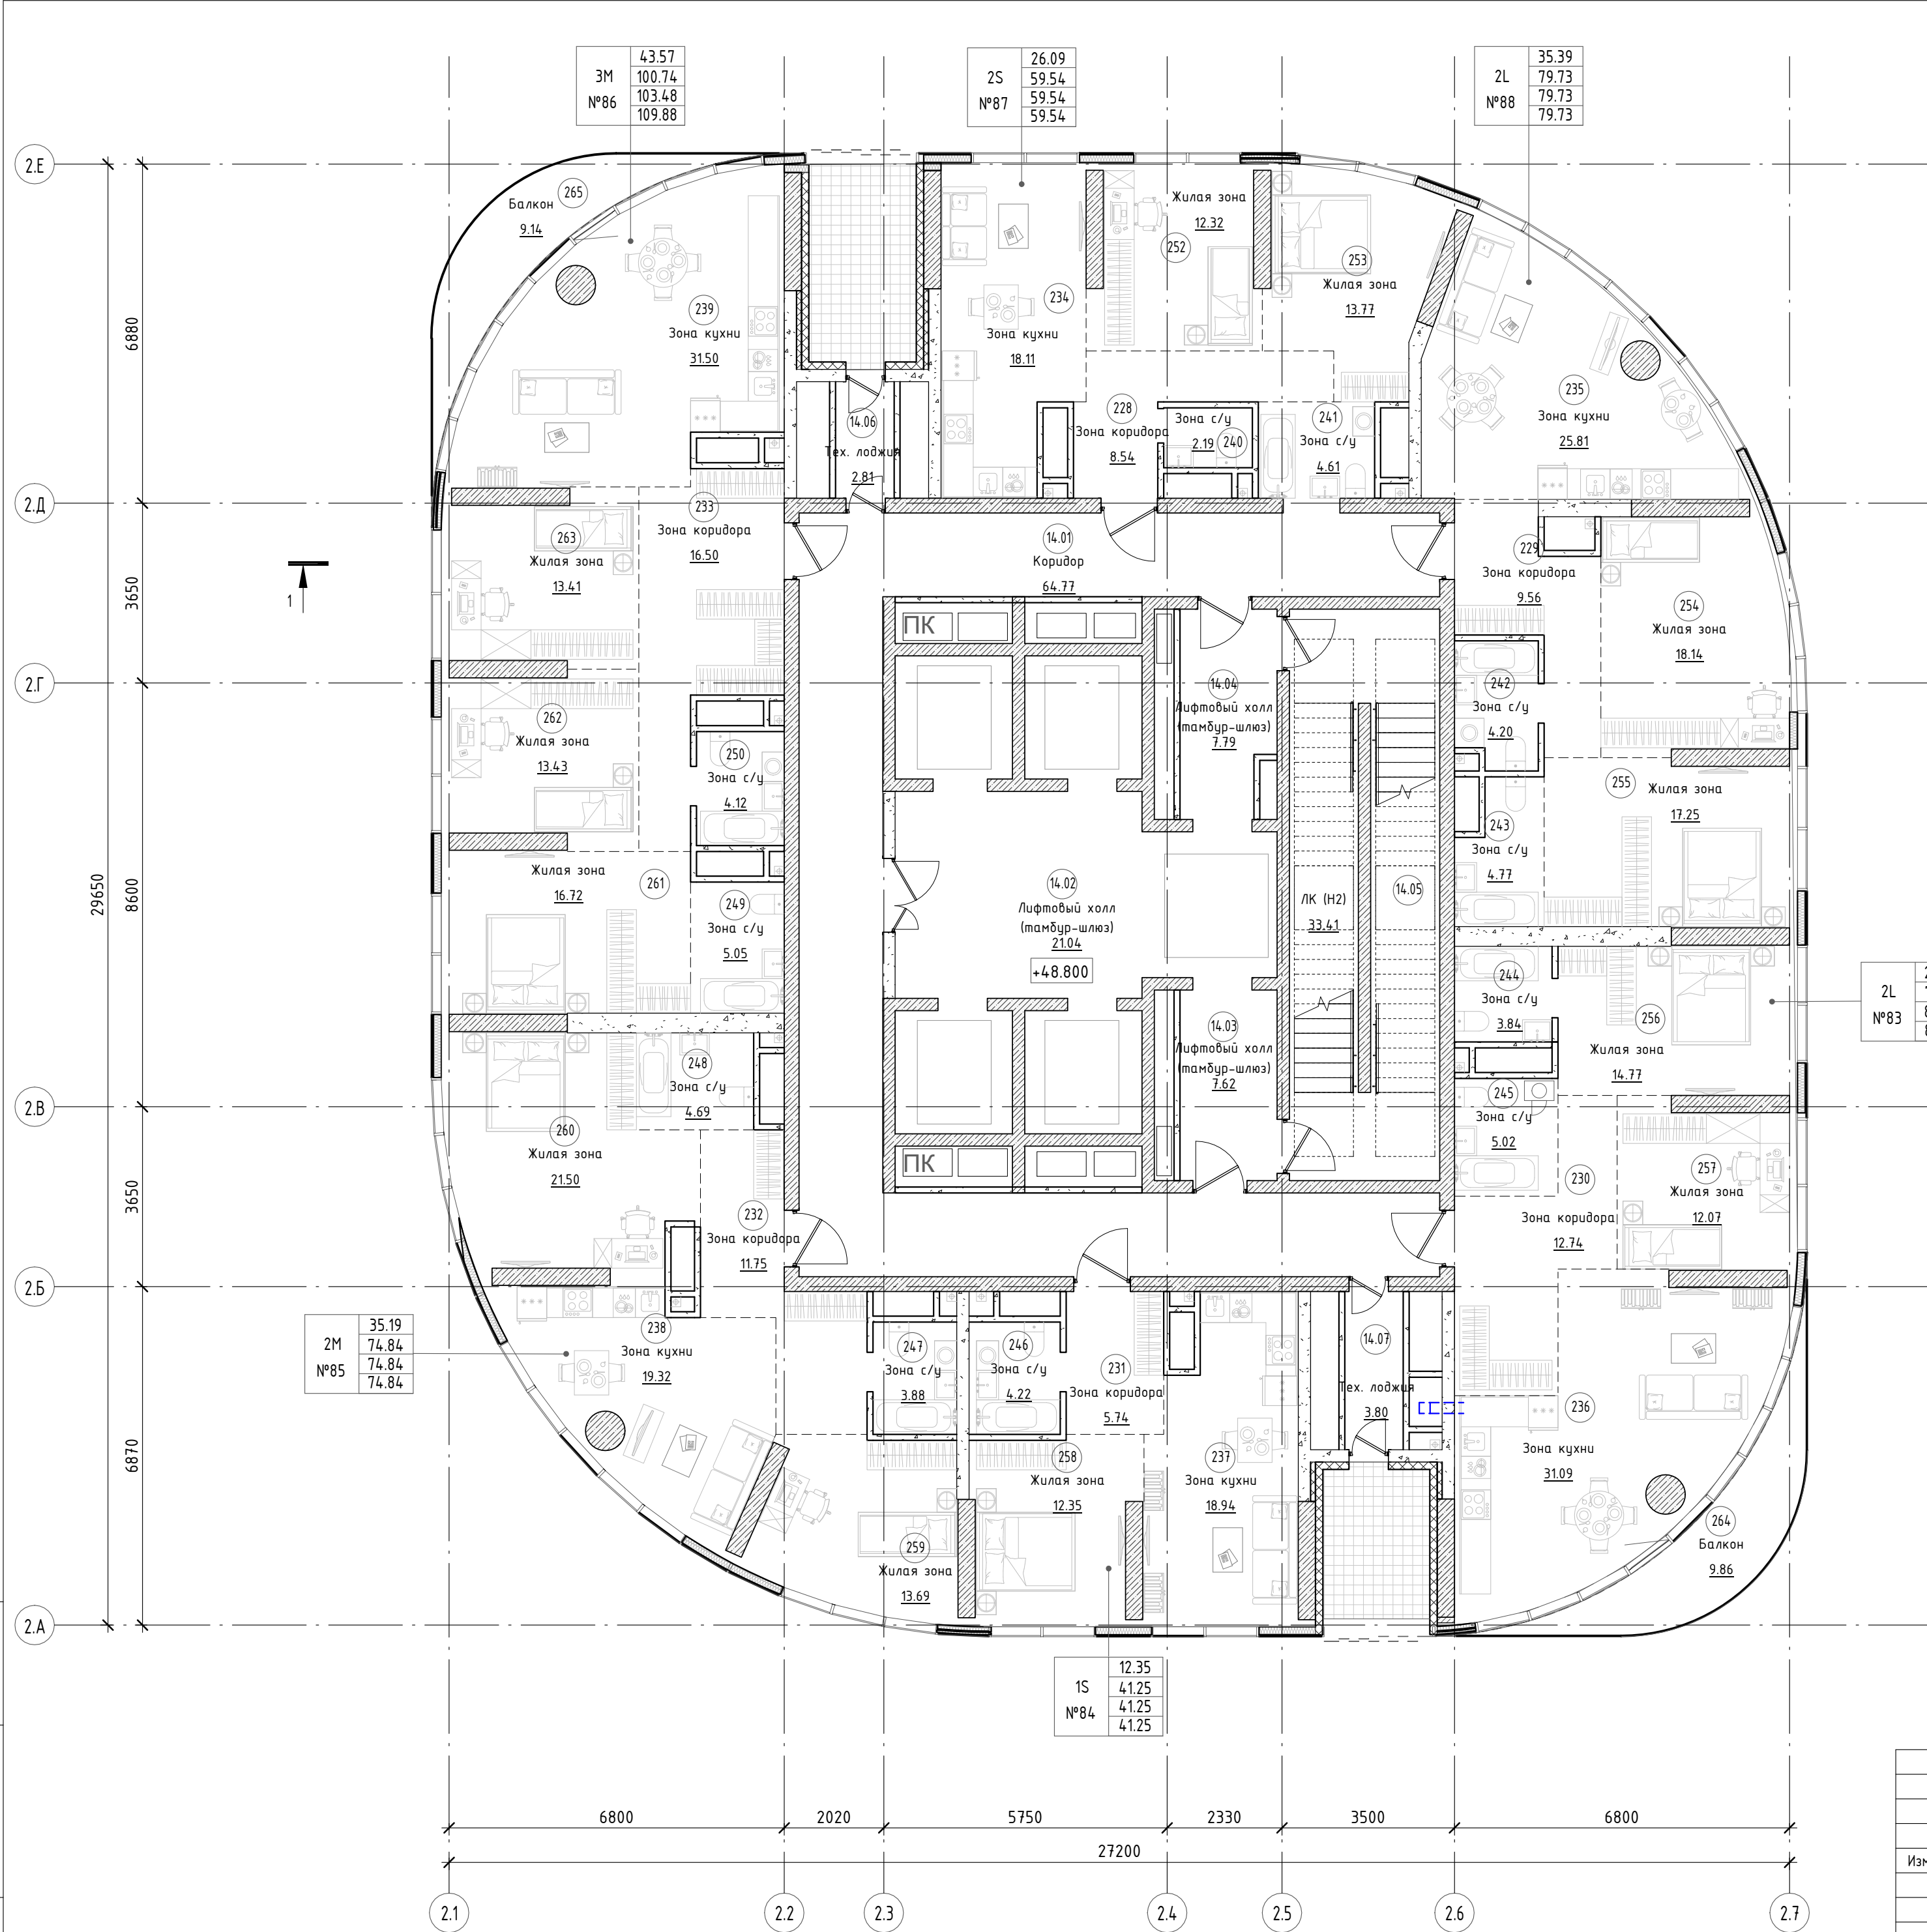


МОП			
14.01	Коридор	64.77	
14.02	Лифтовый холл (тамбур-шлюз)	21.04	
14.03	Лифтовый холл (тамбур-шлюз)	7.62	
14.04	Лифтовый холл (тамбур-шлюз)	7.79	
14.05	ЛК (H2)	33.41	
14.06	Тех. лоджия	2.81	
14.07	Тех. лоджия	3.80	
		141.25	

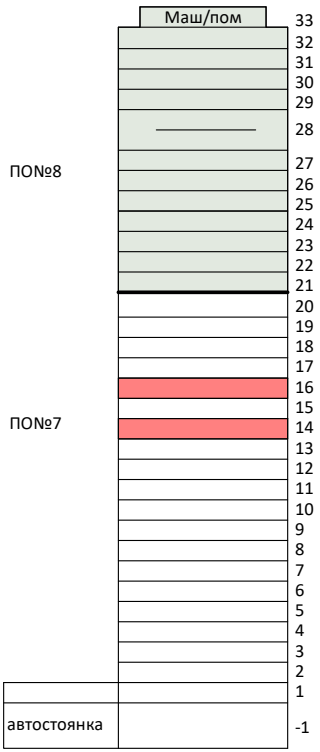


						1506-2026-AP				
						Корпус К-2				
Изм.	Кол.уч.	Лист	№ док.	Подп.	Дата	Архитектурные решения	Стадия	Лист	Листов	
							ПД	12		
							План этажей 14, 16	000 "ПБ Р1"		
		</								

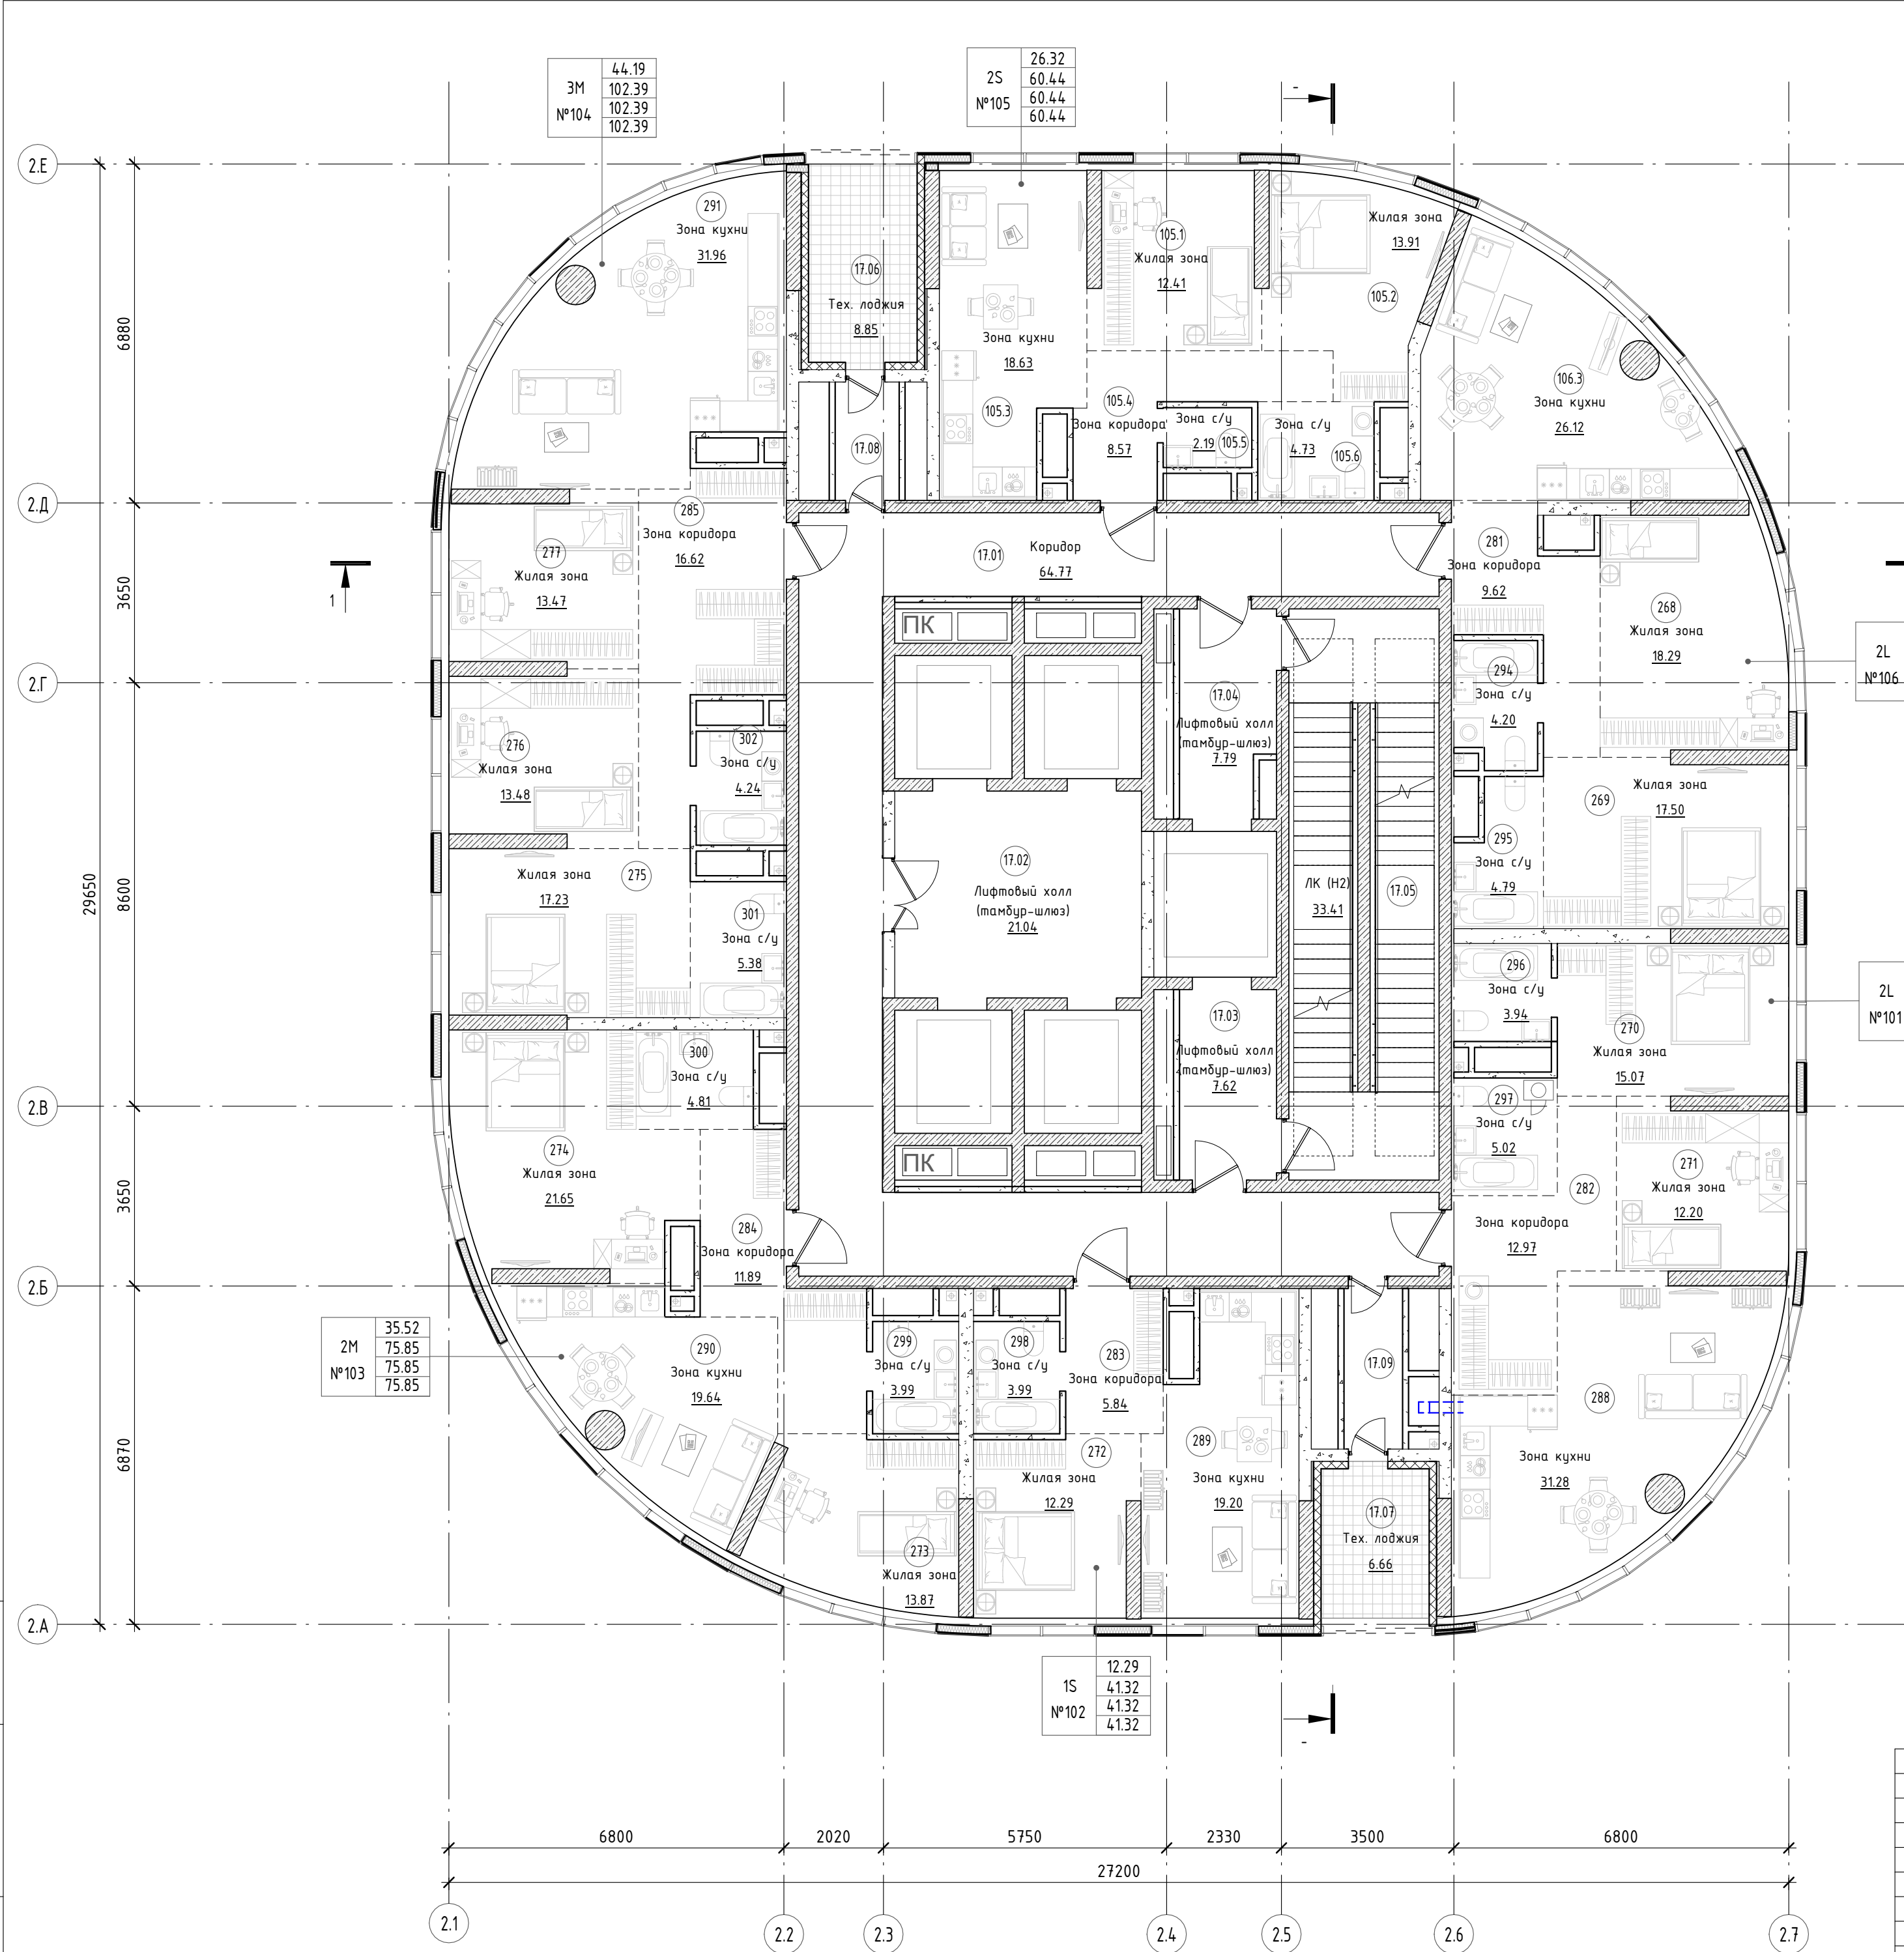

МОП			
17.01	Коридор	64.77	
17.02	Лифтовый холл (тамбур-шлюз)	21.04	
17.03	Лифтовый холл (тамбур-шлюз)	7.62	
17.04	Лифтовый холл (тамбур-шлюз)	7.79	
17.05	ЛК (H2)	33.41	
17.06	Тех. лоджия	8.85	
17.07	Тех. лоджия	6.66	
17.08	Тамбур	3.13	
17.09	Тамбур	3.88	
		157.15	

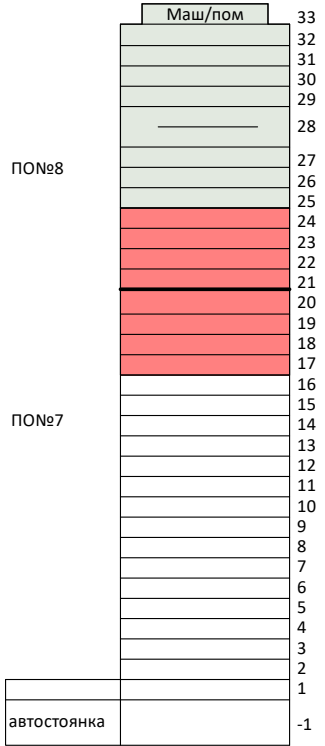

1506-2026-AP					
Корпус К-2					
Изм.	Кол.уч.	Лист	№ док.	Подп.	Дата
Архитектурные решения				Стадия	Лист
				ПД	13
Кочнева				ООО "ПБ Р1"	
Ситчихина					

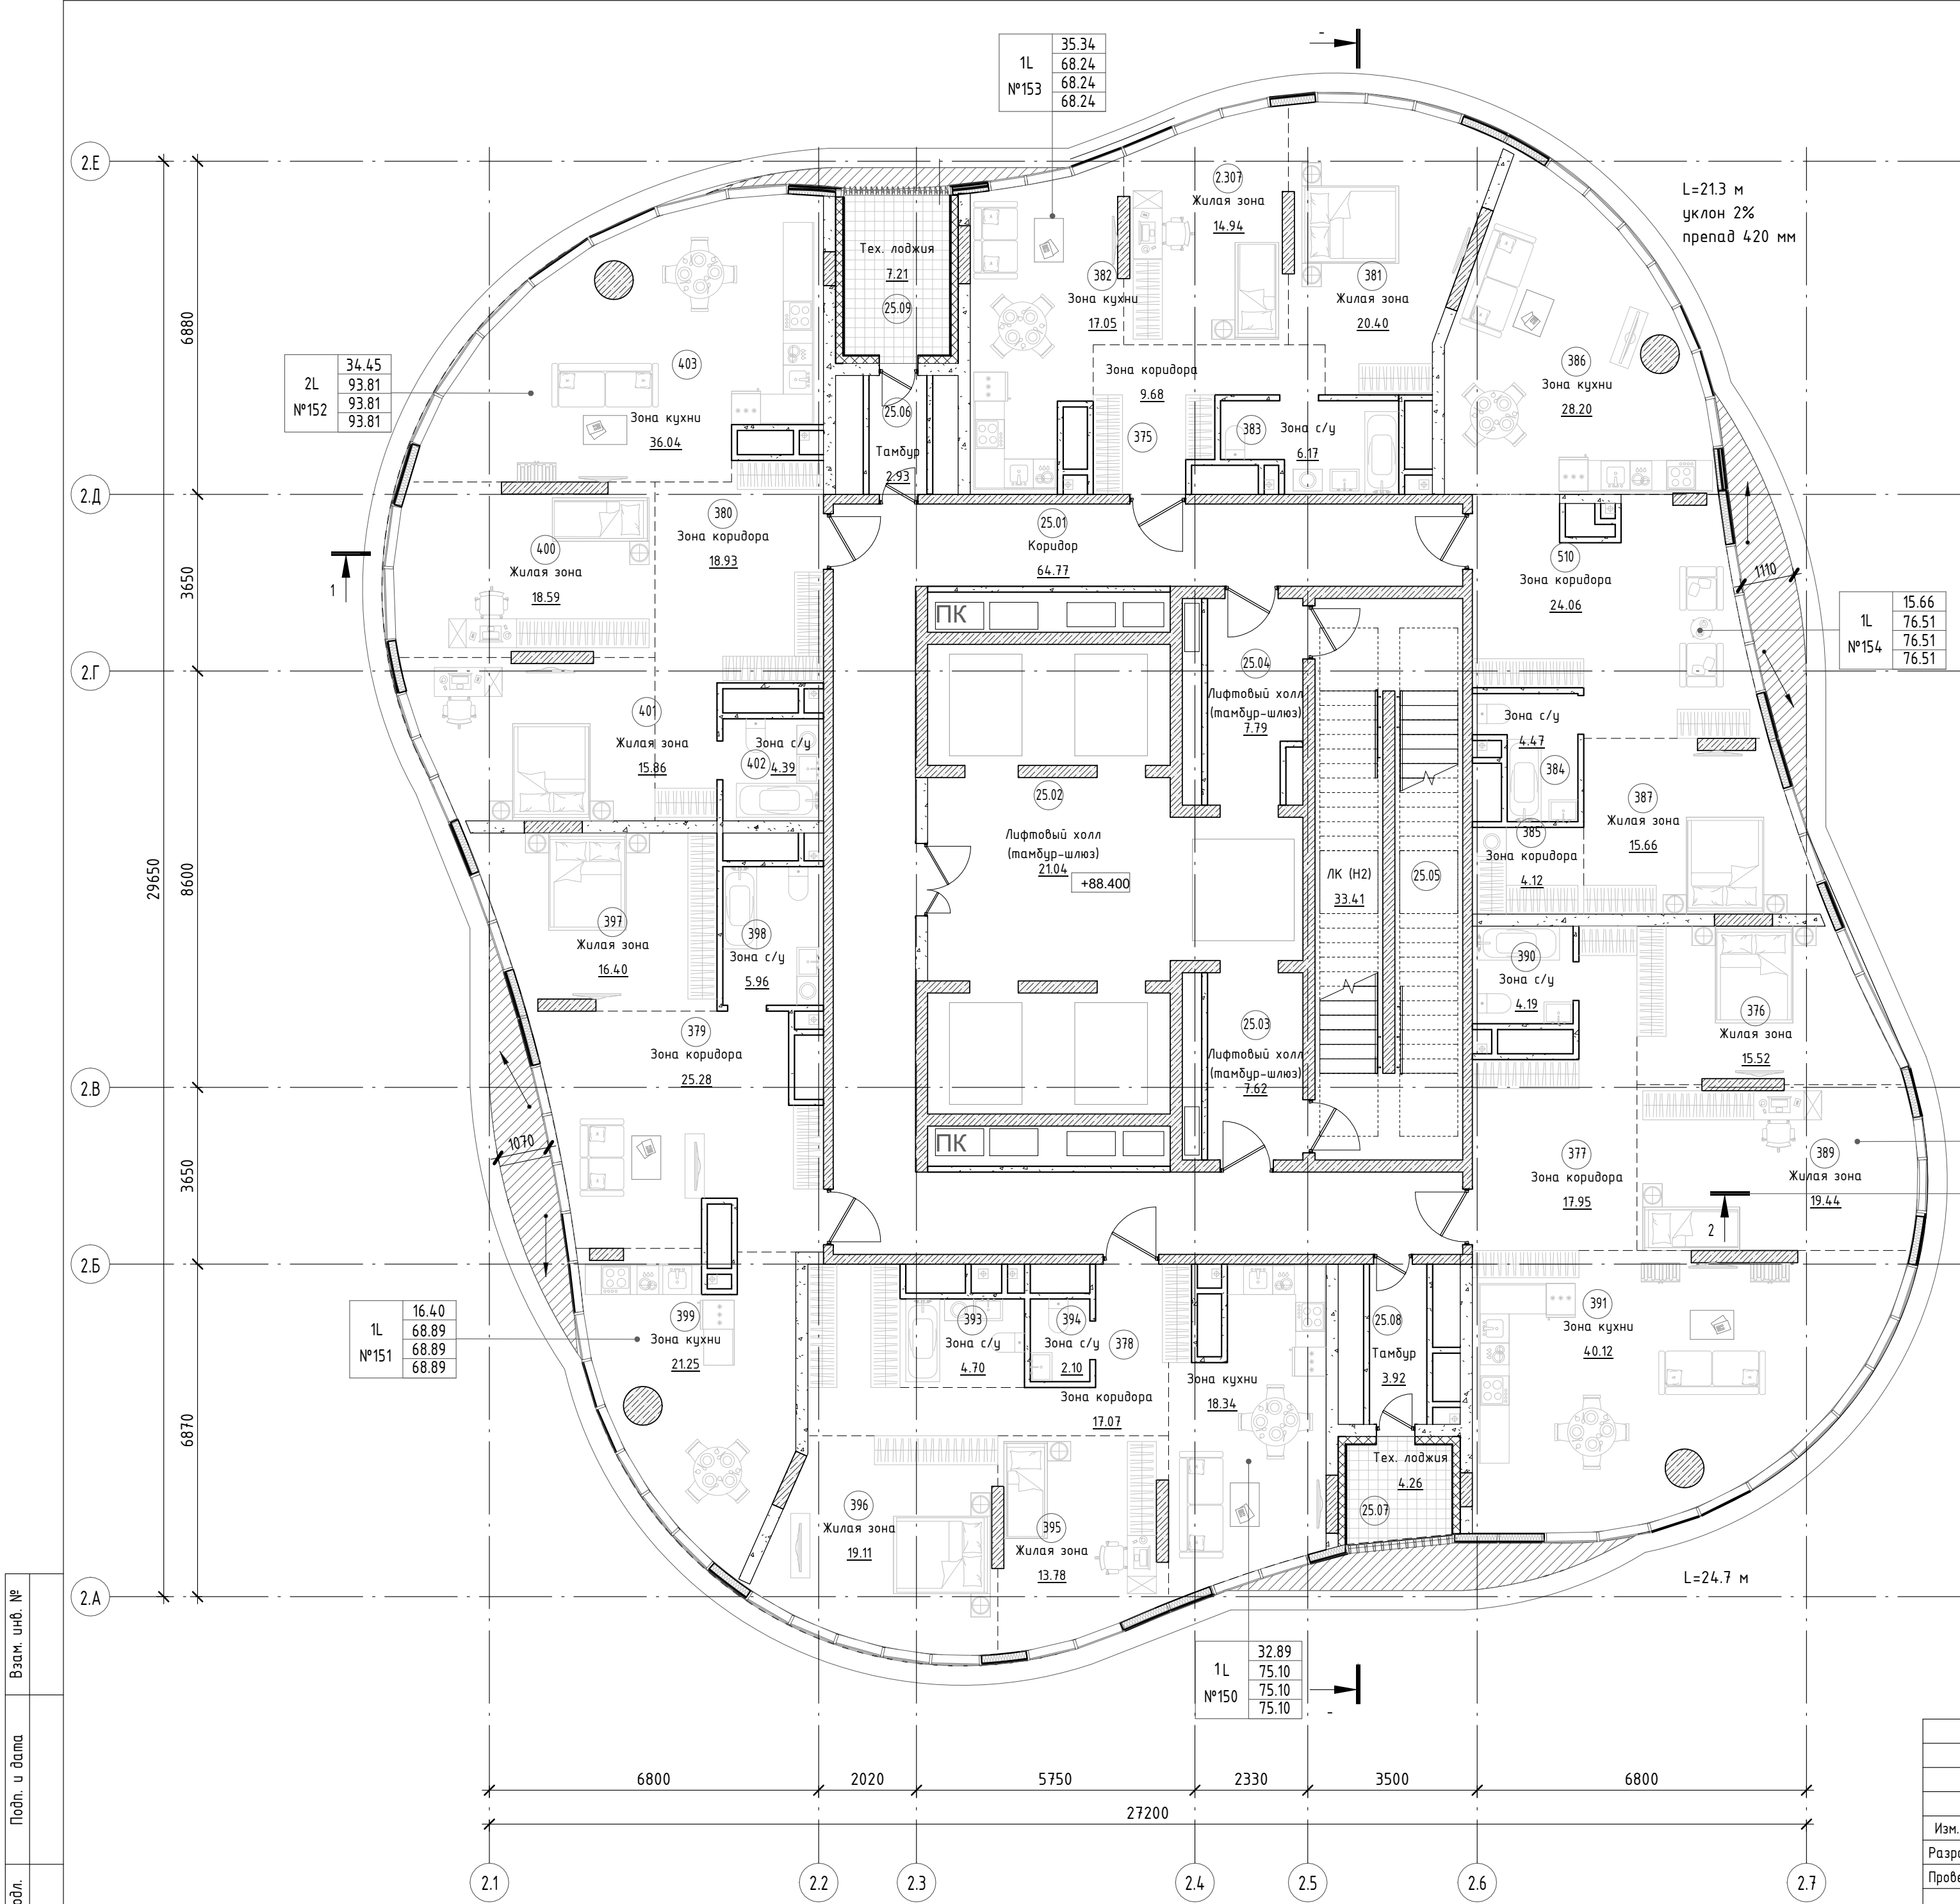


МОП			
25.01	Коридор	64.77	
25.02	Лифтовый холл (тамбур-шлюз)	21.04	
25.03	Лифтовый холл (тамбур-шлюз)	7.62	
25.04	Лифтовый холл (тамбур-шлюз)	7.79	
25.05	ЛК (H2)	33.41	
25.06	Тамбур	2.93	
25.07	Тех. лоджия	4.26	
25.08	Тамбур	3.92	
25.09	Тех. лоджия	7.21	
		152.96	


Маш/пом	33
	32
	31
	30
	29
	28
	27
	26
	25
	24
	23
	22
	21
	20
	19
	18
	17
	16
	15
	14
	13
	12
	11
	10
	9
	8
	7
	6
	5
	4
	3
	2
	1
автостоянка	-1

Инд. № подл.	Взам. инв. №
Подп. и дата	


1506-2026-AP				
Корпус К-2				
Изм.	Кол.уч.	Лист	№ док.	Подп.
Разработал	Шерембеева			03.26
Проверил	Прилуцкая			03.26
Архитектурные решения				
ПД			Лист	Листов
			14	
ГИП			Кочнева	03.26
Н.Контроль			Ситчихина	03.26
План 25 этажа			ООО "ПБ Р1"	

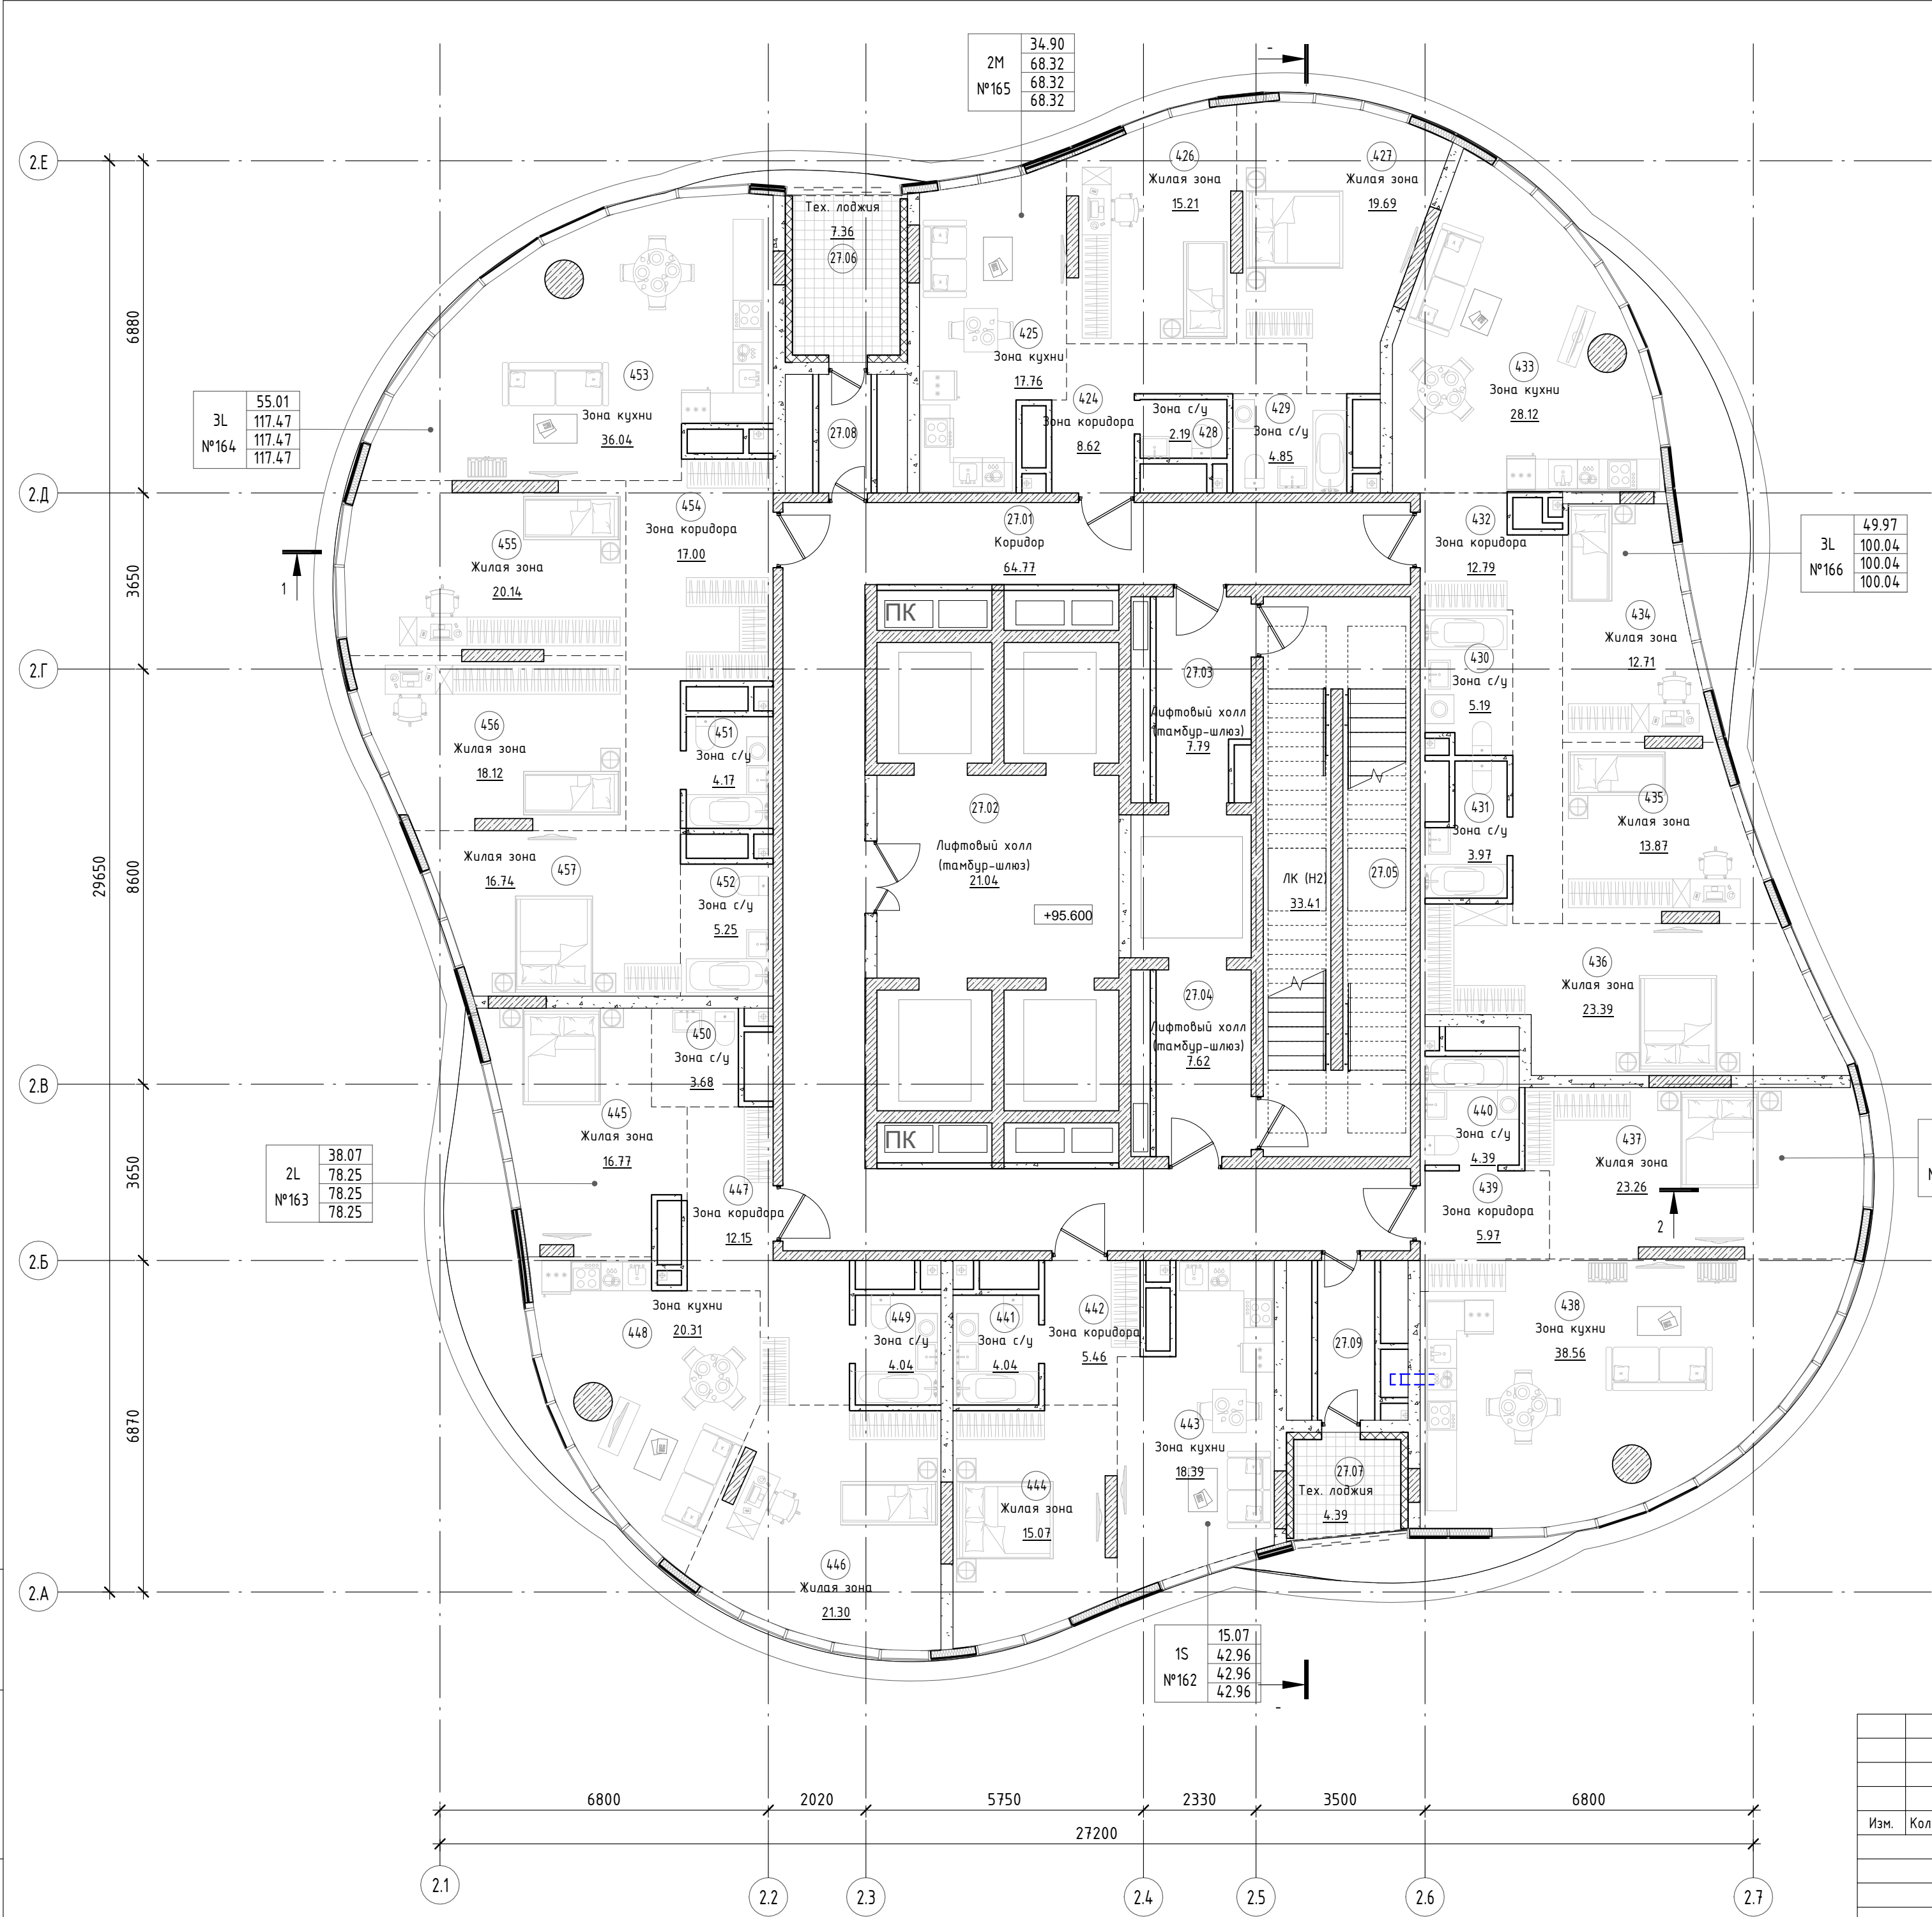


МОП			
27.01	Коридор	64.77	
27.02	Лифтовый холл (тамбур-шлюз)	21.04	
27.03	Лифтовый холл (тамбур-шлюз)	7.79	
27.04	Лифтовый холл (тамбур-шлюз)	7.62	
27.05	ЛК (Н2)	33.41	
27.06	Тех. лоджия	7.36	
27.07	Тех. лоджия	4.39	
27.08	Тамбур	2.68	
27.09	Тамбур	3.92	
		152.98	

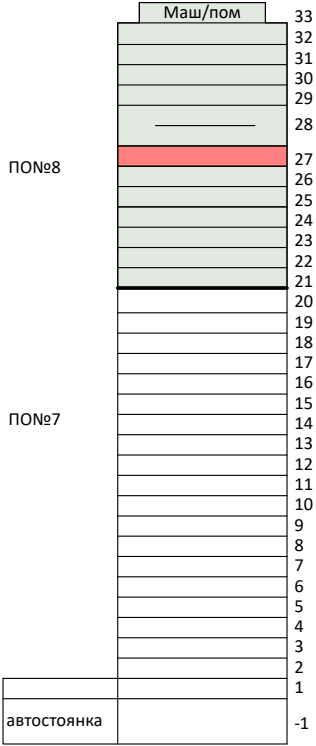



1506-2026-AP			
Корпус К-2			
Архитектурные решения	Стадия	Лист	Листов
	ПД	16	
План 27 этажа		ООО "ПБ Р1"	
Кочнева Ситчихина			

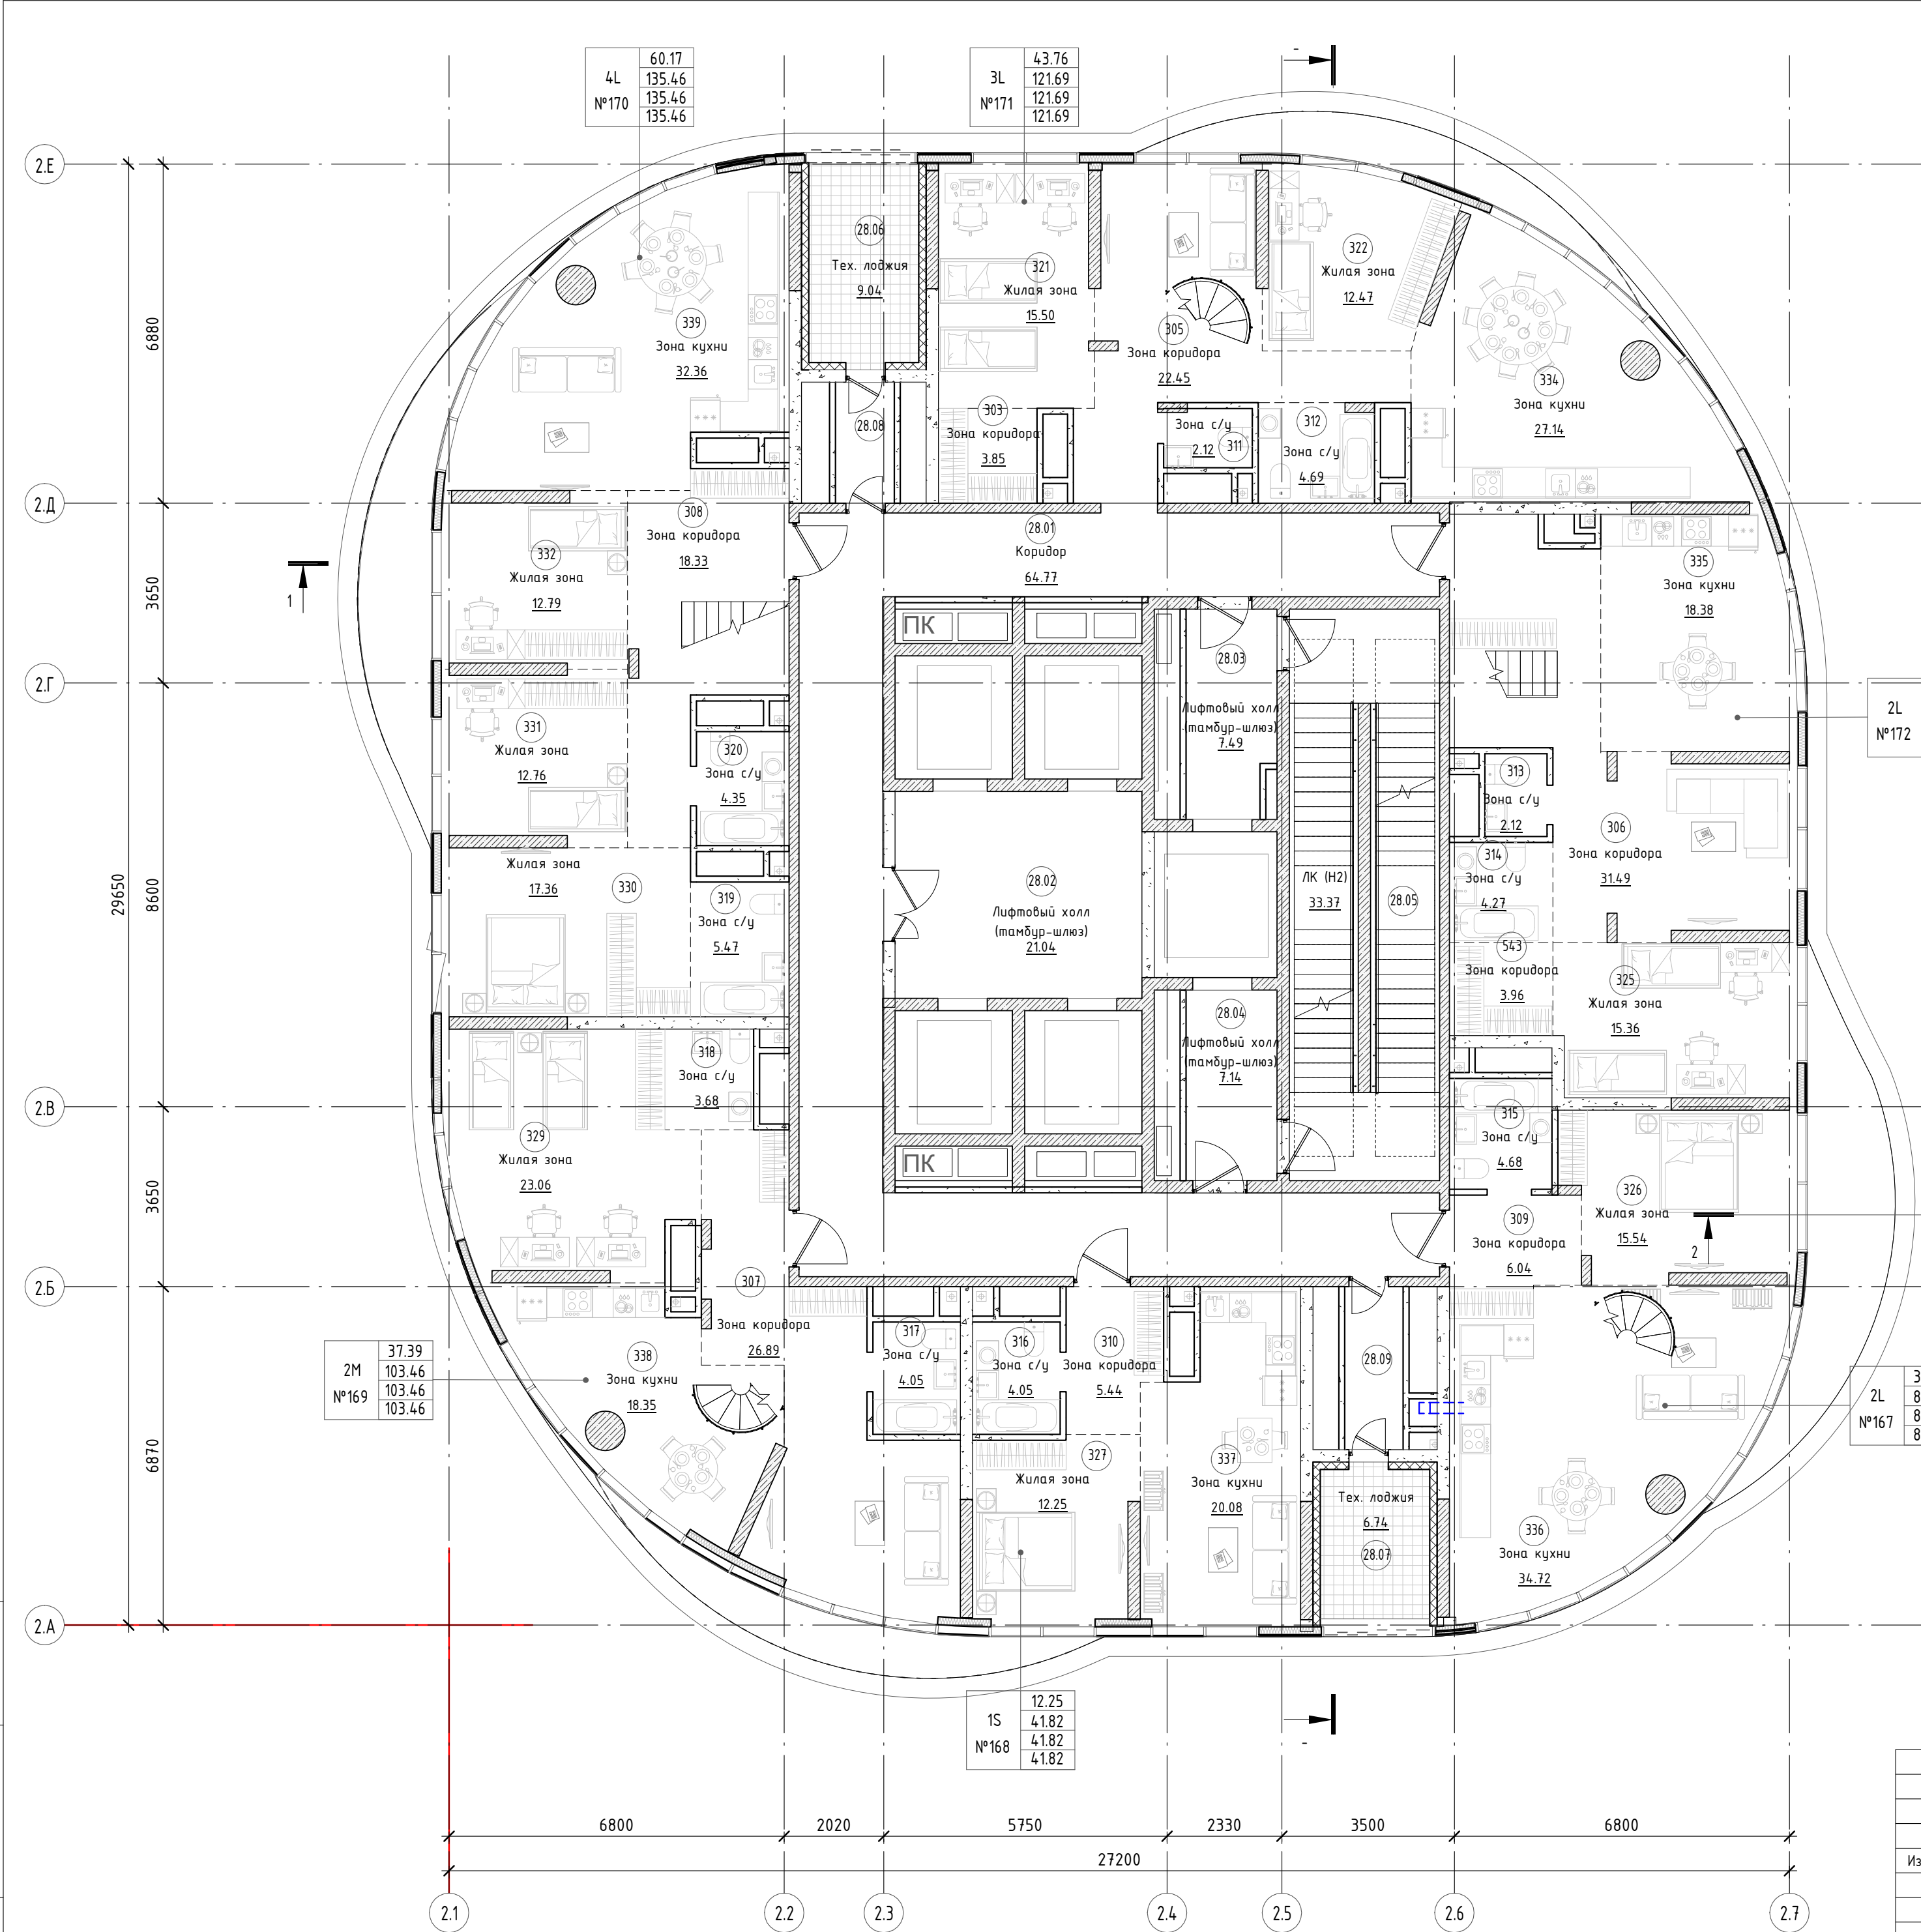


МОП			
28.01	Коридор	64.77	
28.02	Лифтовый холл (тамбур-шлюз)	21.04	
28.03	Лифтовый холл (тамбур-шлюз)	7.49	
28.04	Лифтовый холл (тамбур-шлюз)	7.14	
28.05	ЛК (H2)	33.37	
28.07	Тех. лоджия	6.74	
		140.54	

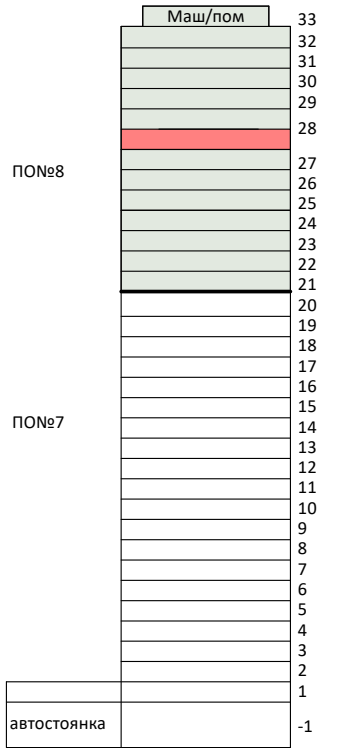

1506-2026-AP					
Корпус К-2					
Изм.		Кол.уч.	Лист	№ док.	Подп.
Дата		Архитектурные решения		Стадия	Лист
				ПД	17
		План 28 этажа		ООО "ПБ Р1"	
		Кочнева			
		Ситчихина			

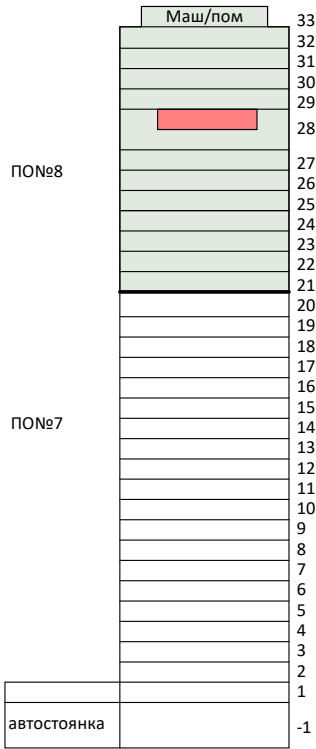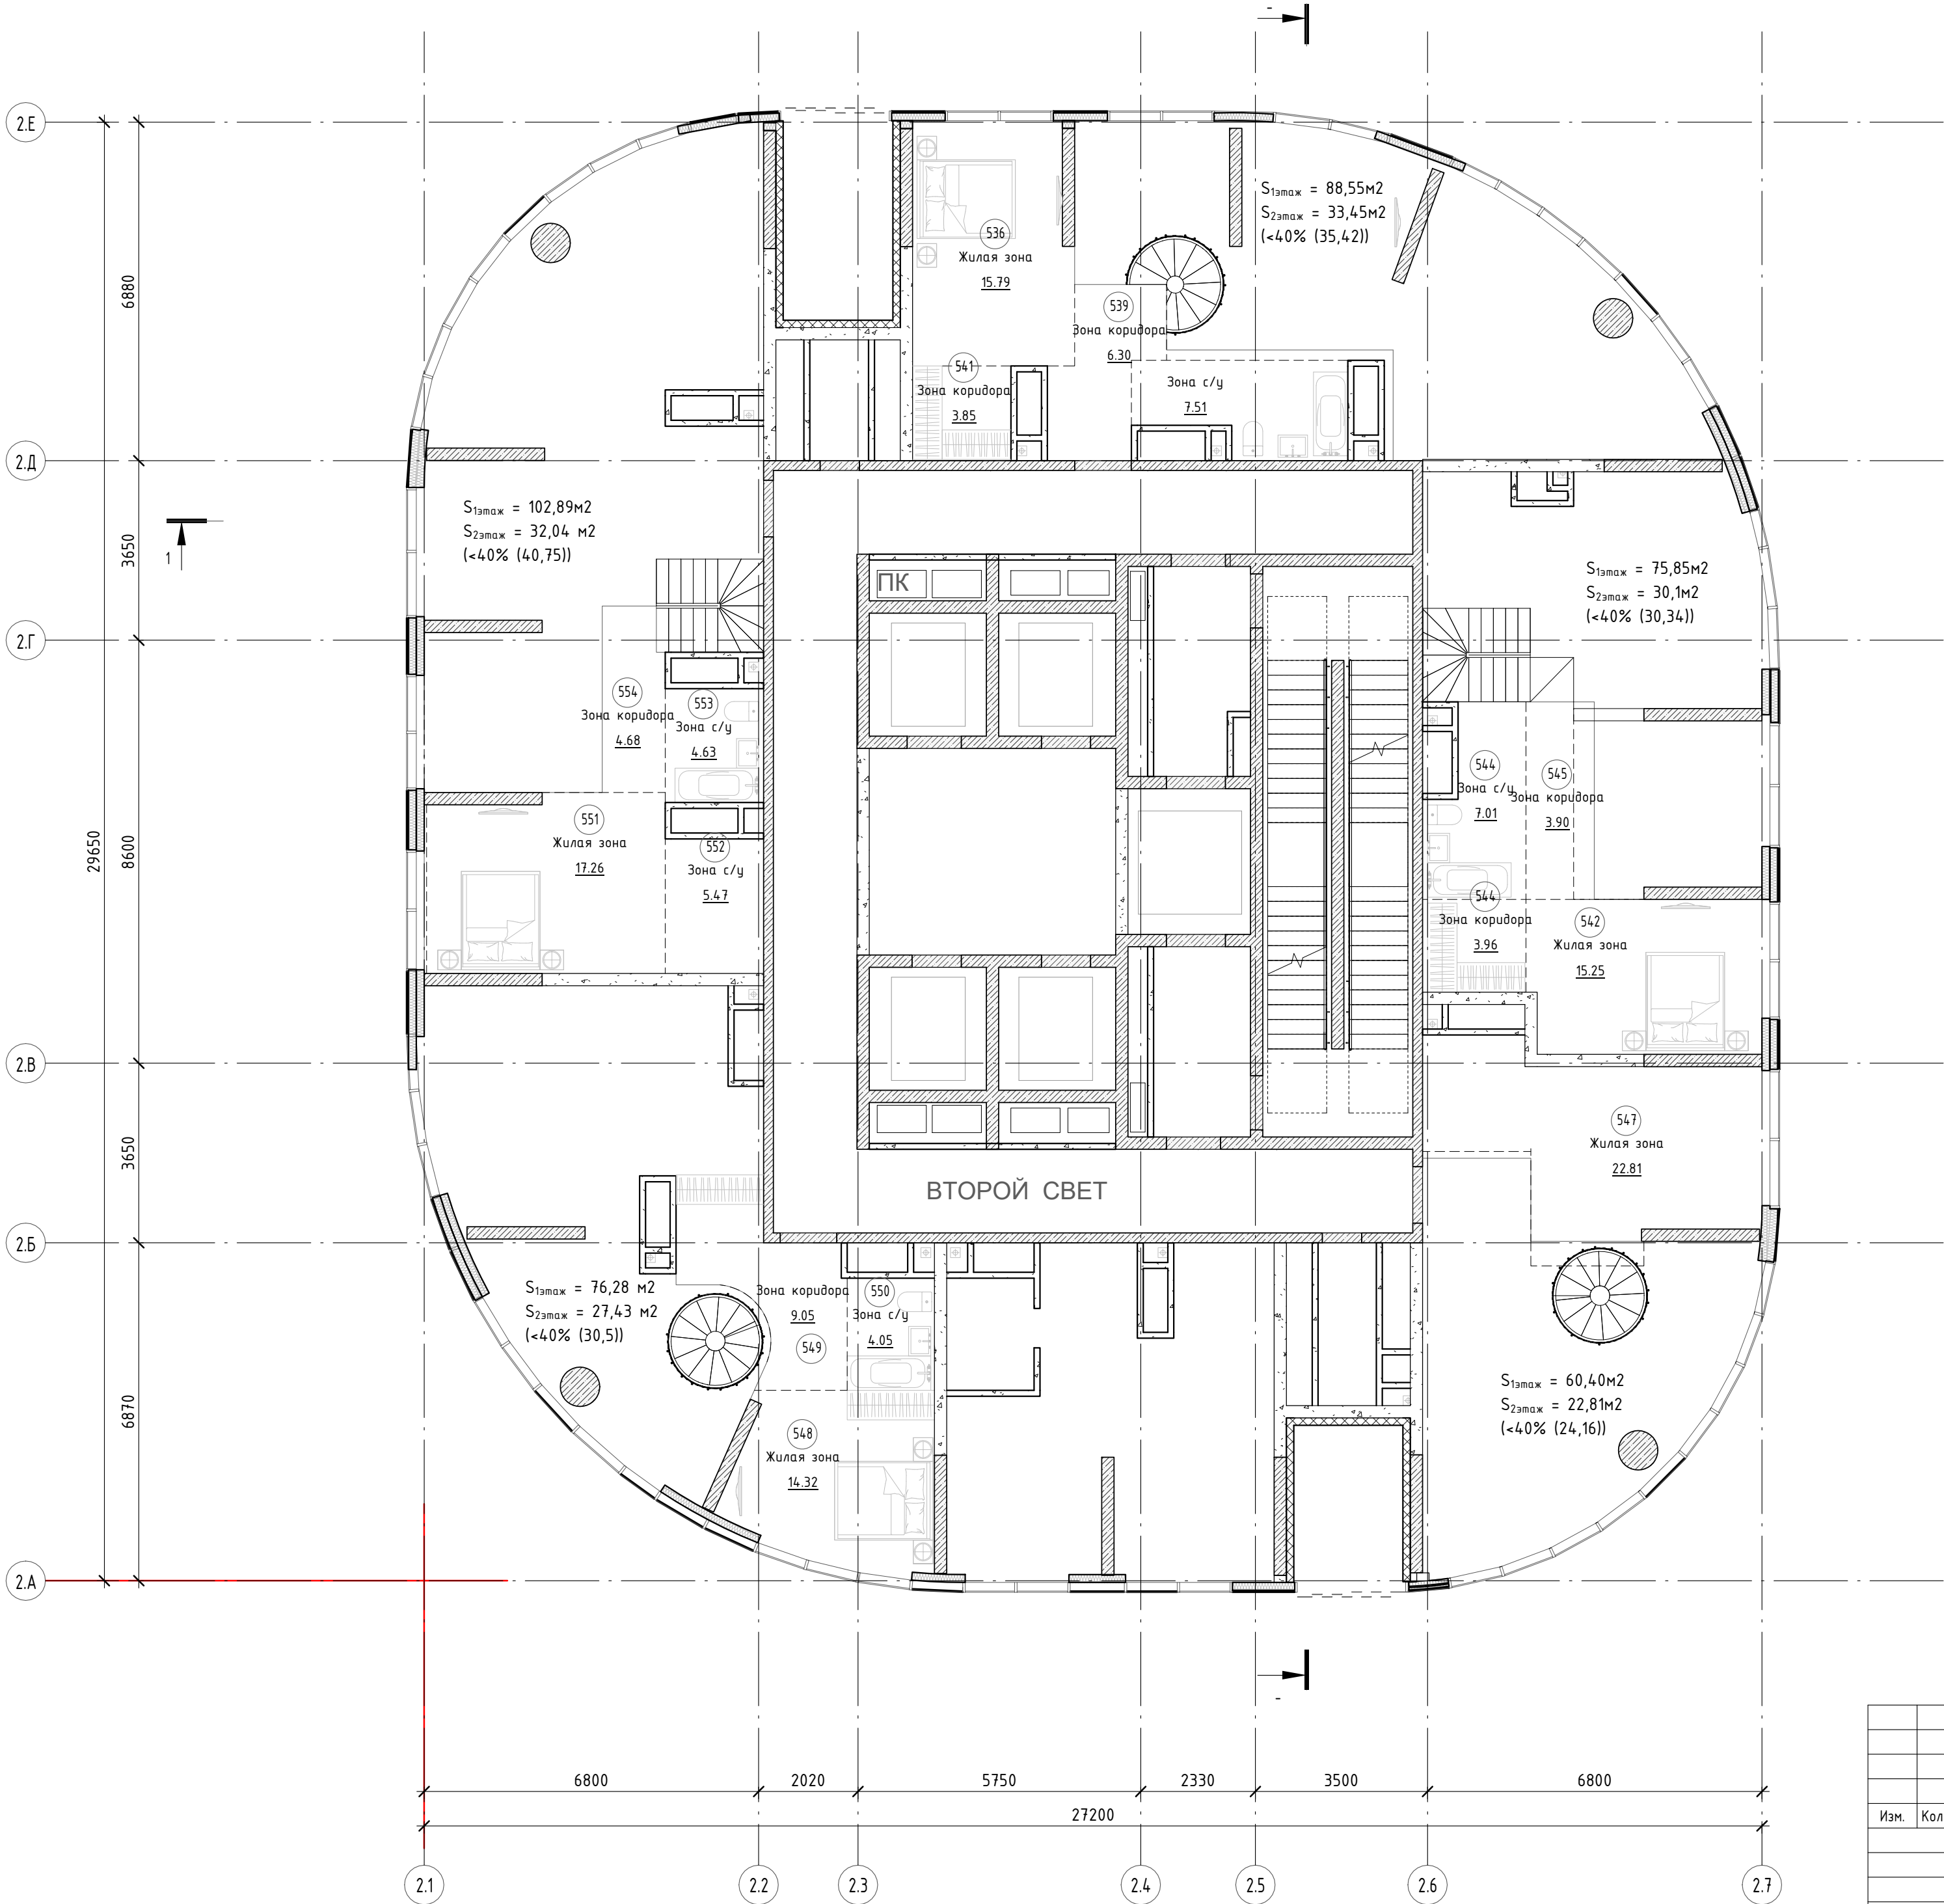


						1506-2026-AP				
						Корпус К-2				
Изм.	Кол.уч.	Лист	№ док.	Подп.	Дата	Архитектурные решения	Стадия	Лист	Листов	
							ПД	18		
							План 28 этажа (антресоли)	ООО "ПБ Р1"		

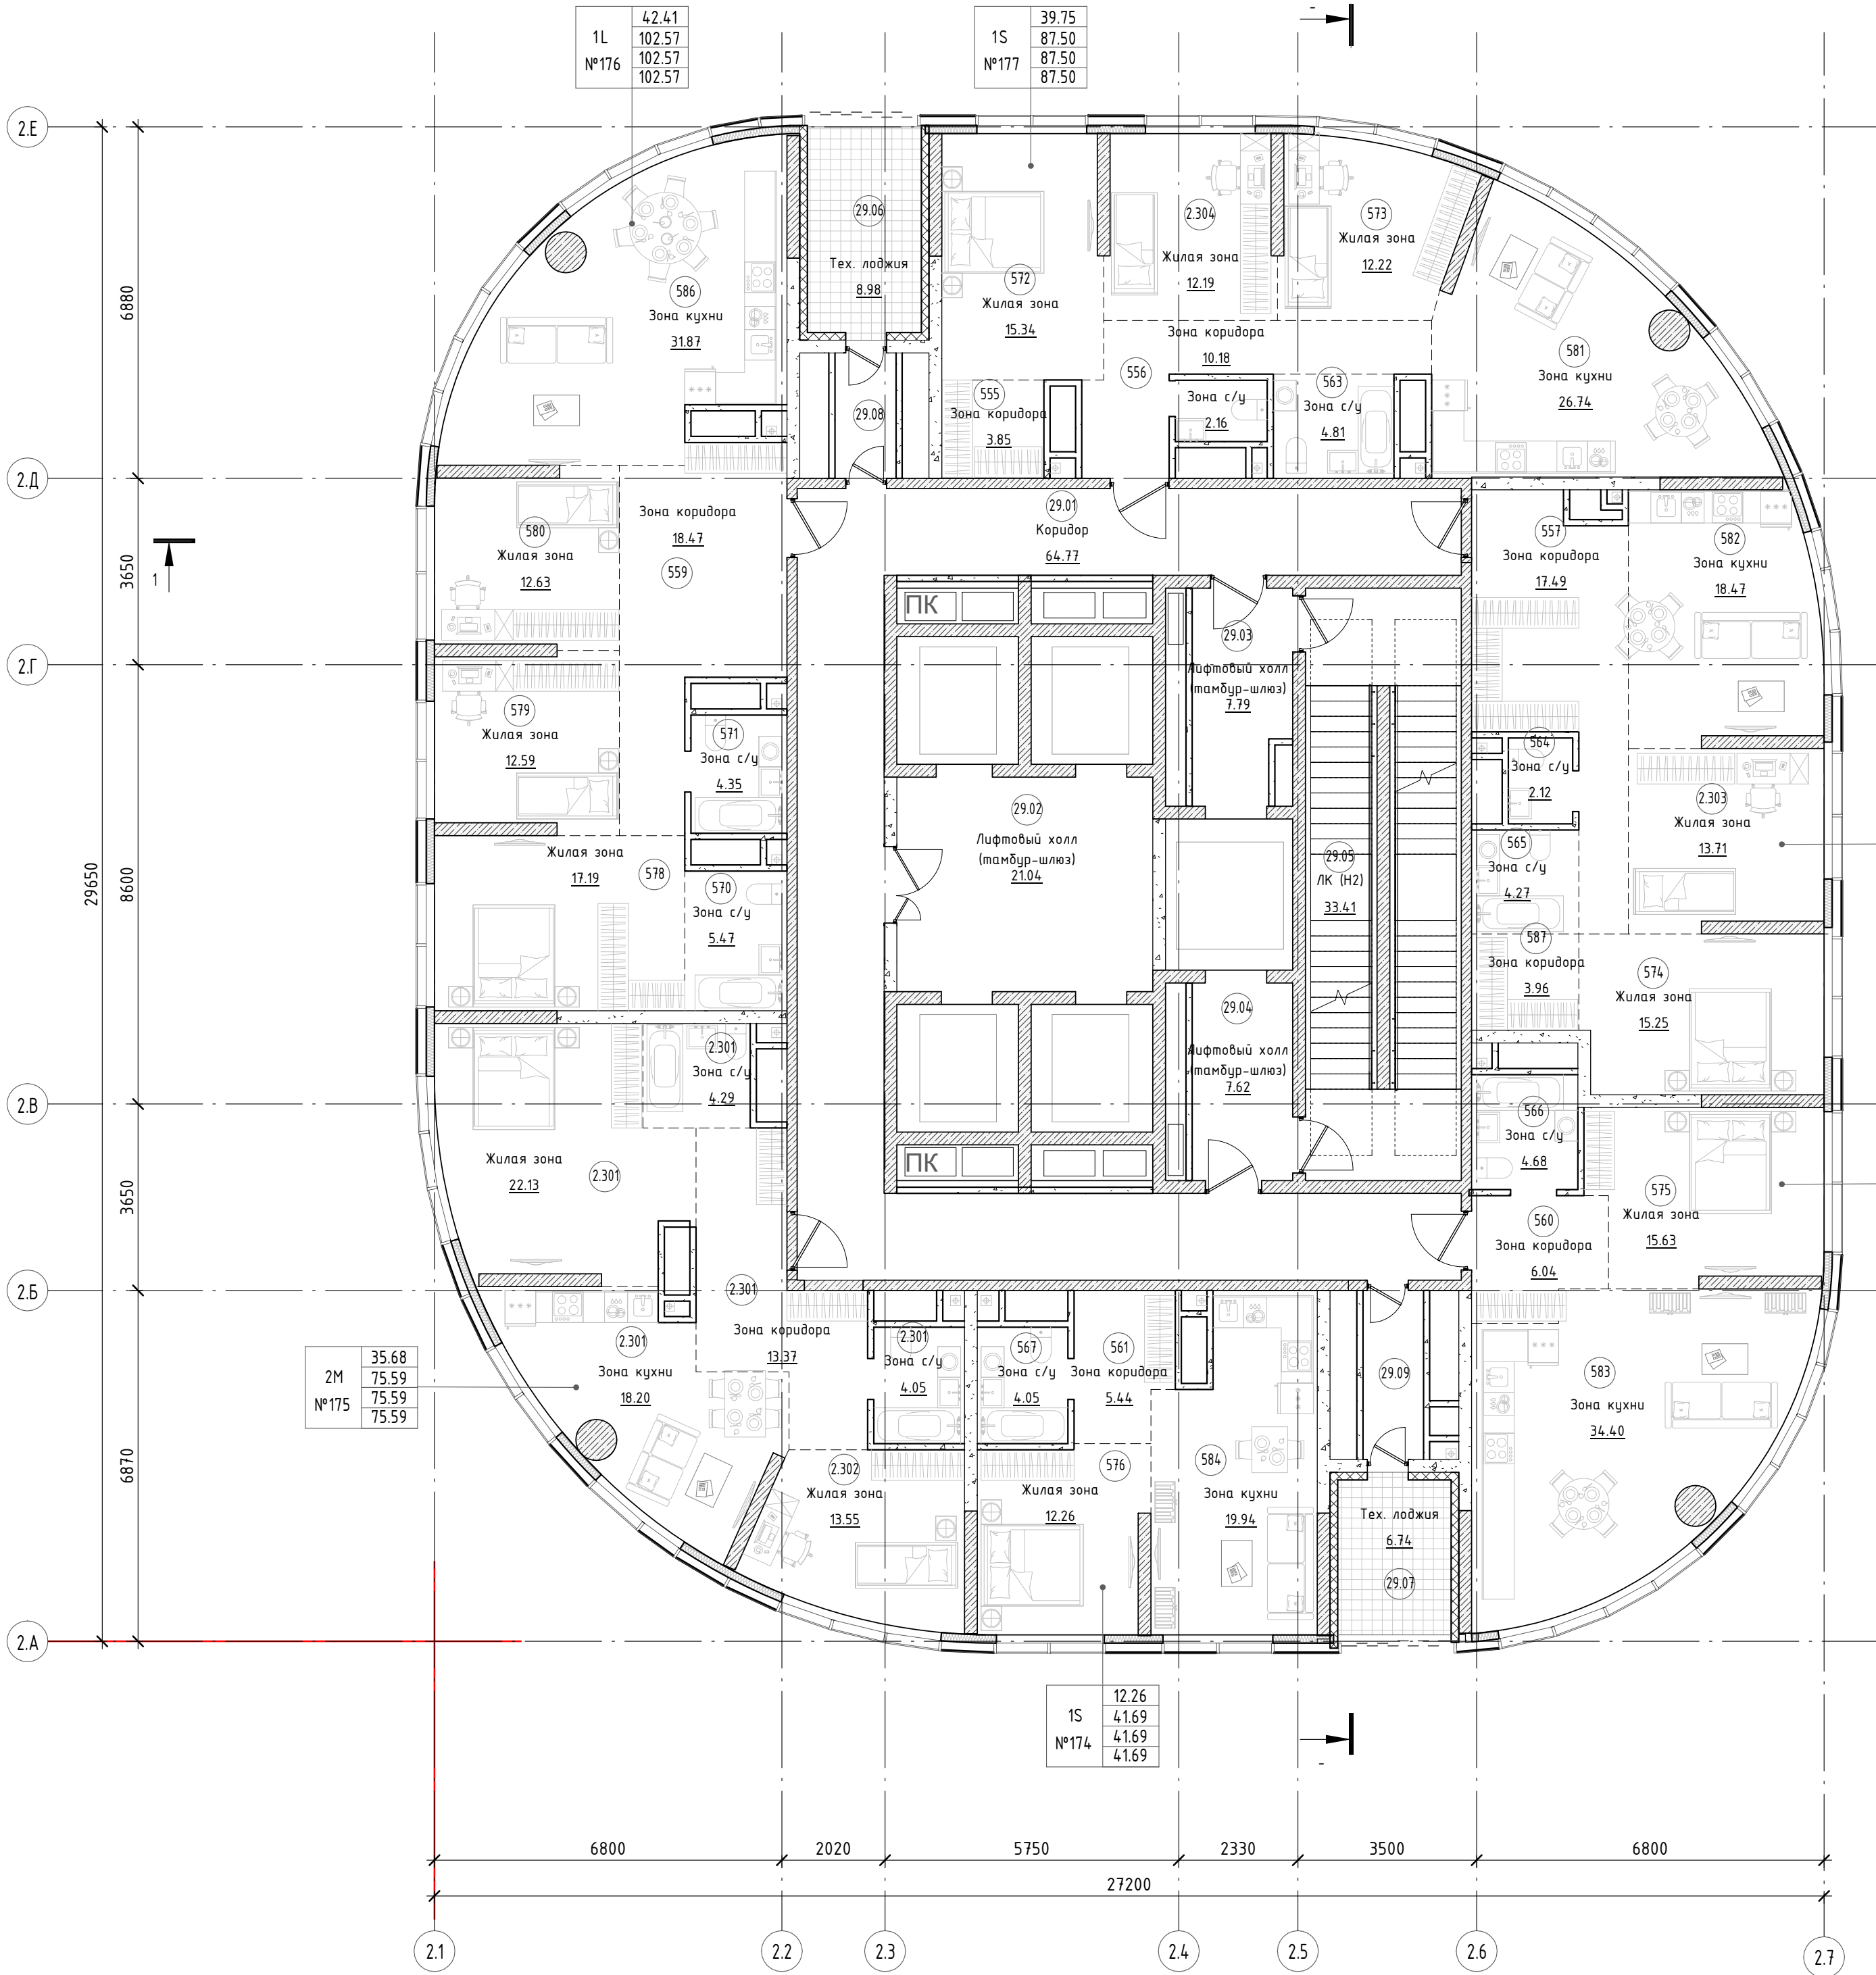

МОП			
29.01	Коридор	64.77	
29.02	Лифтовый холл (тамбур-шлюз)	21.04	
29.03	Лифтовый холл (тамбур-шлюз)	7.79	
29.04	Лифтовый холл (тамбур-шлюз)	7.62	
29.05	ЛК (H2)	33.41	
29.06	Тех. лоджия	8.98	
29.07	Тех. лоджия	6.74	
29.08	Тамбур	2.93	
29.09	Тамбур	3.92	
		157.20	

ПОИ#8	Маш/пом	33
		32
		31
		30
		29
		28
		27
		26
		25
		24
ПОИ#7		23
		22
		21
		20
		19
		18
		17
		16
		15
		14
автостоянка		13
		12
		11
		10
		9
		8
		7
		6
		5
		4
		3
		2
		1
		-1

						1506-2026-AP				
						Корпус К-2				
Изм.	Кол.уч.	Лист	№ док.	Подп.	Дата	Архитектурные решения	Стадия	Лист	Листов	
							ПД	19		
							План 29-30 этажей	000 "ПБ Р1"		
					</					

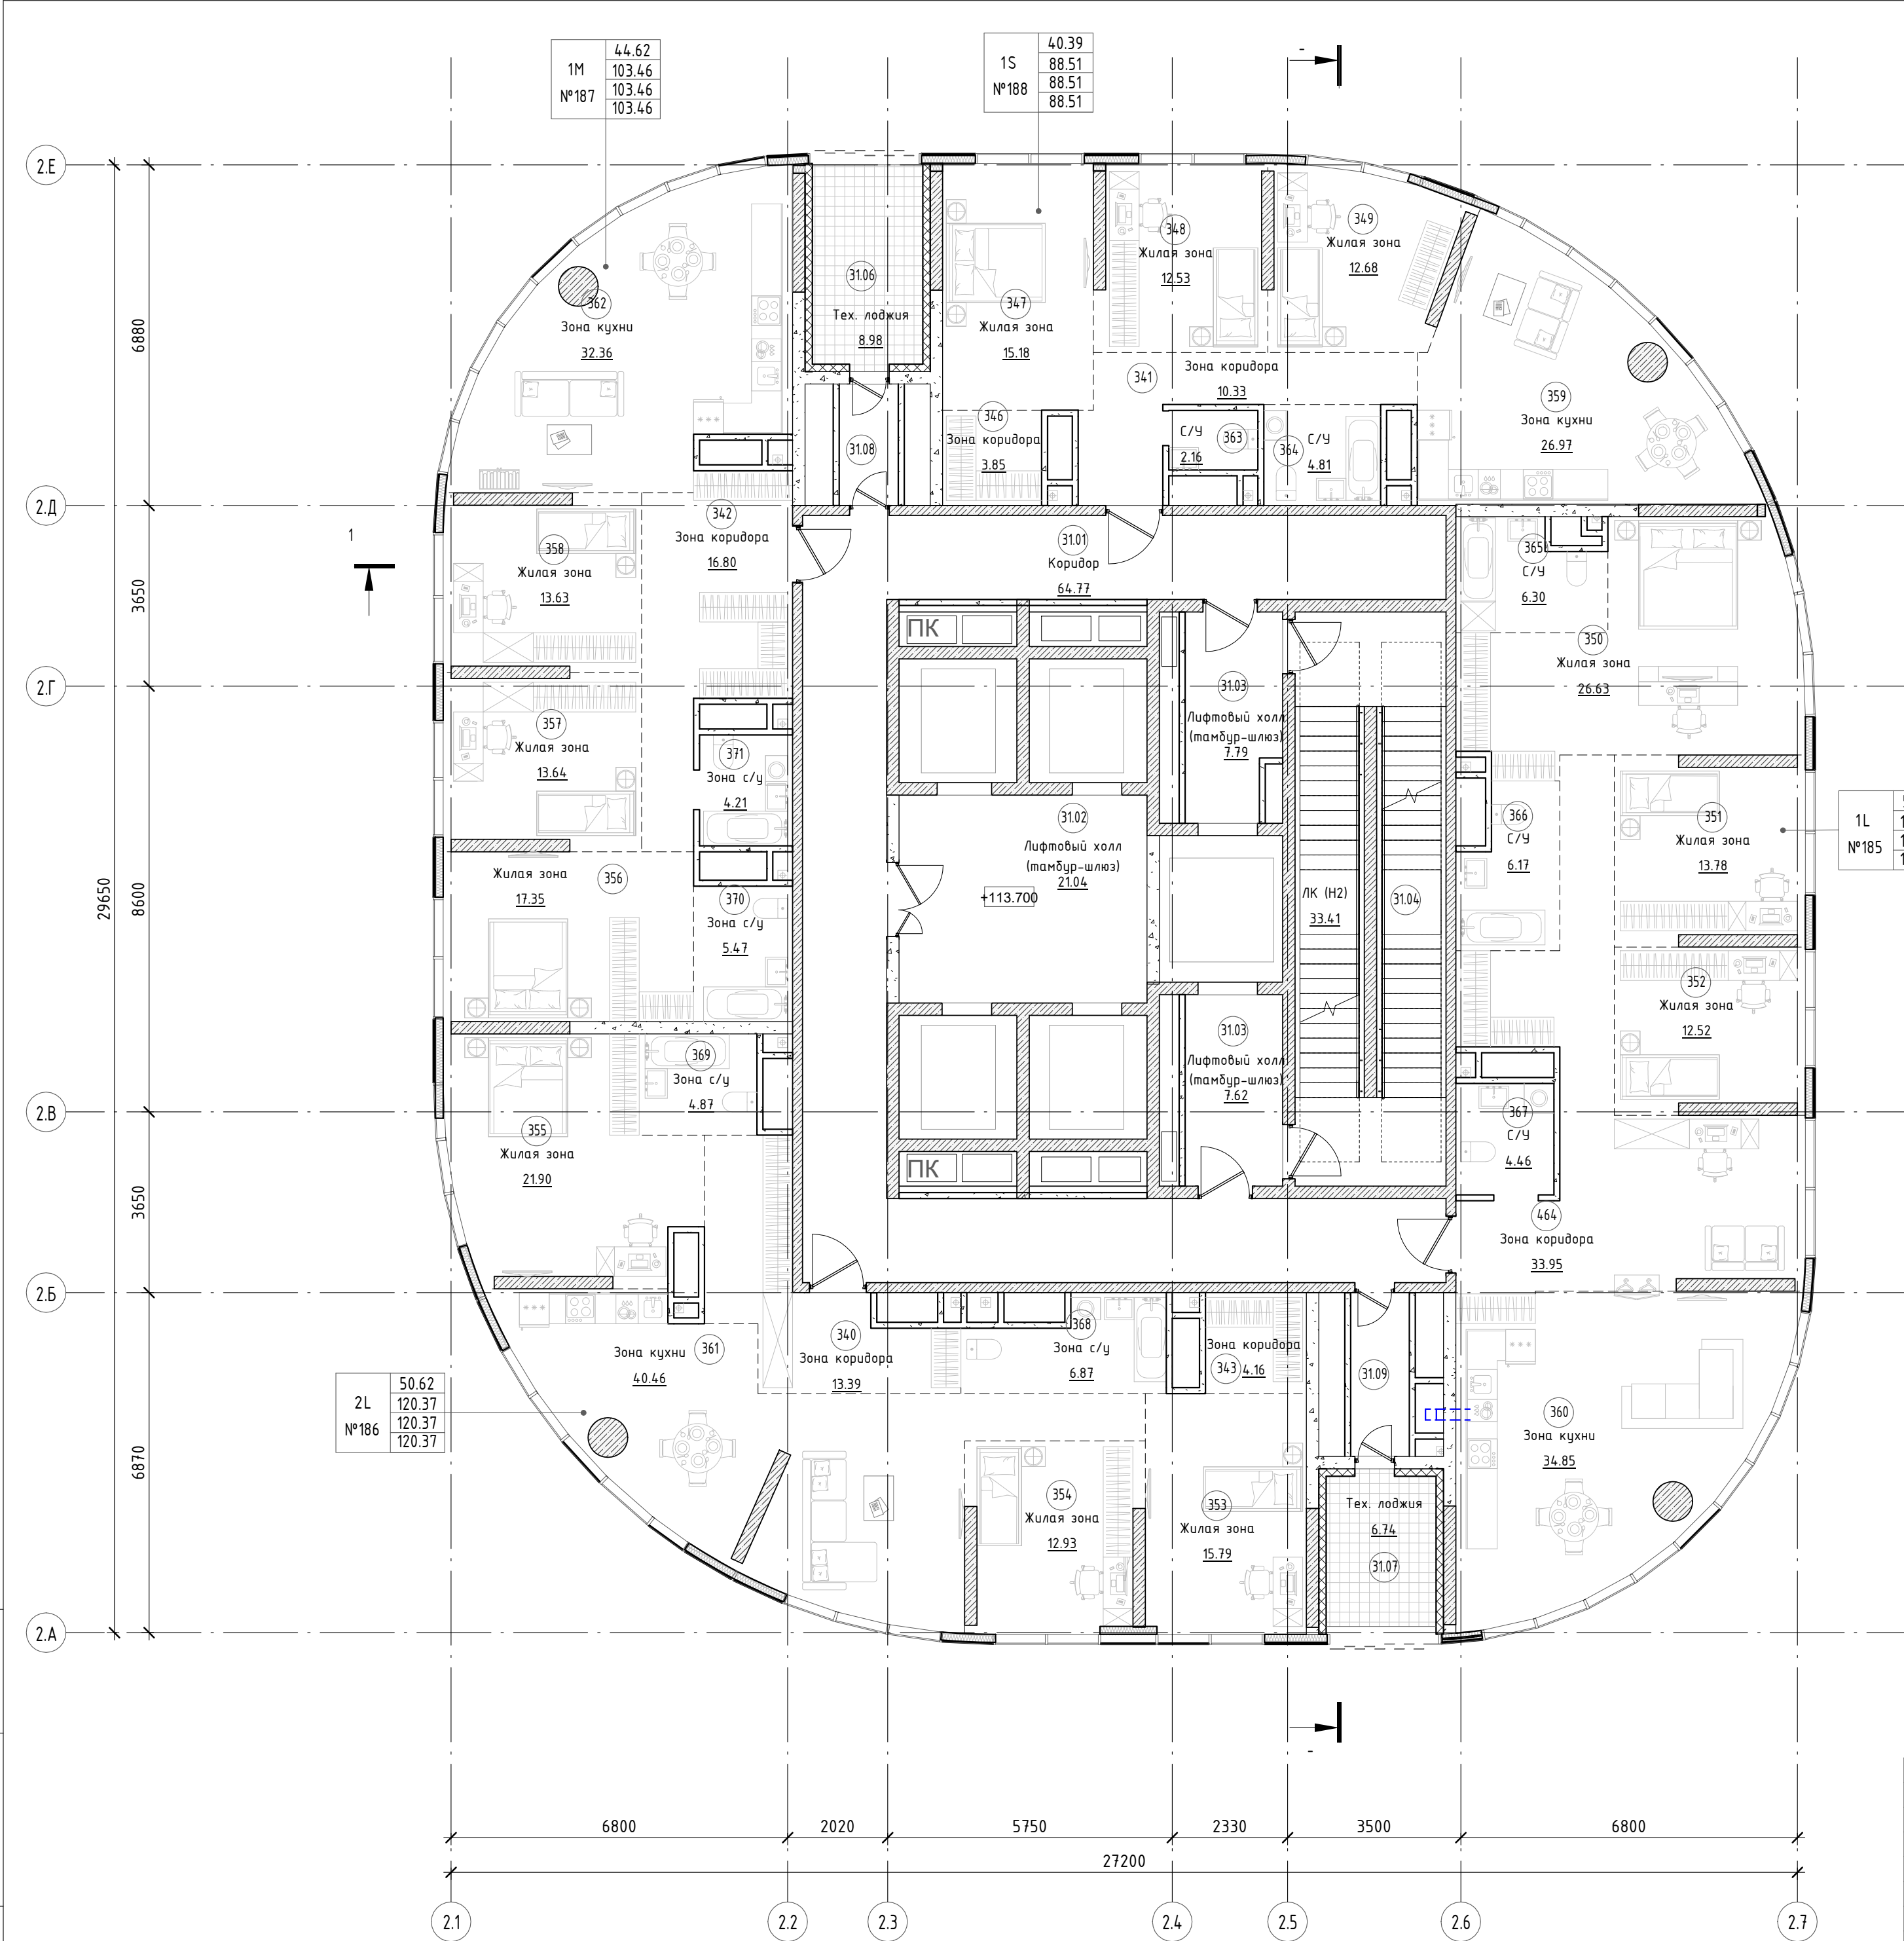

МОП			
31.01	Коридор	64.77	
31.02	Лифтовый холл (тамбур-шлюз)	21.04	
31.03	Лифтовый холл (тамбур-шлюз)	7.79	
31.03	Лифтовый холл (тамбур-шлюз)	7.62	
31.04	ЛК (H2)	33.41	
31.06	Тех. лоджия	8.98	
31.07	Тех. лоджия	6.74	
31.08	Тамбур	2.93	
31.09	Тамбур	3.92	
		157.20	

1L	52.93
№185	138.66
	138.66
	138.66


2L	50.62
№186	120.37
	120.37
	120.37

1M	44.62
№187	103.46
	103.46
	103.46

1S	40.39
№188	88.51
	88.51
	88.51

Маш/пом	33
	32
	31
	30
	29
	28
	27
	26
	25
	24
	23
	22
	21
	20
	19
	18
	17
	16
	15
	14
	13
	12
	11
	10
	9
	8
	7
	6
	5
	4
	3
	2
	1
автостоянка	-1

1506-2026-AP				
Корпус К-2				
Изм.	Кол.уч.	Лист	№ док.	Подп.
				Дата
Архитектурные решения			Стадия	Лист
			ПД	20
План 31 этажа			ООО "ПБ Р1"	
Кочнева				
Ситчихина				

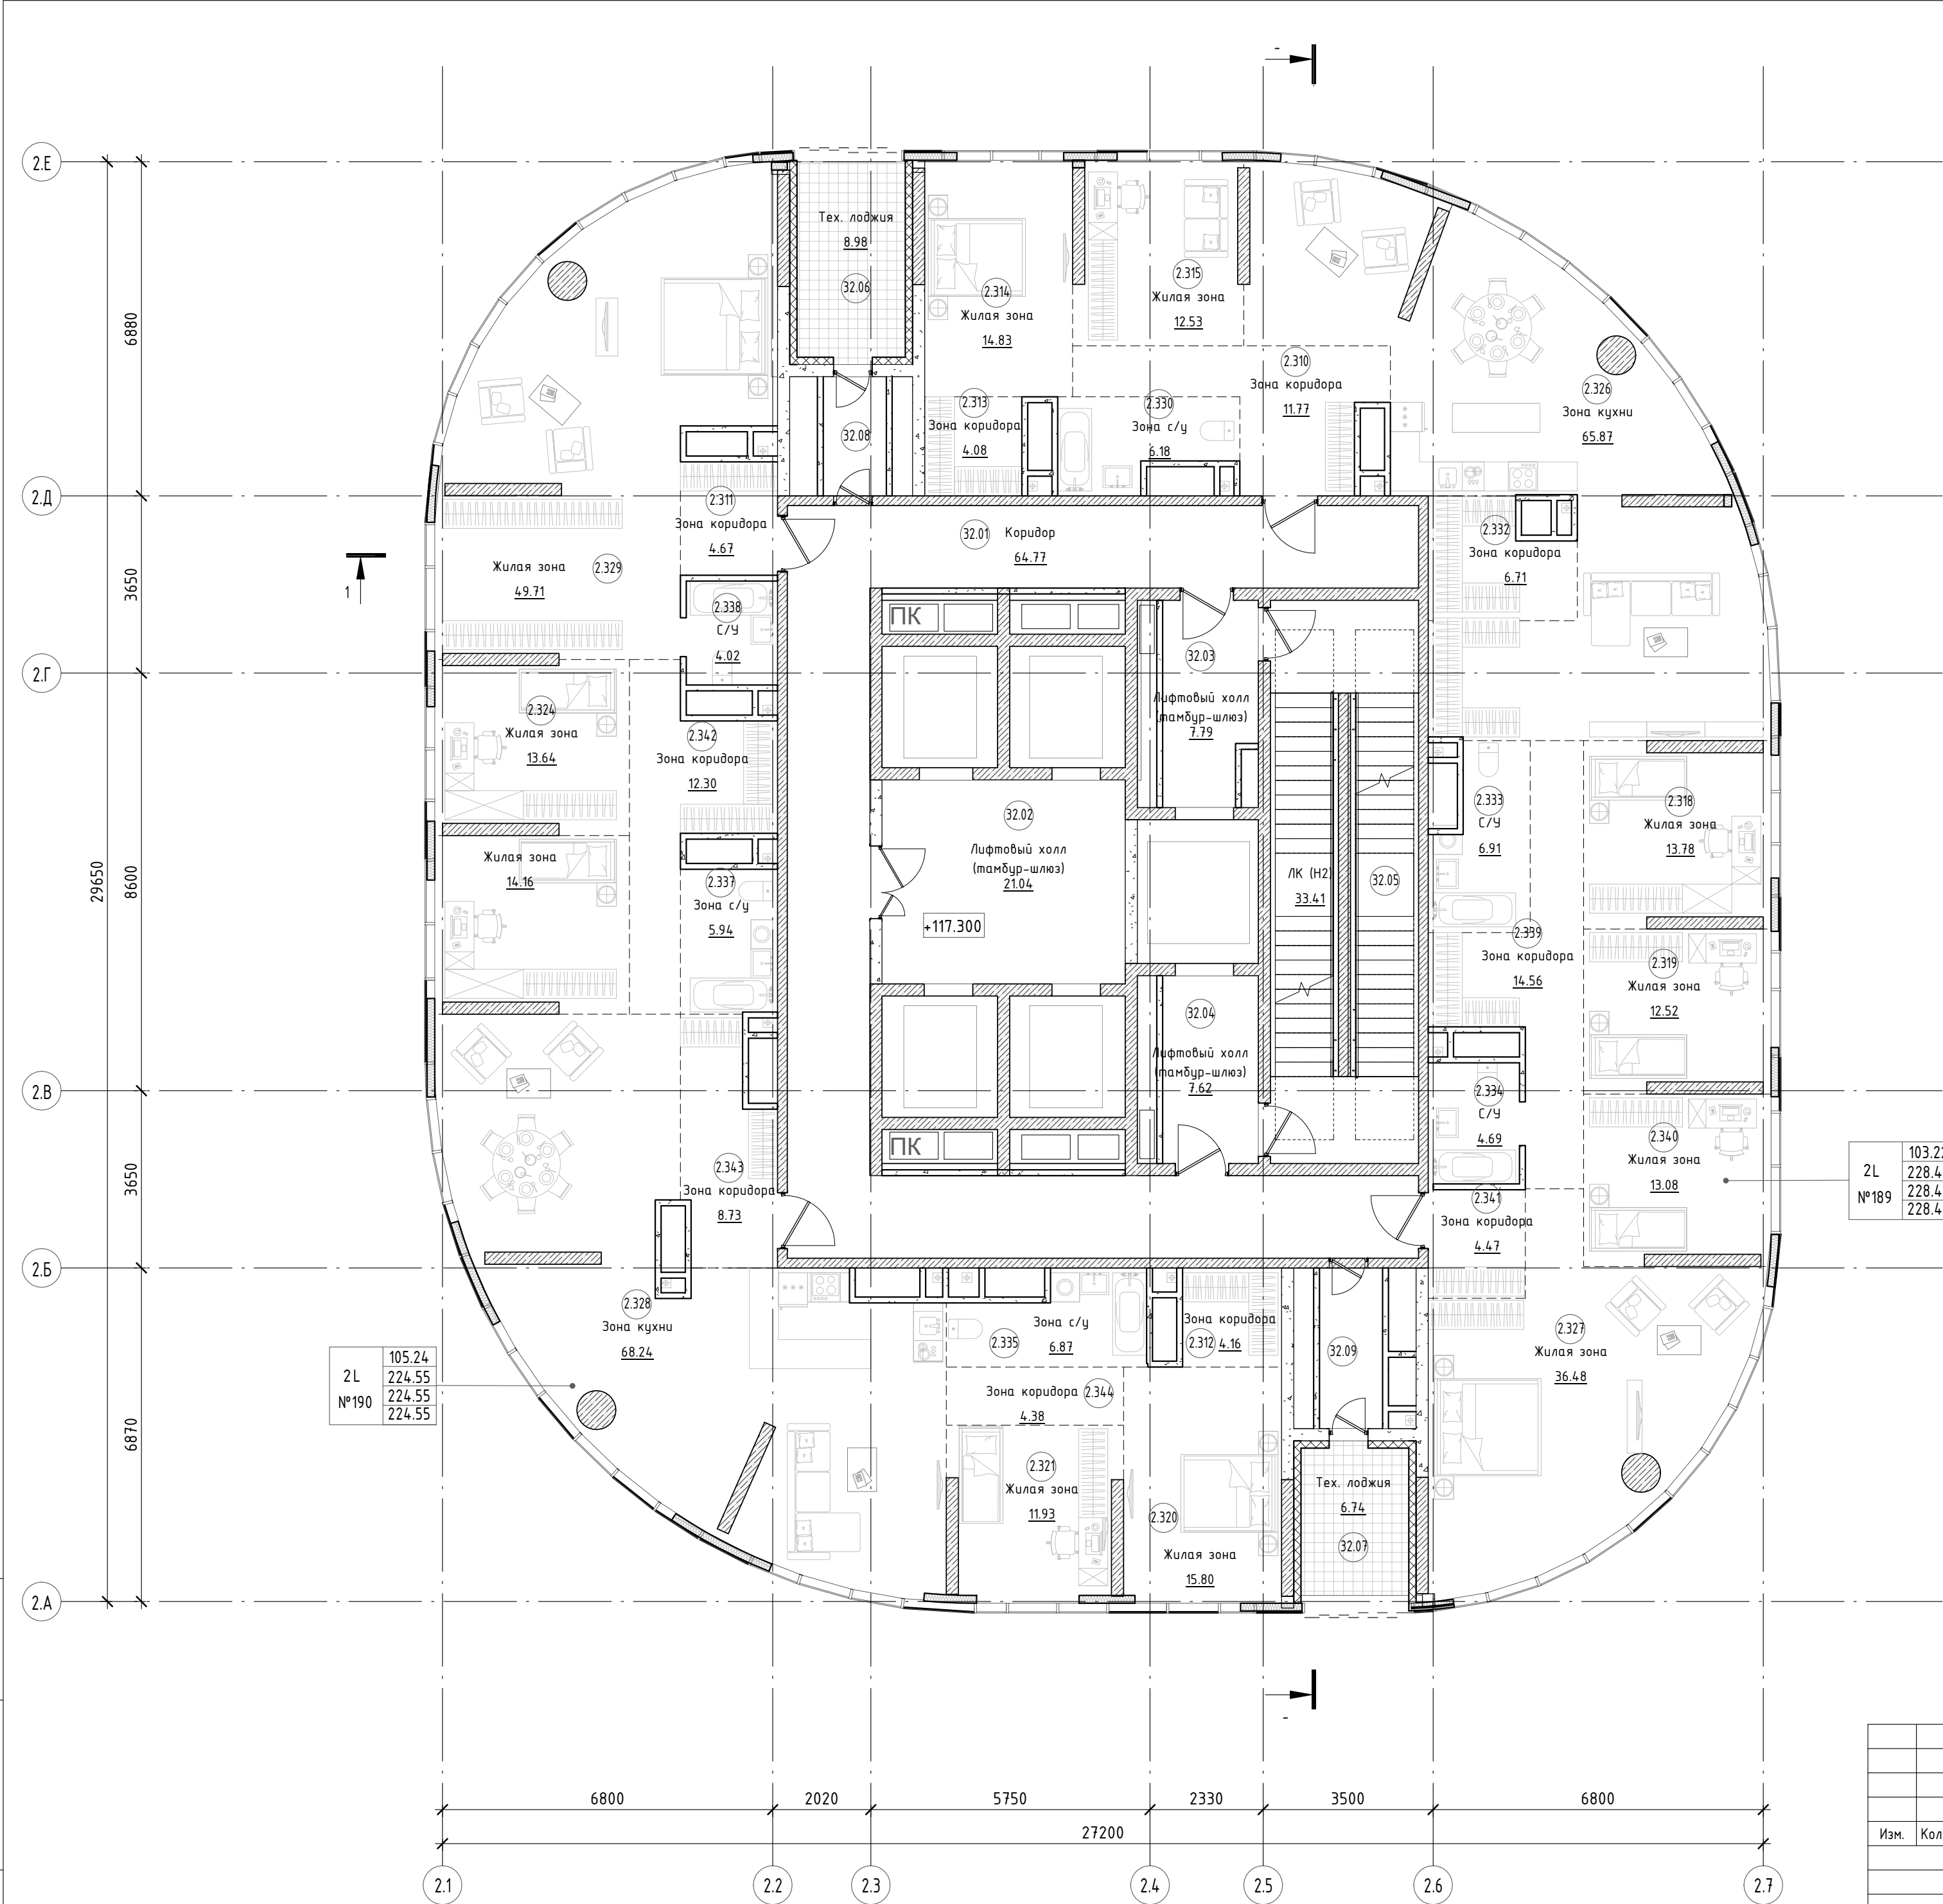


МОП			
32.01	Коридор	64.77	
32.02	Лифтовый холл (тамбур-шлюз)	21.04	
32.03	Лифтовый холл (тамбур-шлюз)	7.79	
32.04	Лифтовый холл (тамбур-шлюз)	7.62	
32.05	ЛК (H2)	33.41	
32.06	Тех. лоджия	8.98	
32.07	Тех. лоджия	6.74	
32.08	Тамбур	3.19	
32.09	Тамбур	4.30	
		157.84	

2L	103.22
№189	228.46
	228.46
	228.46

2L	105.24
№190	224.55
	224.55
	224.55

Маш/пом	33
	32
	31
	30
	29
	28
	27
	26
	25
	24
	23
	22
	21
	20
	19
	18
	17
	16
	15
	14
	13
	12
	11
	10
	9
	8
	7
	6
	5
	4
	3
	2
	1
автостоянка	-1

						1506-2026-AP				
						Корпус К-2				
Изм.	Кол.уч.	Лист	№ док.	Подп.	Дата	Архитектурные решения	Стадия	Лист	Листов	
							ПД	21		
							План 32 этажа	000 "ПБ Р1"		
		Кочнева								
		Ситчихина								

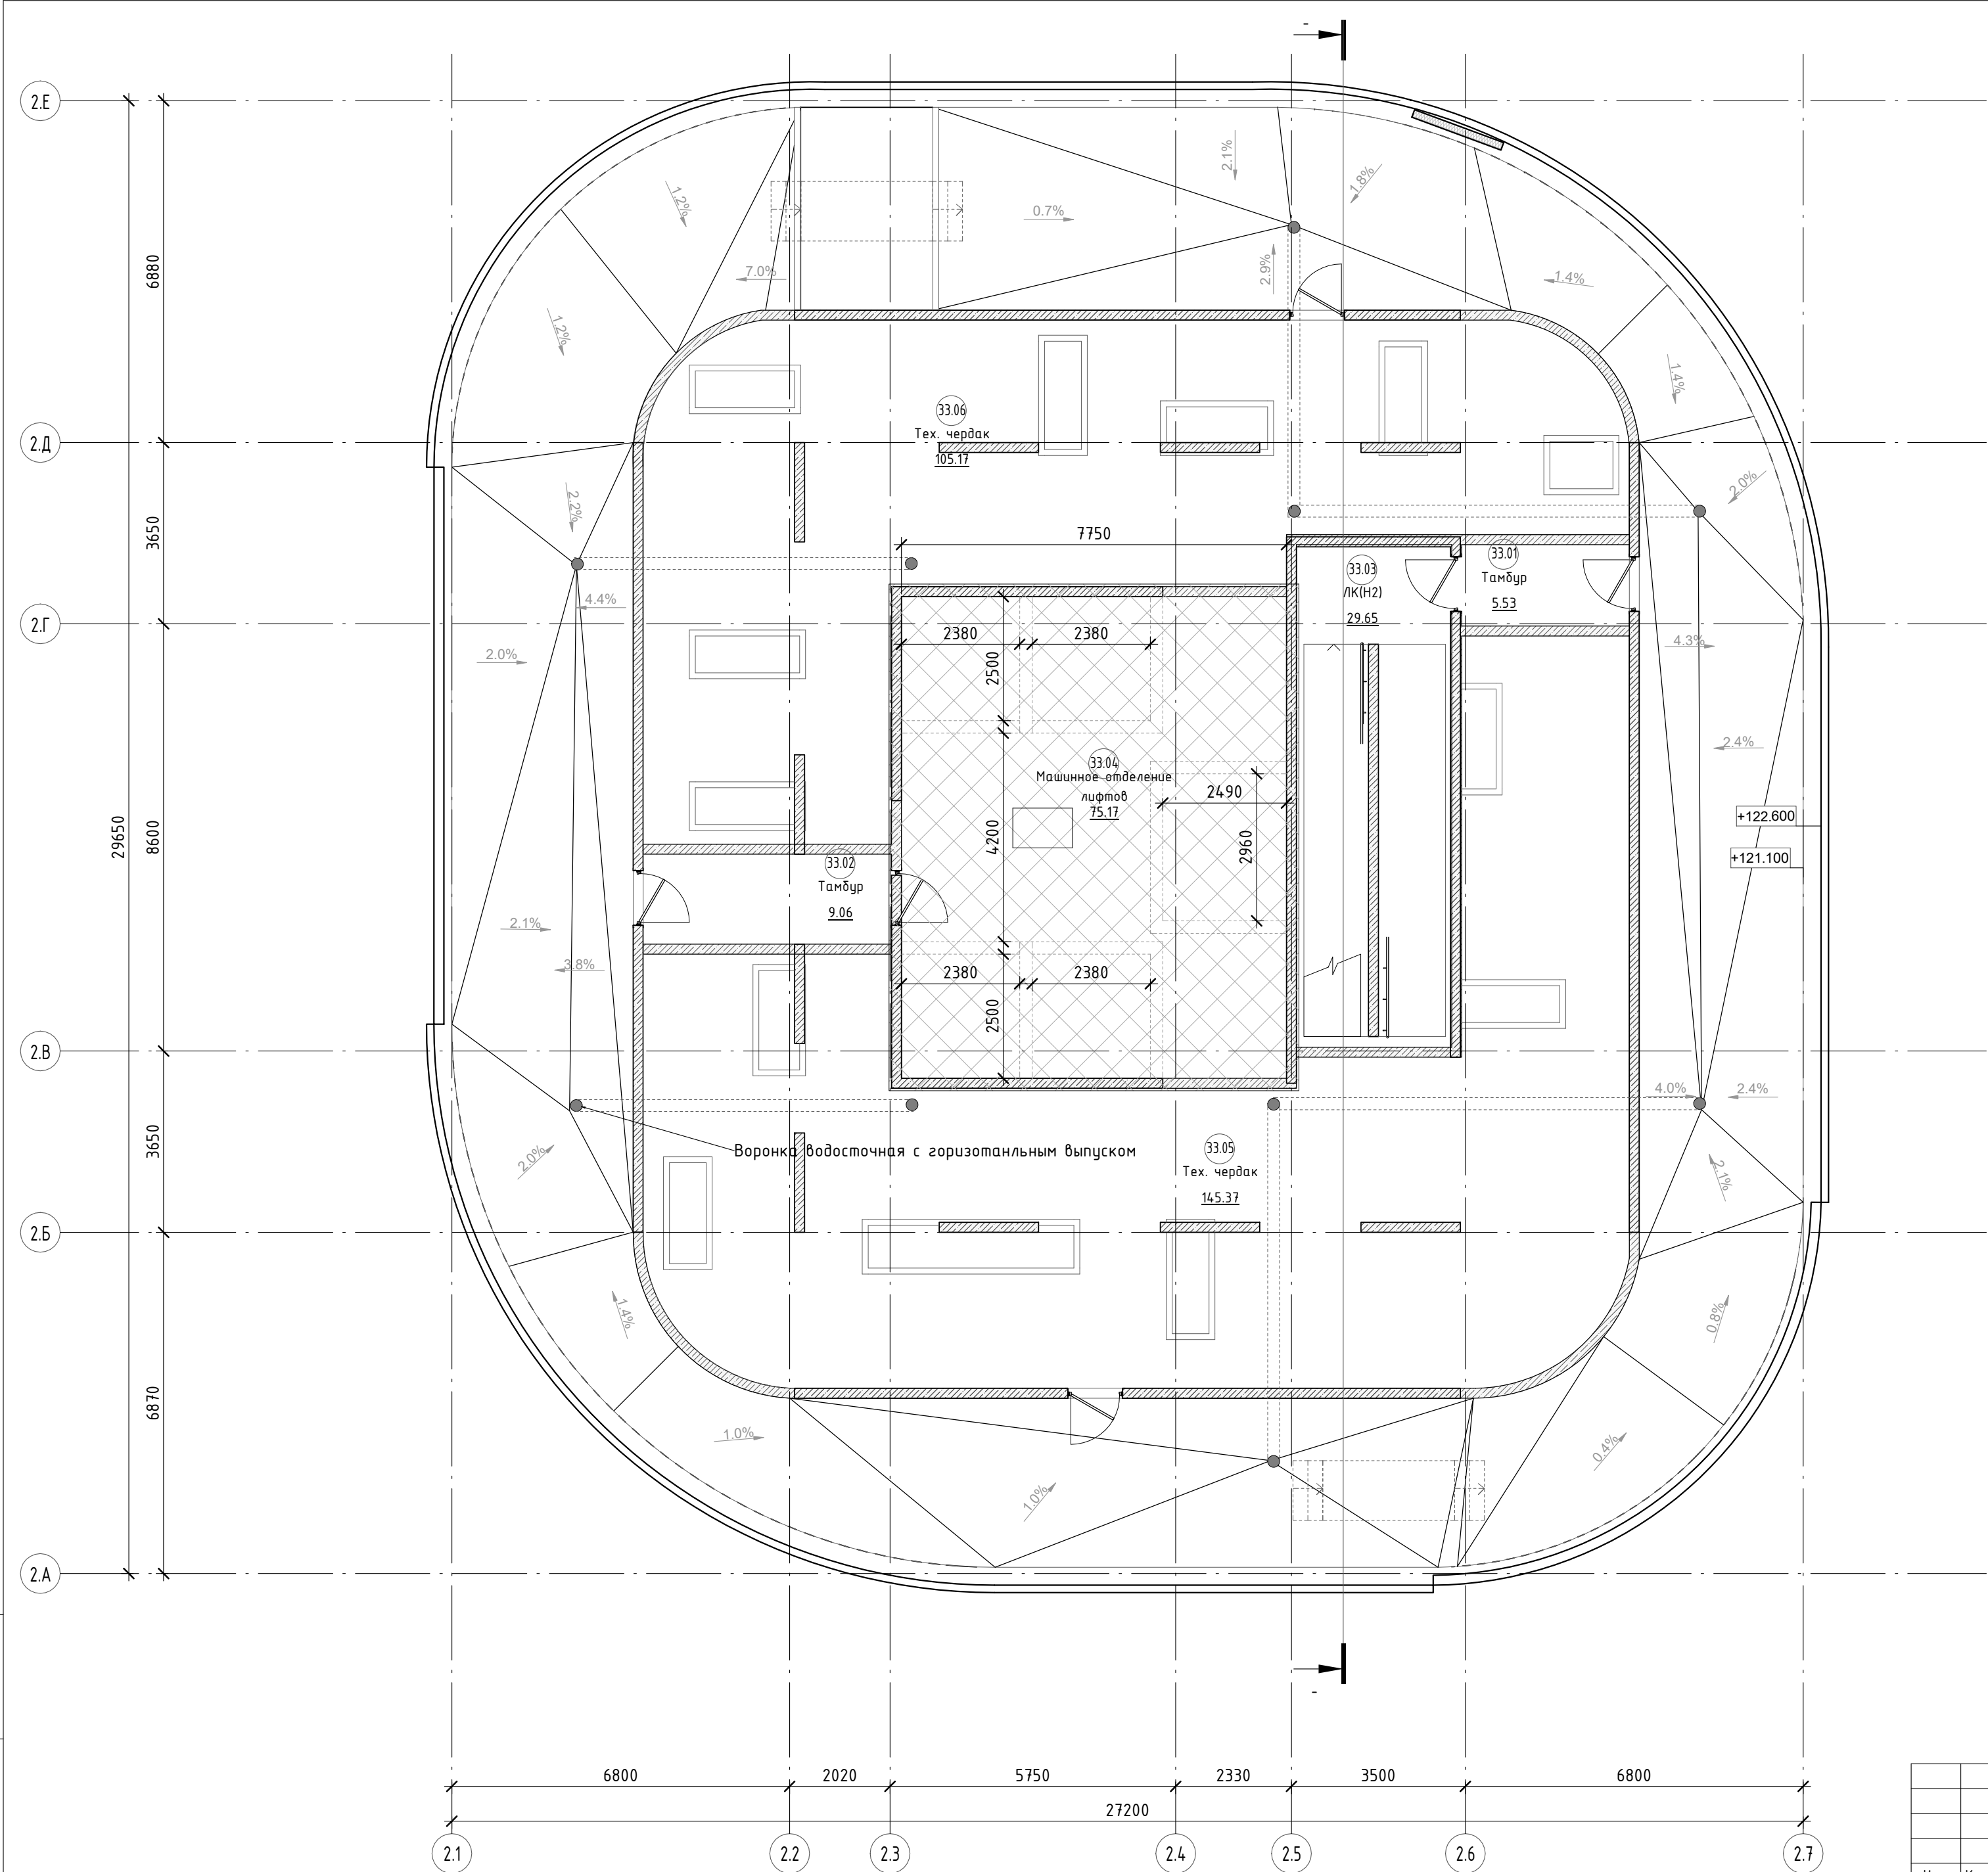

МОП			
33.01	Тамбур	5.53	
33.02	Тамбур	9.06	
33.03	ЛК(Н2)	29.65	
33.04	Машинное отделение лифтов	75.17	Д
33.05	Тех. чердак	145.37	Д
33.06	Тех. чердак	105.17	Д
		369.96	

ПО №8	Маш/пом	33
		32
		31
		30
		29
		28
		27
		26
		25
		24
ПО №7		23
		22
		21
		20
		19
		18
		17
		16
		15
		14
		13
		12
		11
		10
		9
		8
		7
		6
		5
		4
		3
		2
		1
автостоянка		-1

						1506-2026-AP			
						Корпус К-2			
Изм.	Кол.уч.	Лист	№ док.	Подп.	Дата	Архитектурные решения	Стадия	Лист	Листов
Разработал		Балобырина			03.26		ПД	33	
Проверил		Прилуцкая			03.26				
						План тех. этажа	000 "ПБ Р1"		
ГИП		Кочнева			03.26				
Н.Контроль		Ситчихина			03.26				