


План -1 этажа

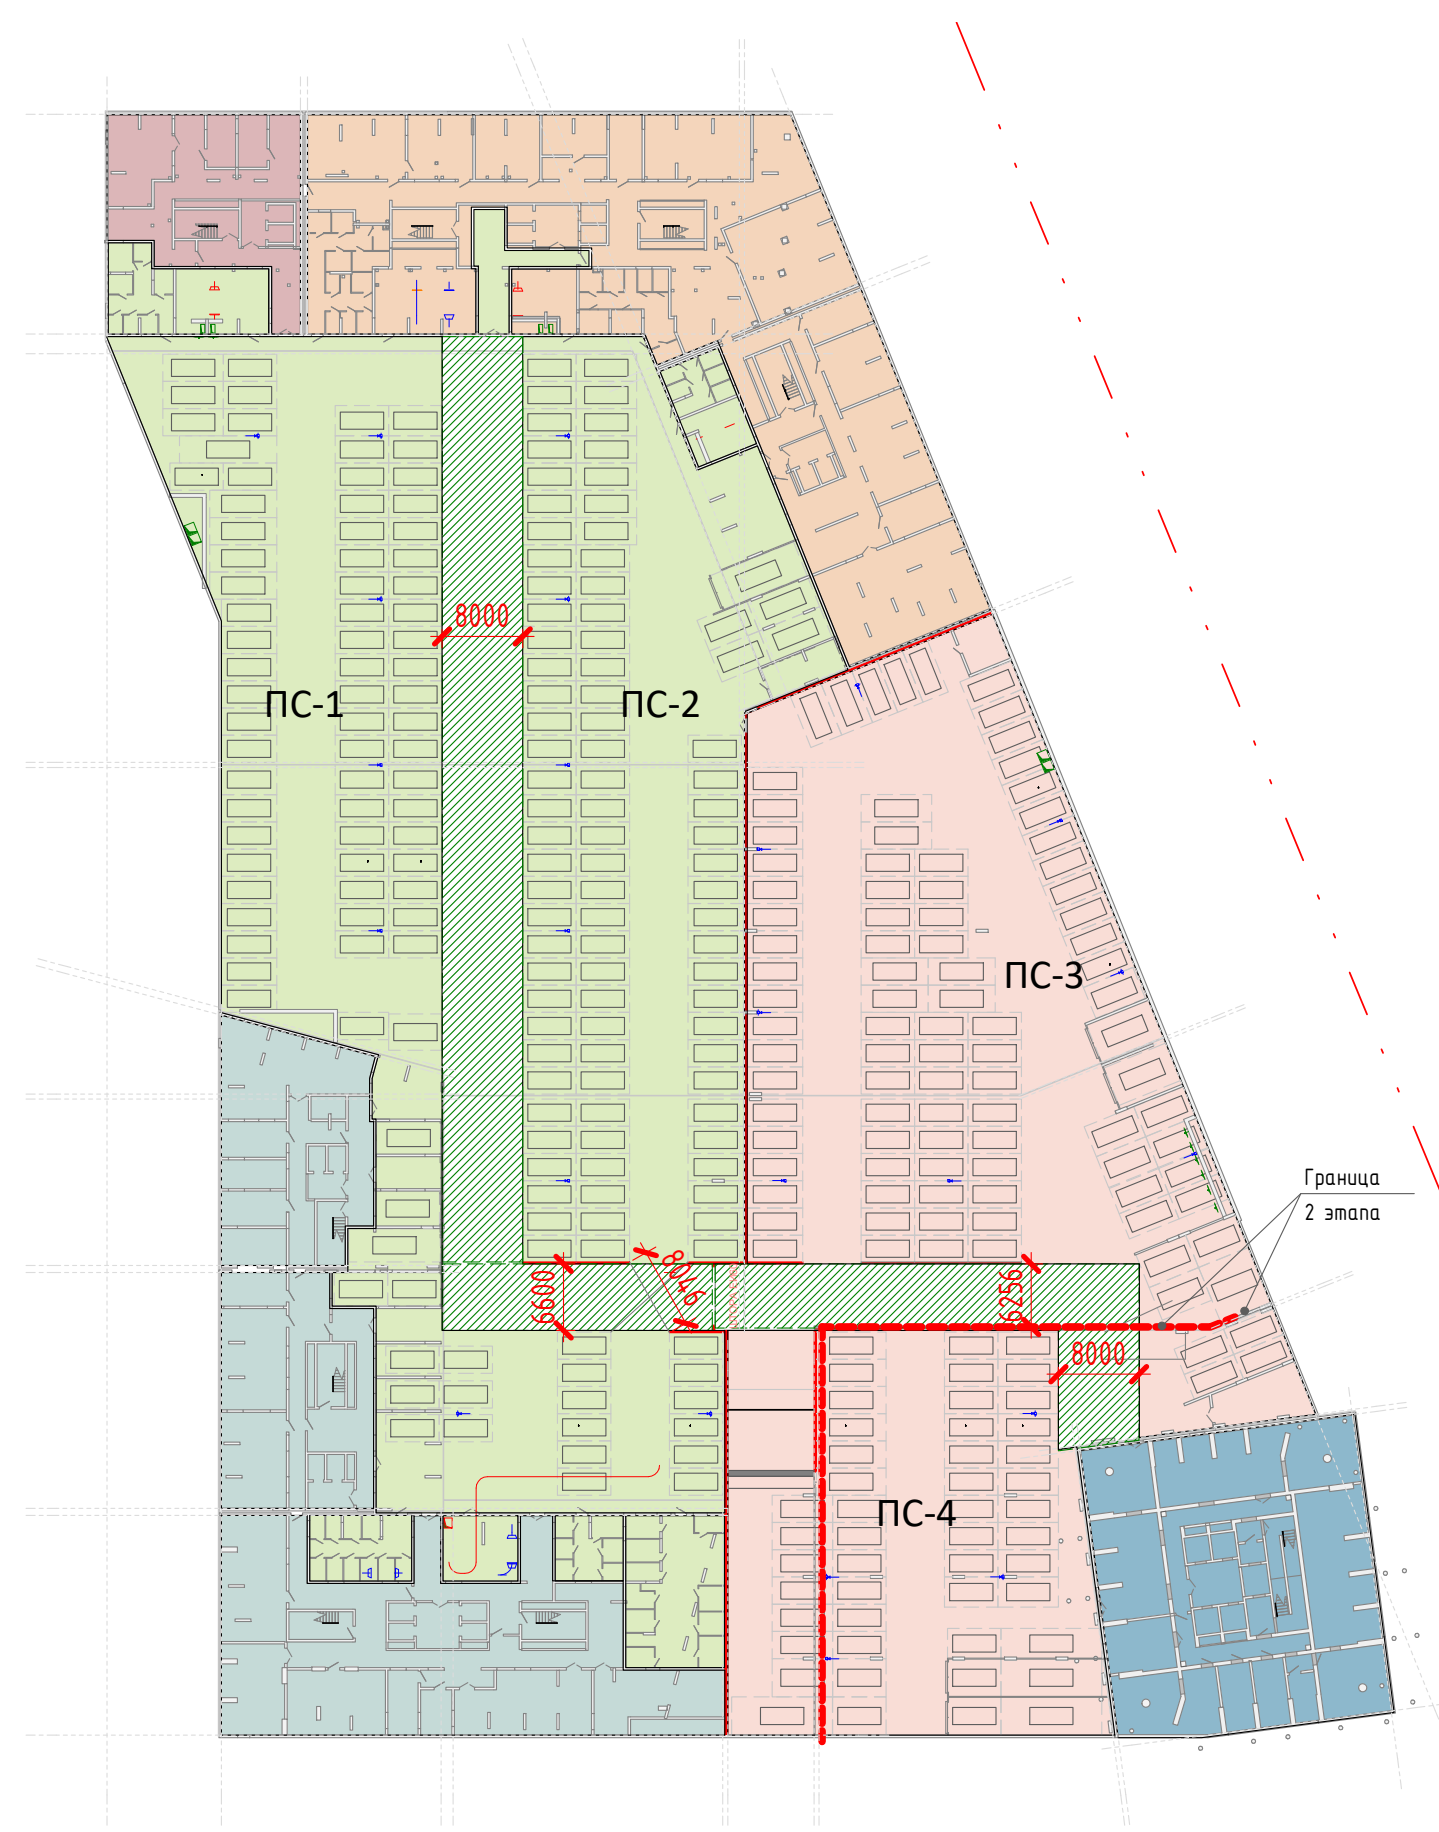

План 1 этажа

План 1 этажа

ПО №4

ПО №5

ПО №6

ПО №7

ПО №3

ПО №5

ПО №6

ПО №7

Выход в обходоулку после входа 1 этаж

Выход в обходоулку после входа 2 этаж

Граница 2 этажа



План 2 этажа



ПО №4

ПО №5

ПО №6

ПО №7/8

Граница 2 этажа

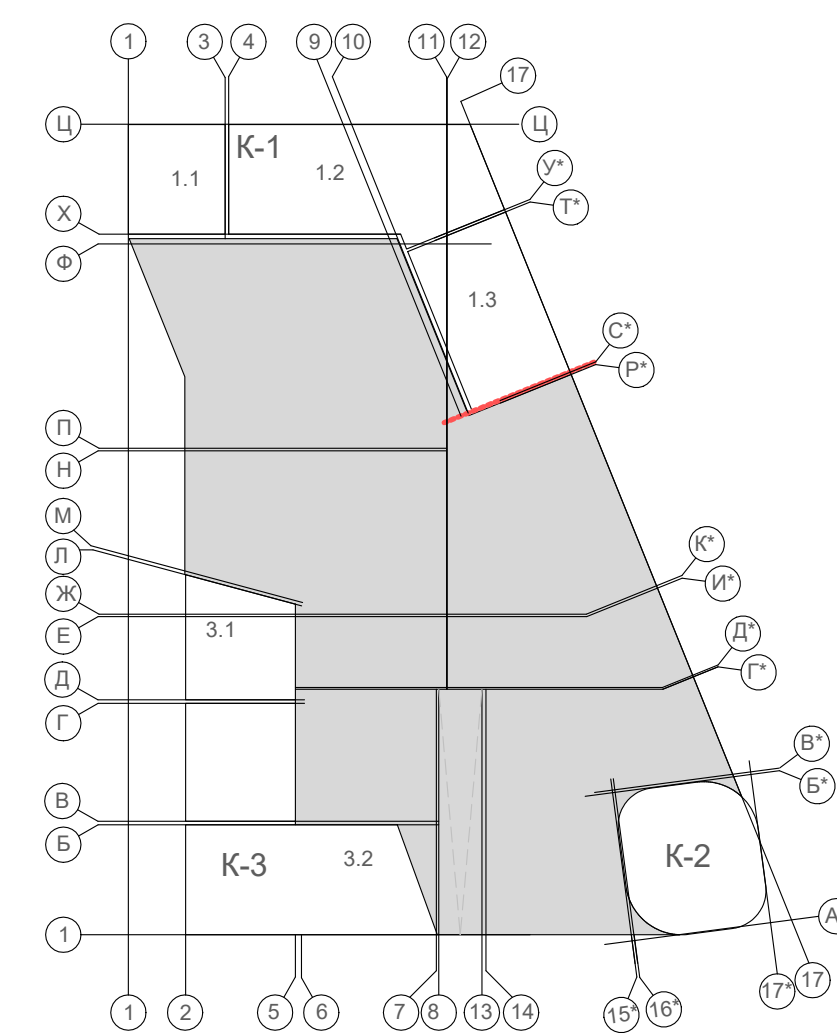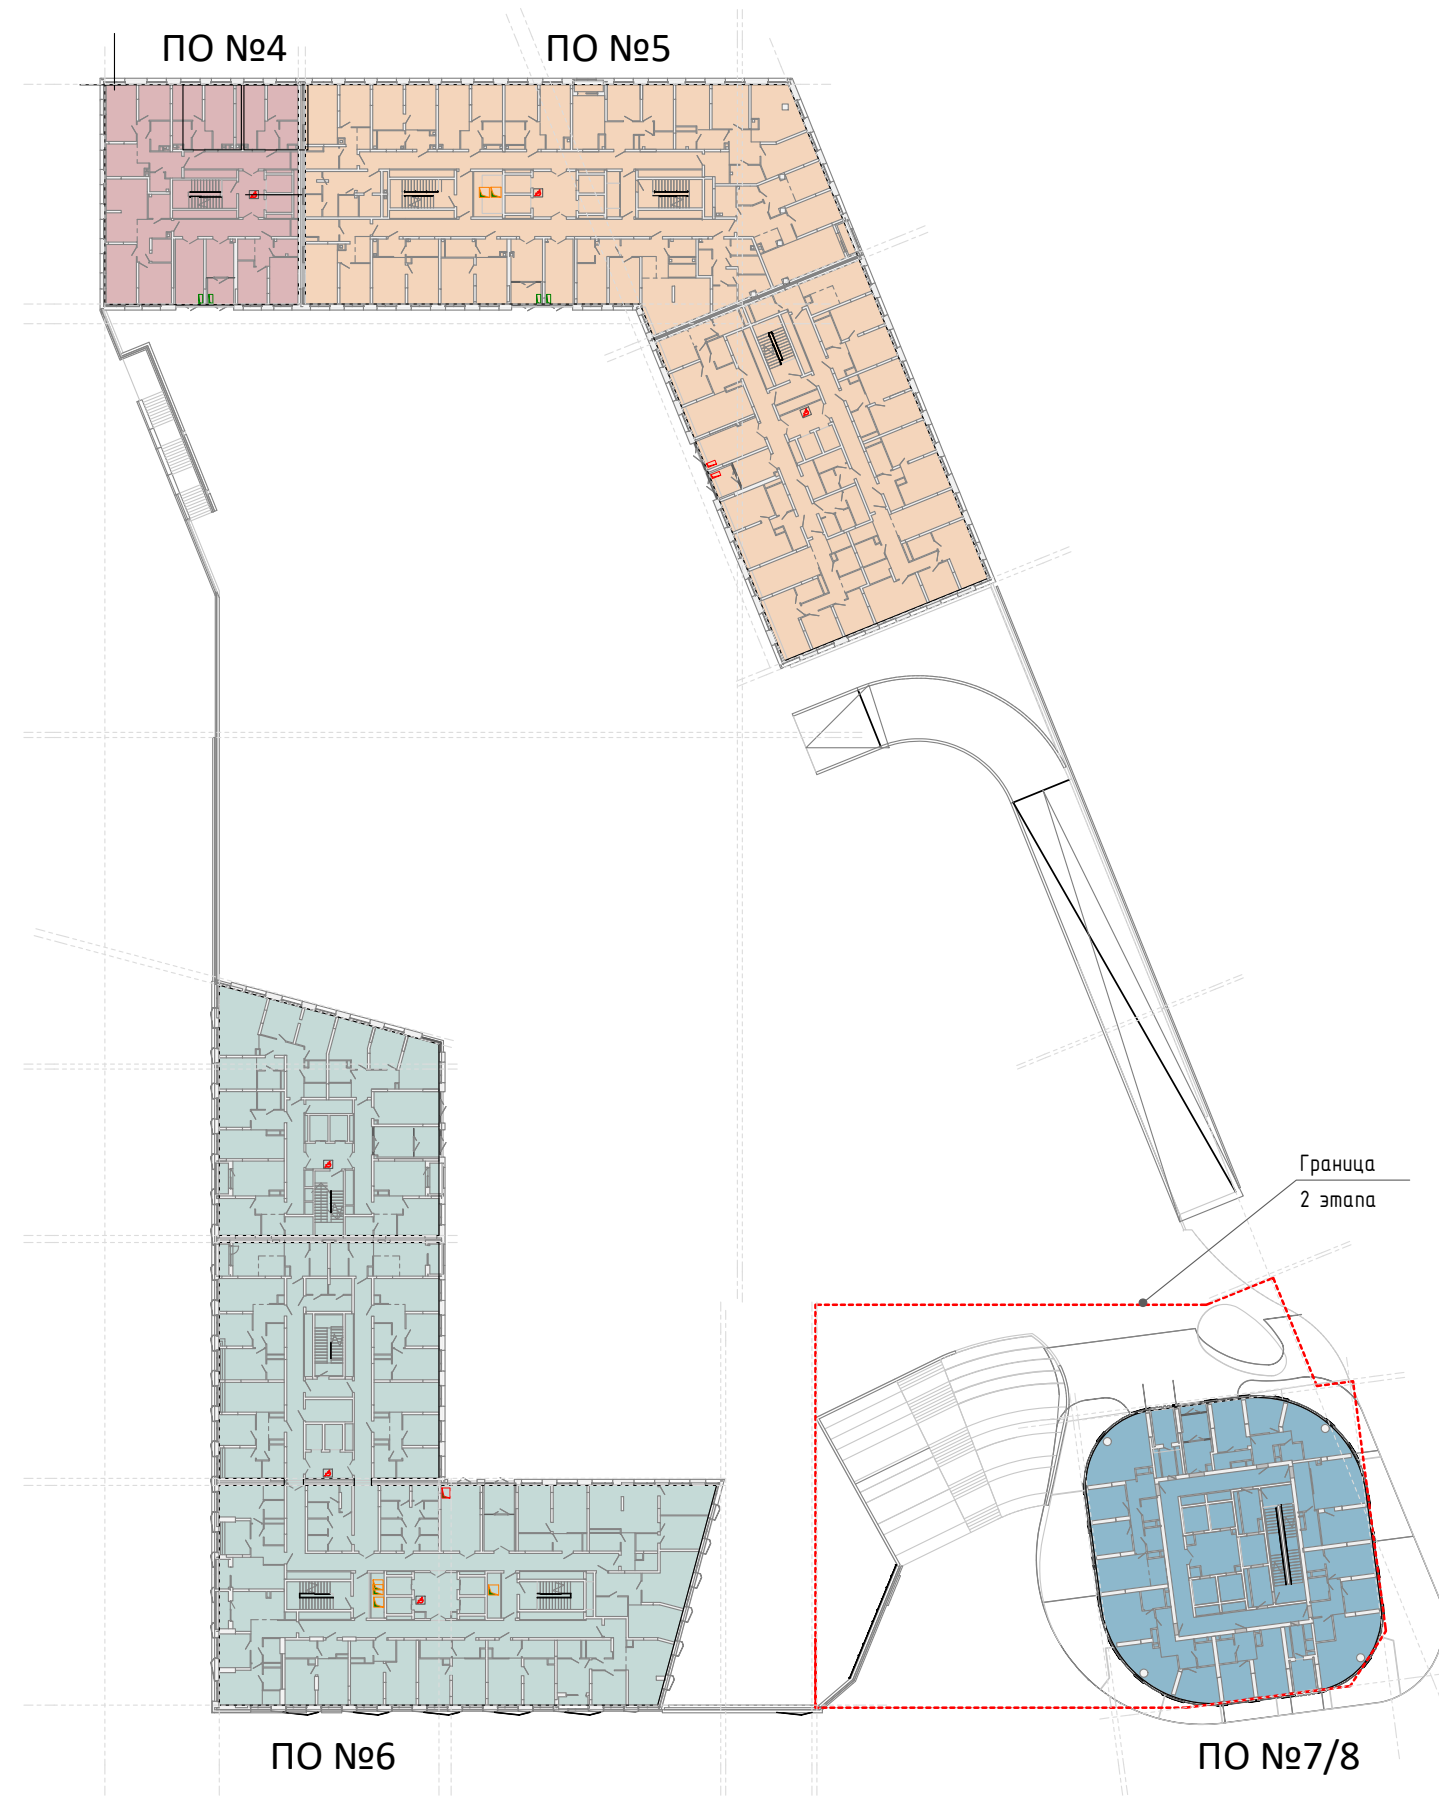

ПО №1	Встроенно-пристроенная подземная автостоянка Блоки кладовых Тех. помещения автостоянки	I/CO	1 этаж	ПО №1 ПС-1 ПС-2	5728,0 м2 2983,0 м2 2167,0 м2
ПО №2	Встроенно-пристроенная подземная автостоянка Блоки кладовых Тех. помещения автостоянки	I/CO	1 этаж	ПО №2 ПС-3 ПС-4	4199,0 м2 2530,0 м2 1423,0 м2
ПО №3	Встроенно-пристроенная наземная автостоянка Блоки кладовых Тех./служебные помещения автостоянки	I/CO	1 этаж	ПО №3 ПС-5 ПС-6 ПС-7	8566,5 м2 1935,0 м2 3129,5 м2 2870,5 м2
ПО №4	Жилой корпус К-1 секция 1.1	I/CO	10 этажей (в т.ч. подземный этаж)	ПО №4	418,5 м2
ПО №5	Жилой корпус К-1 секция 1.2-1.3	I/CO	18/20 этажей (в т.ч. подземный этаж и 20 этажей с размещением высолов на кровле)	ПО №5	1875,0 м2
ПО №6	Жилой корпус К-3 секции 3.1, 3.2	I/CO	10/10/18 этажей (в т.ч. подземный этаж и 20 этажей с размещением высолов на кровле)	ПО №6	2000,0 м2
ПО №7	Жилой корпус К-2 подземный, 1., 20 этажи высота пожарного отсека (по п. 5.3 СП 477.1325800.2020 не более 75 м)	I/CO	22 этажа (в т.ч. подземный этаж)	ПО №7	1180 м2
ПО №8	Жилой корпус К-2 21., 33 этажи высота пожарного отсека (по п. 5.3 СП 477.1325800.2020 не более 50 м)	I/CO	12 этажа	ПО №8	741,5 м2

К-1

до 50 м


до 100 м

ПО №4

ПО №5


1.1 1.2 1.3

29 28 27 26 25 24 23 22 21 20 19 18 17 16 15 14 13 12 11 10 9 8 7 6 5 4 3 2 1 -1

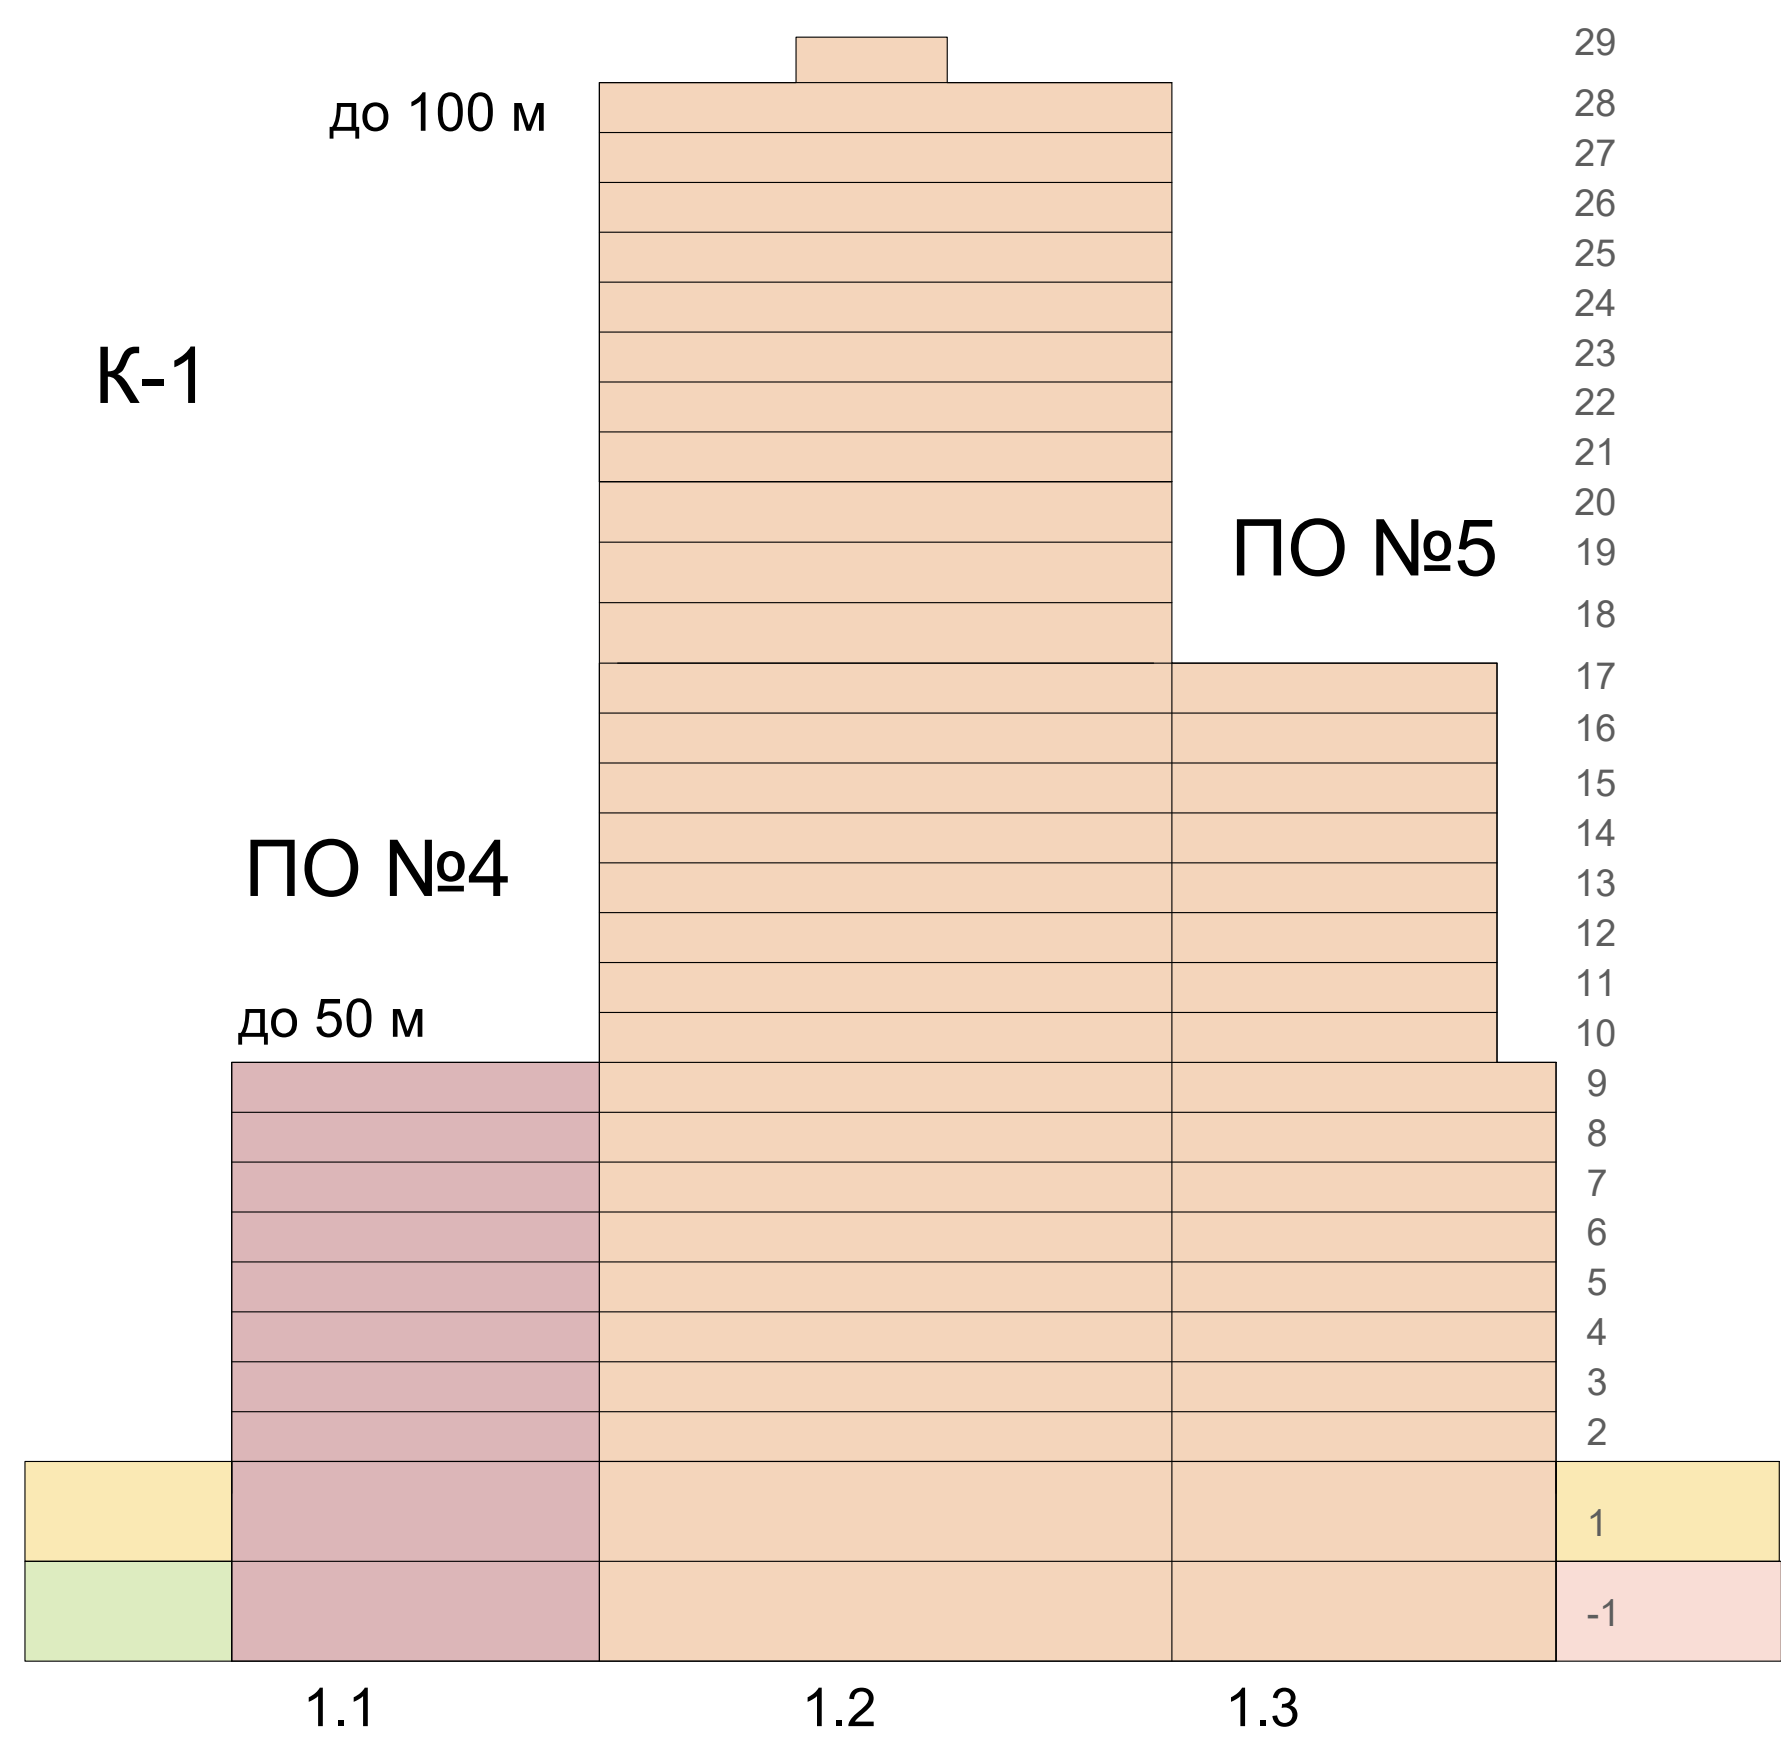


Technical drawing of a stepped profile with the following dimensions and labels:

- Top horizontal dimension: 123,6 м
- Second horizontal dimension: 117,3 м
- Third horizontal dimension: 74,1 м
- Vertical dimension on the left: 49,5 м
- Vertical dimension on the right: 6950
- Vertical dimension on the right: 13300
- Labels: ПО №8, К-2, ПО №7
- Top right label: 33 Маши/р/с.
- Bottom right label: -1

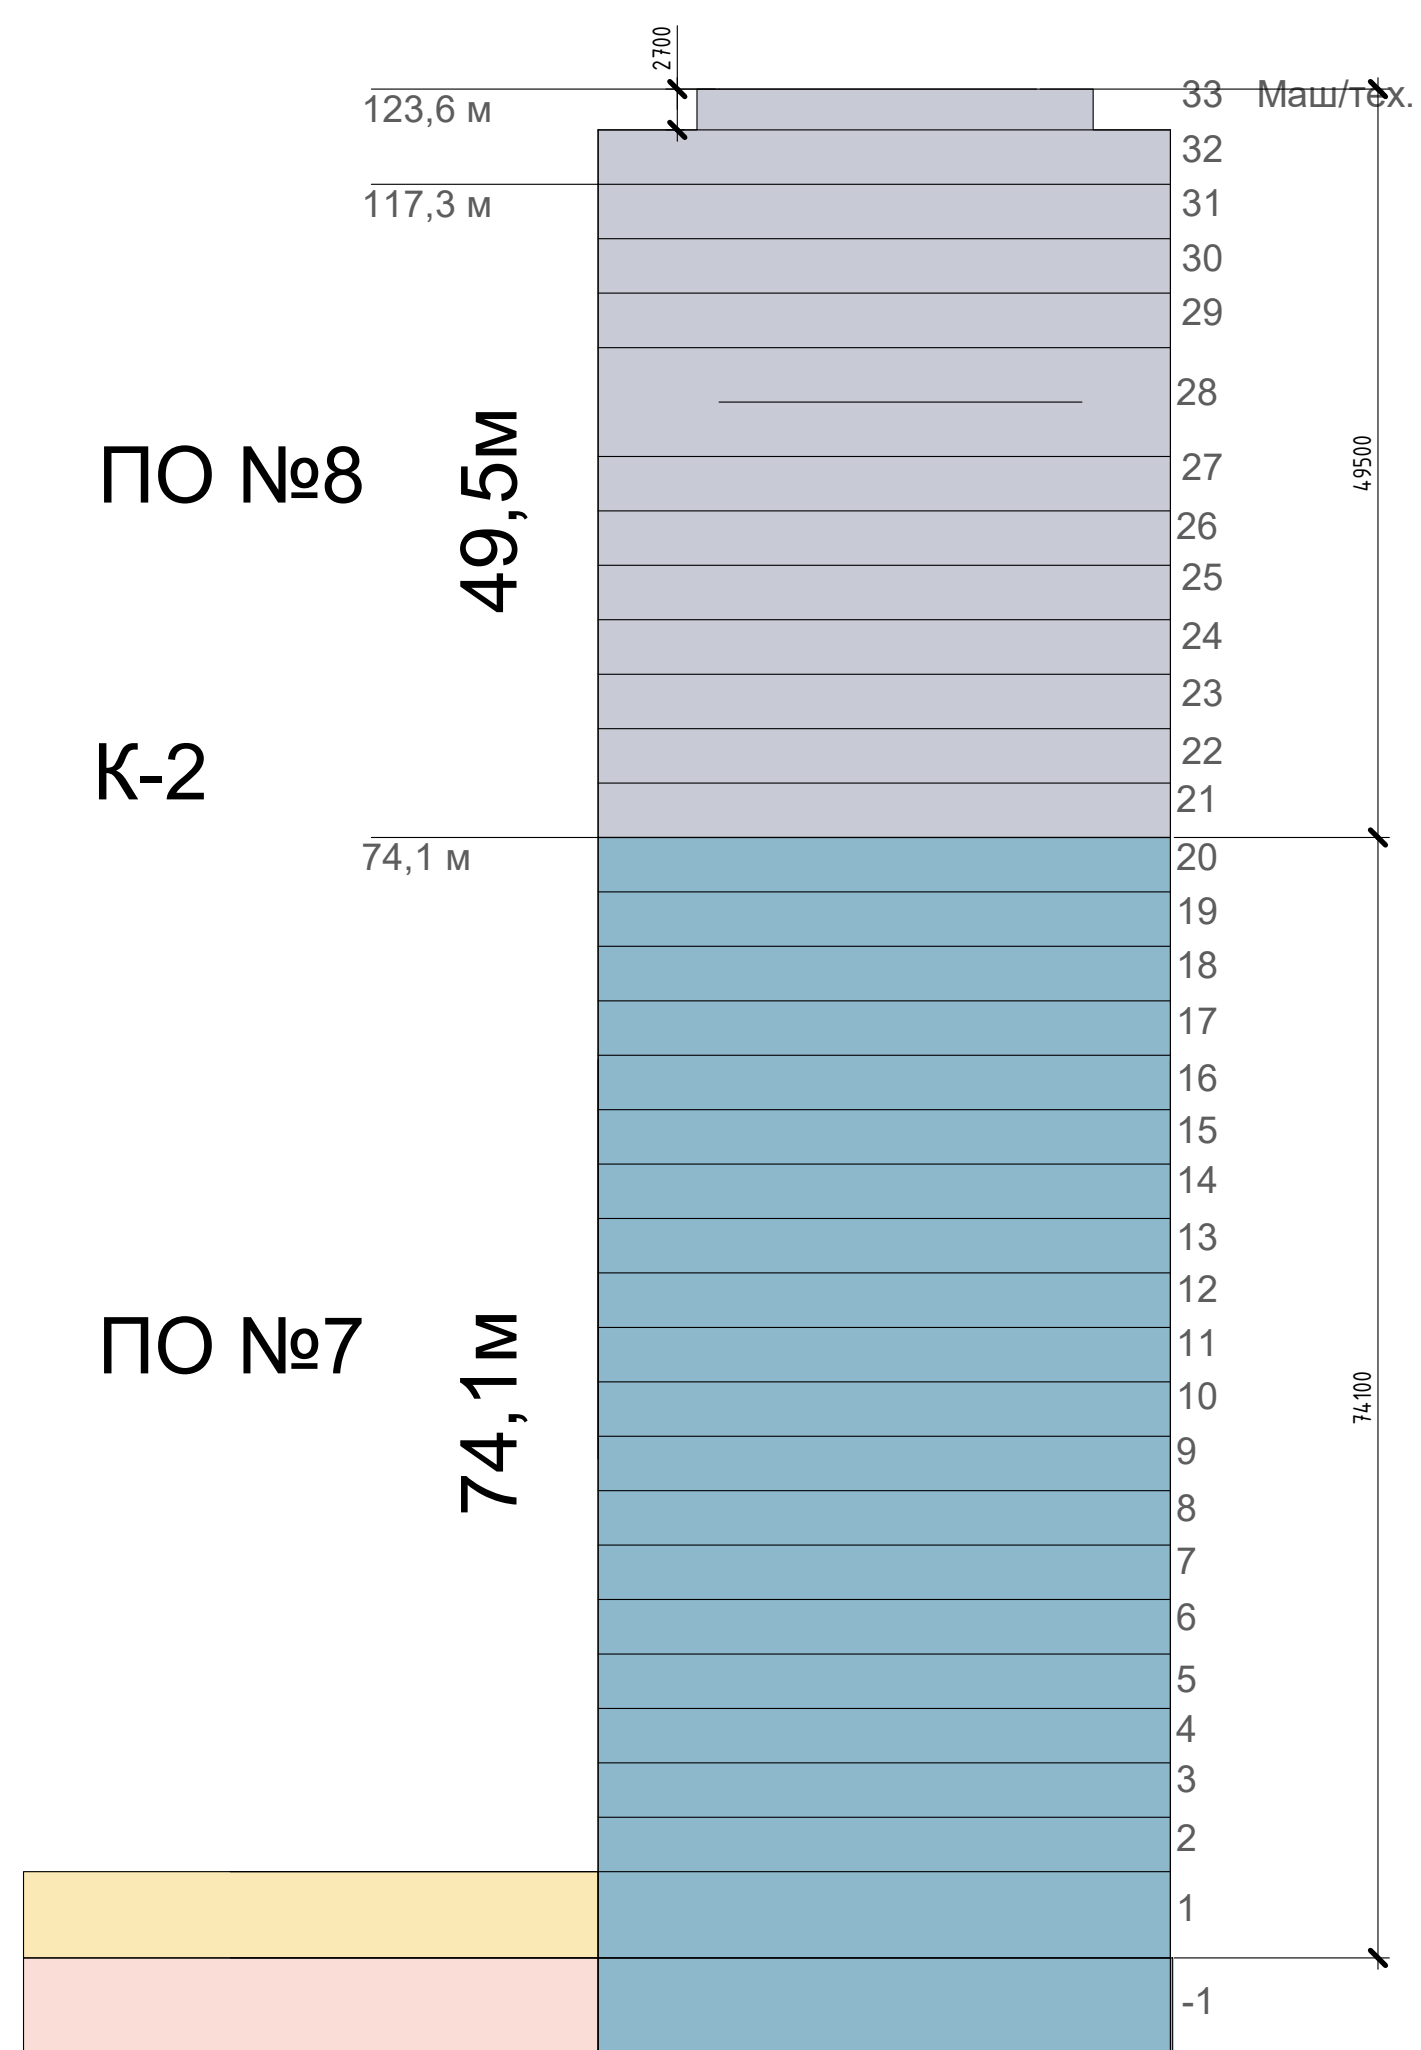


The figure is a 3D bar chart representing the height profile of the K-3 PO №6 building. The vertical axis (Z-axis) is labeled from -1 to 29 in increments of 1. The horizontal axis (X-axis) is divided into three sections: 3.1, 3.2, and 3.3. Section 3.1 has a height of 50 meters, section 3.2 has a height of 100 meters, and section 3.3 has a height of 17 meters. The bars are colored in a gradient from light blue at the base to light green at the top. The chart is titled 'К-3' and 'ПО №6'.

Section	Height (m)
3.1	50
3.2	100
3.3	17

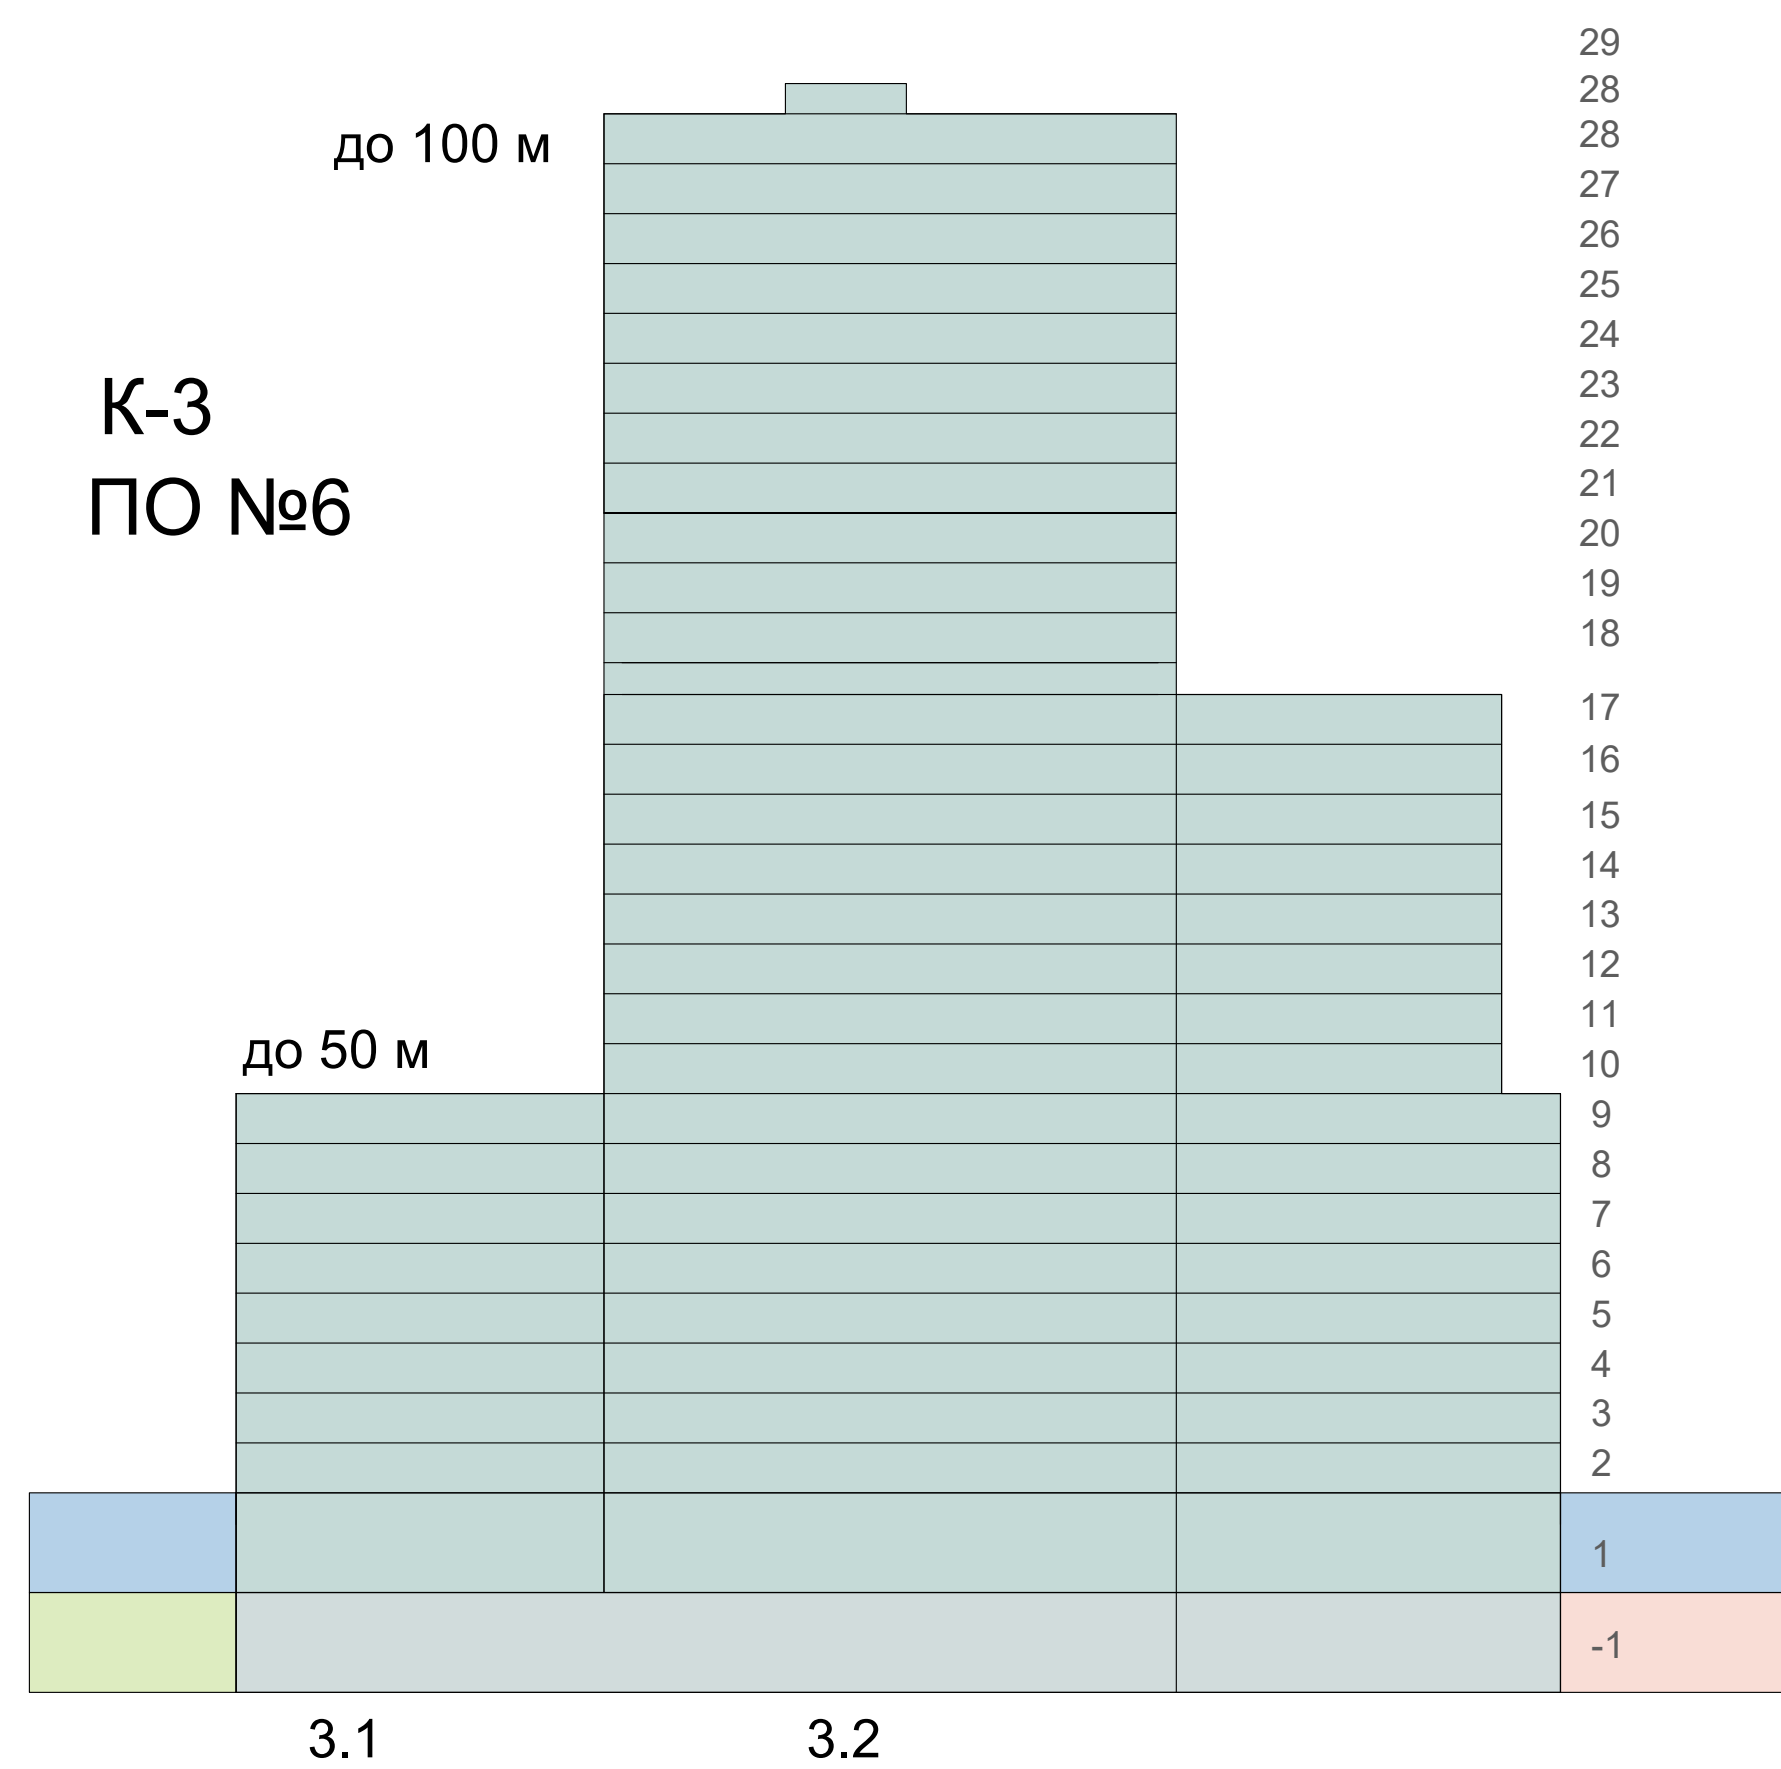

							АР-00
Изм.	Колоск.	Лист	В док.	Подп.	Дата		
						Архитектурные решения Архитектурные решения Абсолютского	Страницы Лист Листов П 1
						Схемы деления комплекса на ПО	Проектное бюро РТ

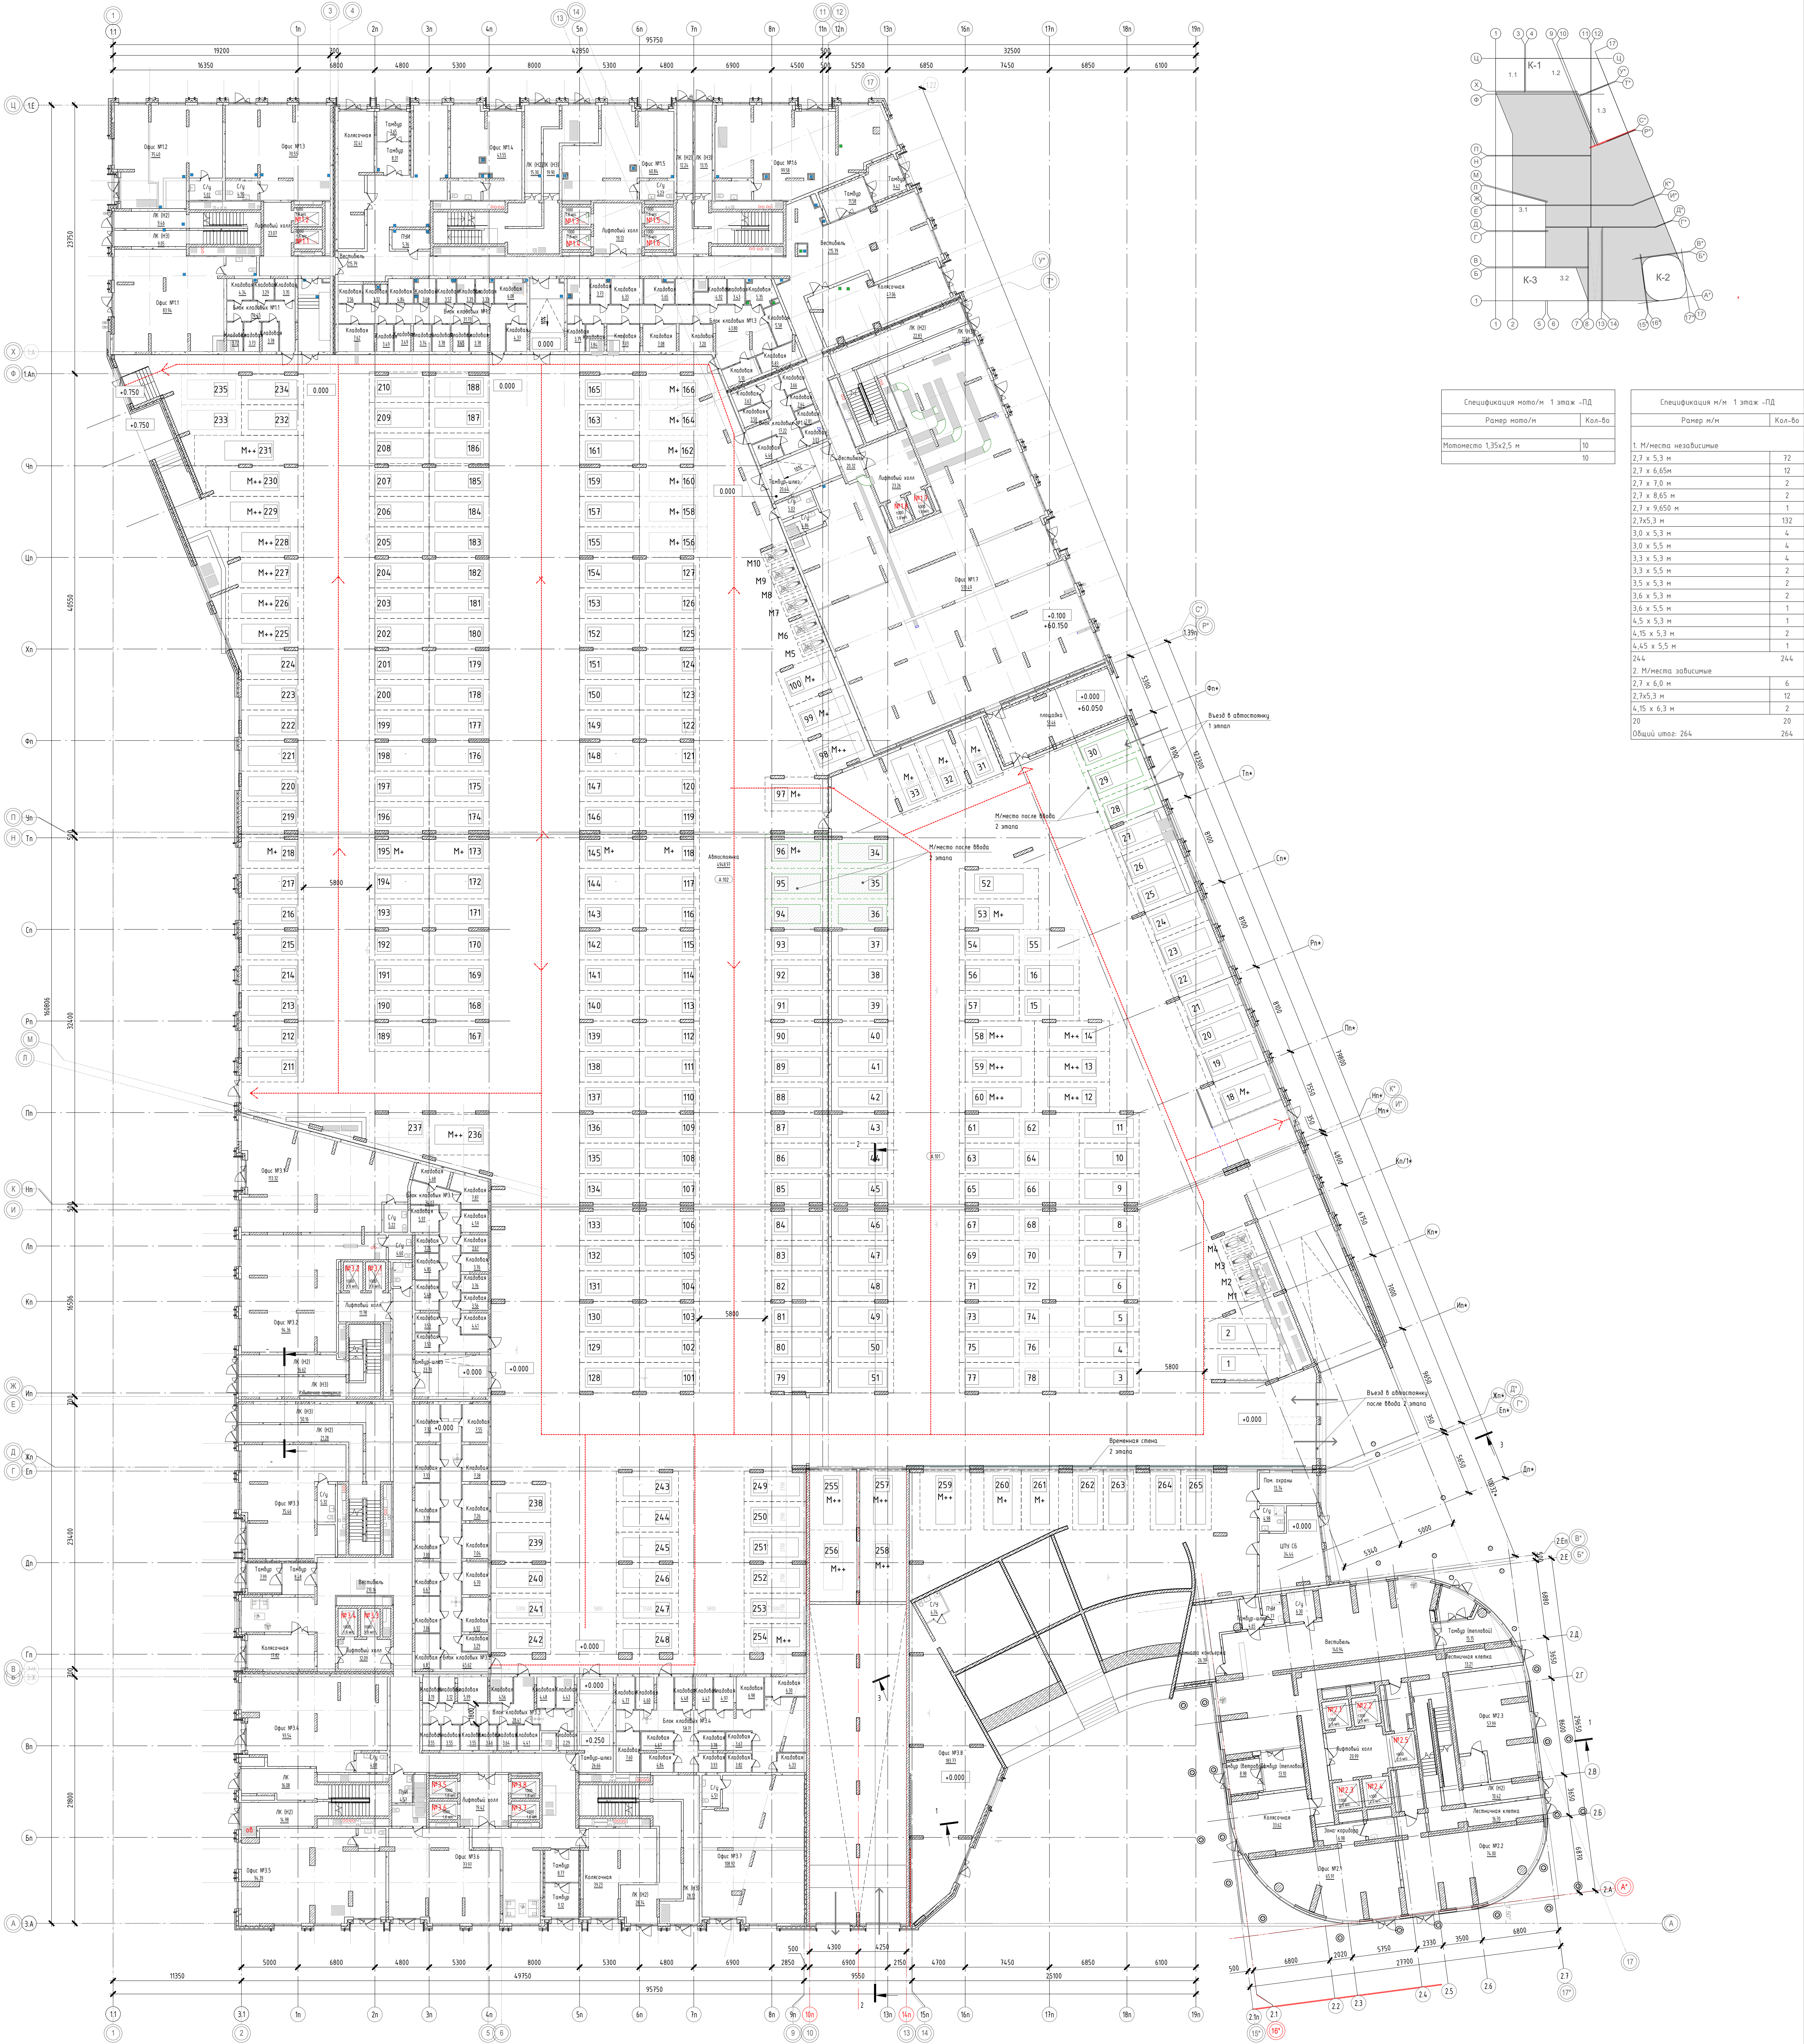

Спецификация н/м 1 этаж -ПД	
Размер н/м	Кол-во
Материал 1,35x2,5 м	10
Материал 1,35x2,5 м	10

Спецификация н/м 1 этаж -ПД	
Размер н/м	Кол-во
1. Места независимые	
2,7 x 5,3 м	72
2,7 x 6,65 м	12
2,7 x 8,0 м	2
2,7 x 8,65 м	2
2,7 x 9,65 м	1
2,7x5,3 м	132
3,0 x 5,3 м	4
3,0 x 5,5 м	4
3,3 x 5,3 м	4
3,5 x 5,3 м	2
3,5 x 5,5 м	2
3,6 x 5,3 м	1
4,5 x 5,3 м	1
4,5 x 5,5 м	2
4,5 x 5,5 м	1
244	244
2. Места зависимые	
2,7 x 5,0 м	6
2,7x5,3 м	12
4,15 x 6,3 м	2
20	20
Общий итог: 264	264



Спецификация м/м -1 этаж -ПД		
Размер м/м	Кол-во	
1. М/места независимые		
2,7 х 5,3 м	63	
2,7 х 6,0 м	2	
2,7 х 6,9 м	6	
2,7 х 6,95 м	8	
2,7 х 10,0 м	2	
2,7 х 9,650 м	1	
2,7х5,3 м	154	
3,0 х 5,3 м	8	
3,0 х 5,5 м	3	
3,2 х 5,3 м	1	
3,3 х 5,5 м	5	
3,3 х 5,5 м	2	
3,3 х 6,4 м	1	
3,3 х 9,1 м	1	
3,5 х 5,3 м	2	
3,6 х 5,3 м	1	
3,6 х 9,0 м	1	
3,8 х 5,3 м	4	
3,45 х 6,3 м	1	
4,0 х 6,6 м	2	
268	268	
2. М/места зависимые		
2,7 х 6,0 м	23	
2,7х5,3 м	22	
3,0 х 6,0 м	1	
3,0 х 10,0 м	1	
3,2 х 5,3 м	1	
3,3 х 5,5 м	2	
3,3 х 6,5 м	2	
3,5 х 5,3 м	1	
3,8 х 6,0 м	1	
3,8 х 10,0 м	3	
5,9 х 5,3 м	1	
58	58	
Общий итог:	326	

Абхазская. Экспликация помещений -1 этажа			
№ пом.	Наименование	Площадь, м2	Кат.
Абхазская			
A.001	Абхазская	5408.92	B2
A.002	Абхазская	4193.29	B2
Блок кладовых №16			
K.119	Кладовая	3.14	B4
K.120	Кладовая	3.20	B4
K.121	Кладовая	3.35	B4
K.122	Кладовая	3.47	B4
K.123	Кладовая	3.52	B4
K.1003	Блок кладовых №15	12.35	B4
Блок кладовых №17			
K.107	Кладовая	3.01	B4
K.108	Кладовая	3.12	B4
K.109	Кладовая	3.40	B4
K.110	Кладовая	4.05	B4
K.111	Кладовая	2.53	B4
K.112	Кладовая	5.04	B4
K.113	Кладовая	6.60	B4
K.114	Кладовая	3.76	B4
K.115	Кладовая	4.30	B4
K.116	Кладовая	6.65	B4
K.1002	Эвакуационный проход	36.71	B4
Блок кладовых №18			
K.100	Кладовая	3.17	B4
K.101	Кладовая	2.18	B4
K.102	Кладовая	2.69	B4
K.103	Кладовая	4.69	B4
K.104	Кладовая	7.03	B4
K.105	Кладовая	3.25	B4
K.106	Кладовая	4.75	B4
K.1001	Эвакуационный проход	21.06	B4
Всего:			
		494.2	

Абхазская. Экспликация помещений -1 этажа			
№ пом.	Наименование	Площадь, м2	Кат.
Блок кладовых №19			
K.160	Кладовая	4.81	B4
K.161	Кладовая	4.62	B4
K.162	Кладовая	3.17	B4
K.163	Кладовая	3.49	B4
K.164	Кладовая	7.08	B4
K.165	Кладовая	7.20	B4
K.166	Кладовая	4.42	B4
K.1005	Эвакуационный проход	26.92	B4
Блок кладовых №35			
K.1028	Кладовая	6.40	B4
K.1029	Кладовая	5.96	B4
K.1030	Кладовая	8.06	B4
K.1031	Кладовая	5.09	B4
K.1032	Кладовая	5.70	B4
K.1033	Кладовая	6.41	B4
K.1034	Кладовая	5.94	B4
K.1035	Кладовая	6.07	B4
K.1036	Кладовая	7.57	B4
K.1037	Кладовая	7.68	B4
K.3.001	Эвакуационный проход	75.30	B4
Блок кладовых №36			
K.148	Блок кладовых №35	24.71	B4
K.149	Кладовая	3.46	B4
K.150	Кладовая	3.48	B4
K.151	Кладовая	4.04	B4
K.152	Кладовая	4.13	B4
K.153	Кладовая	3.60	B4
K.154	Кладовая	3.60	B4
K.155	Кладовая	3.49	B4
K.156	Кладовая	3.84	B4
K.157	Кладовая	3.60	B4
K.158	Кладовая	3.60	B4
Всего:			
		615.4	

Абхазская. Экспликация помещений -1 этажа			
№ пом.	Наименование	Площадь, м2	Кат.
Блок кладовых №37			
K.142	Кладовая	3.89	B4
K.143	Кладовая	3.54	B4
K.144	Кладовая	3.69	B4
K.145	Кладовая	6.96	B4
K.146	Кладовая	4.78	B4
K.147	Кладовая	3.55	B4
K.3.002	Эвакуационный проход	15.11	B4
МПО			
M.1001	Тамбур-шлюз	40.32	
M.1002	Лифтовый холл (Тамбур-шлюз)	10.99	
M.1003	ЛК (ИЗ)	17.38	
M.1004	Коридор	103.70	
M.1005	Тамбур-шлюз	61.29	
M.1006	Лифтовый холл (Тамбур-шлюз)	17.53	
M.1007	ЛК (ИЗ)	18.44	
M.1008	ЛК (ЛП)	18.42	
M.1009	Коридор	269.82	
M.1010	Тамбур-шлюз	21.72	
M.1011	Лифтовый холл (Тамбур-шлюз)	10.92	
M.1012	ЛК (ИЗ)	17.78	
M.1013	Коридор	182.53	
M.2.001	Тамбур-шлюз	35.95	
M.2.002	Тамбур-шлюз	65.92	
M.2.003	Тамбур-шлюз	43.74	
M.2.004	Лифтовый холл (Тамбур-шлюз)	21.04	
M.2.005	Лифтовый холл (Тамбур-шлюз)	4.92	
M.2.006	ЛК (ИЗ)	17.10	
M.2.007	ЛК (ЛП)	15.39	
M.2.008	ЛК (ЛП)	9.25	
M.3.001	Тамбур-шлюз	31.40	
M.3.002	Лифтовый холл (Тамбур-шлюз)	9.43	
M.3.003	ЛК (ИЗ)	17.38	
M.3.004	Коридор	42.98	

Абхазская. Экспликация помещений -1 этажа			
№ пом.	Наименование	Площадь, м2	Кат.
M.3.005	Тамбур-шлюз	62.23	
M.3.006	Лифтовый холл (Тамбур-шлюз)	11.83	
M.3.007	ЛК (ИЗ)	17.12	
M.3.008	Коридор	54.39	
M.3.009	Тамбур-шлюз	72.35	
M.3.010	Лифтовый холл (Тамбур-шлюз)	19.42	
M.3.011	ЛК (ИЗ)	17.46	
M.3.012	ЛК (ЛП)	17.46	
M.3.013	Коридор	161.83	
Технические помещения			
T.1.001	Тех. подвал	Не размечено	Д
T.1.002	Электрощитовая	14.96	B4
T.1.003	Пом. связи	14.96	B4
T.1.004	Вентилятор ДУ	51.84	
T.1.005	ИТП	61.22	Д
T.1.006	Узел ввода ТС/коллекторная	40.96	Д
T.1.007	Вентилятор	40.38	Д
T.1.008	Пом. связи	25.58	B4
T.1.009	Электрощитовая	20.96	B4
T.1.010	Вентилятор ДУ	66.74	
T.1.011	Насосная	100.77	Д
T.1.012	Вентилятор ОВ	33.16	
T.1.013	Вентилятор ОВ	75.53	
T.1.014	Вентилятор ДУ	42.65	
T.1.015	Насосная ПП абхазская	136.10	
T.1.016	Электрощитовая абхазская	25.37	B4
T.1.017	Электрощитовая абхазская	19.69	
T.1.018	Электрощитовая	24.03	
T.1.019	Пом. связи	21.28	
T.1.020	Вентилятор ОВ	58.91	
T.1.021	Вентилятор ОВ	30.63	
T.2.003	Насосная	136.10	
T.2.004	ИТП	33.33	
T.2.005	Узел ввода ТС/коллекторная	61.18	

Абхазская. Экспликация помещений -1 этажа			
№ пом.	Наименование	Площадь, м2	Кат.
T.2.006	Электрощитовая 1	20.27	
T.2.007	Электрощитовая 2	20.34	
T.2.008	Помещение связи 1	11.98	
T.2.009	Тех. подвал	100.38	
T.2.010	Тех. подвал	44.26	
T.2.011	Вентилятор ОВ	42.12	
T.2.012	Вентилятор ДУ	100.75	
T.2.013	Тех. подвал	22.90	
T.2.014	Электрощитовая	18.38	
T.2.015	Пом. связи	22.25	
T.2.016	Вентилятор ПВД	48.19	
T.2.017	Тех. подвал	64.02	
T.2.018	Насосная узл-пильная	60.64	
T.2.019	Вентилятор ПВД	79.01	
T.2.020	Вентилятор ПВД	54.39	
T.2.021	Тех. подвал	61.80	
T.2.022	Пом. связи	19.35	
T.2.023	Электрощитовая	13.95	
T.2.024	ИТП	77.98	
T.2.025	Вентилятор ПВД	64.88	
T.2.026	Вентилятор ДУ	47.71	
T.2.027	Тех. подвал	Не размечено	
Всего: 145			
		2127.70	
		13758.12	